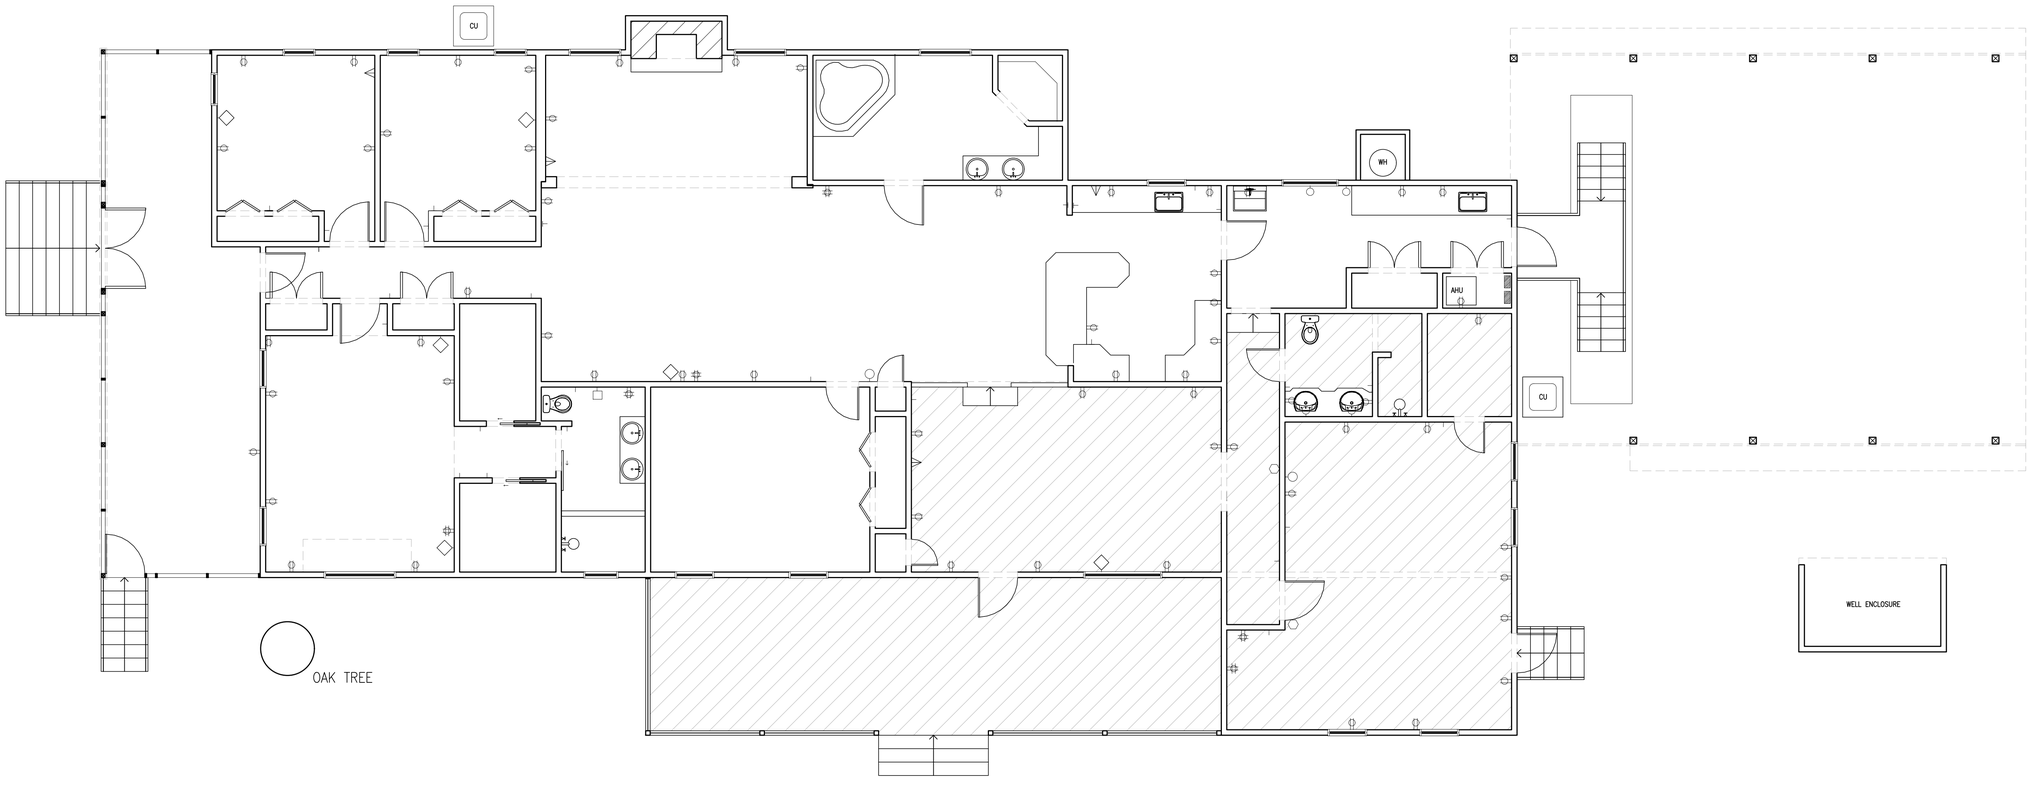


FLOOR PLAN - EXISTING

SCALE 3/16" = 1'-0"

LOWER FLOOR AREA

SeibertArchitects PA
1373Fifth Street Sarasota Florida 34236
tel 941.366.9765 fax 941.365.0902 lic AA C000070
www.seibertarchitects.com


RENOVATIONS TO THE
Red House

©Copyright Seibert Architects, P.A. All Rights Reserved

Date:	SEPTEMBER 3, 2026
Project:	2601
Rev. 1:	
Rev. 2:	
Rev. 3:	
Rev. 4	

A1.0

Sheet No.

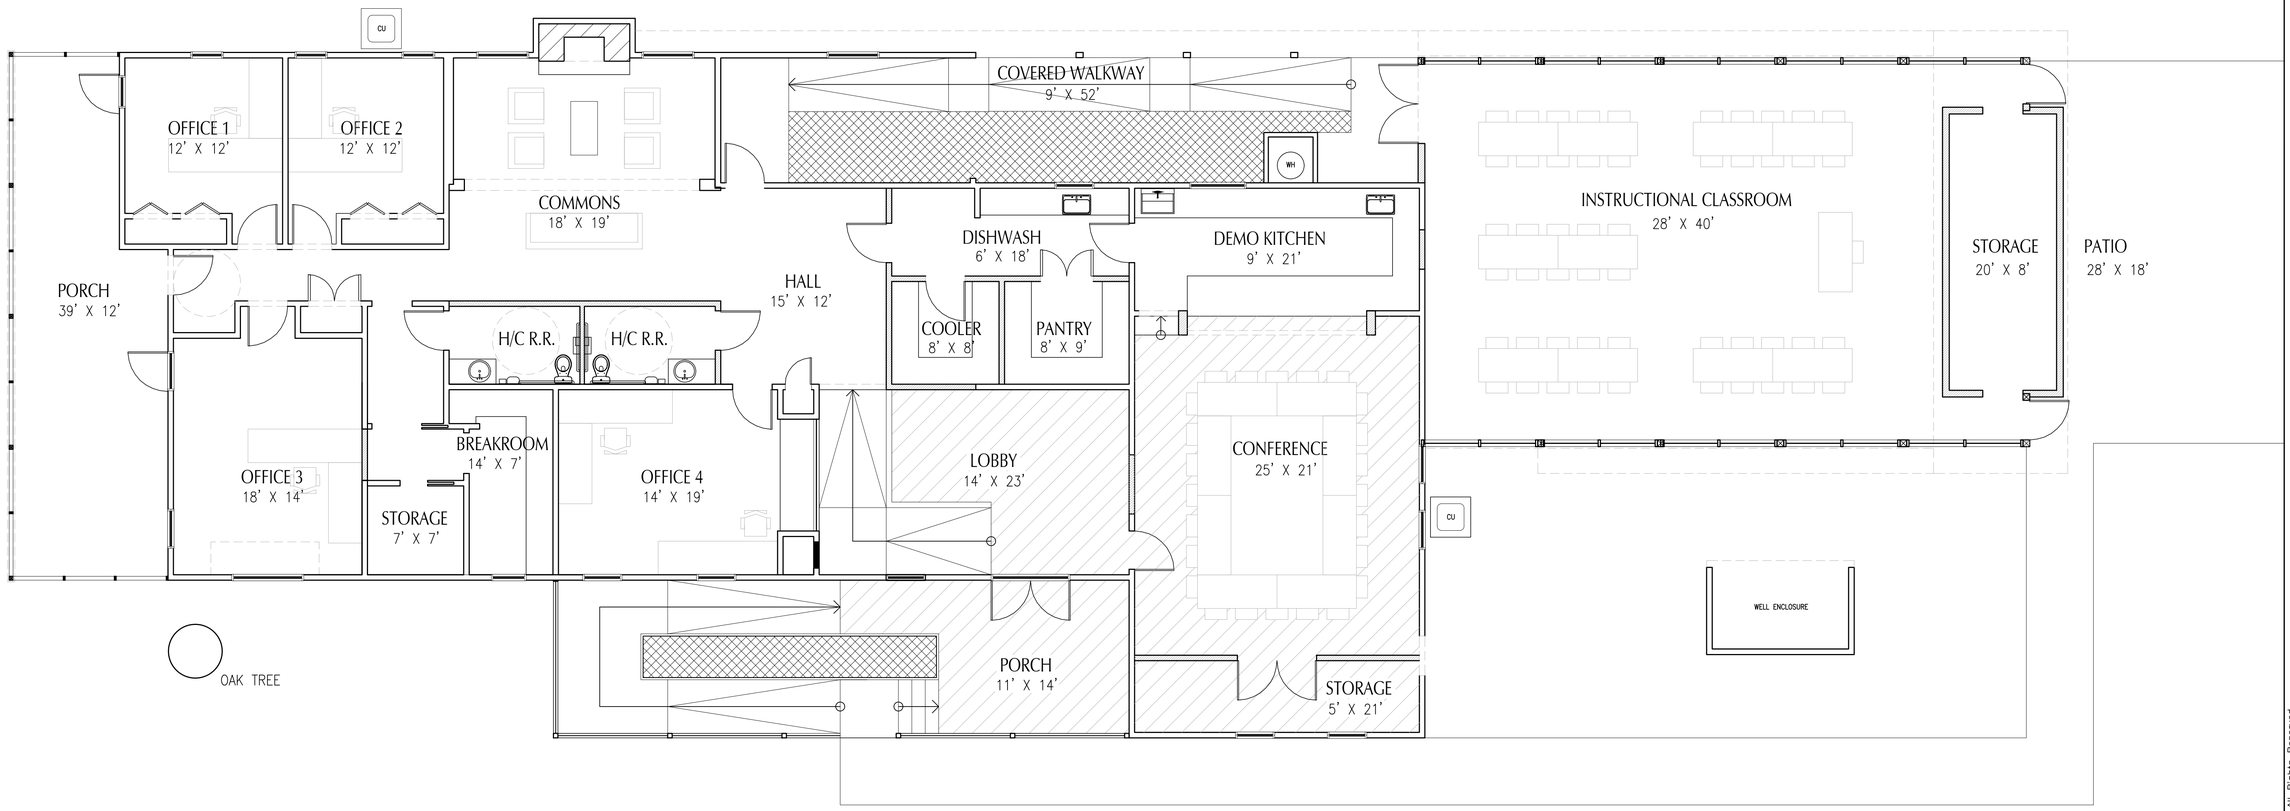

FLOOR PLAN - LEVEL 1

SCALE 3/16" = 1'-0"

LOWER FLOOR AREA

NEW WALLS

SeibertArchitects PA
1373 Fifth Street Sarasota Florida 34236
www.seibertarchitects.com tel 941.366.9765 fax 941.365.0902 lic AA C000070


RENOVATIONS TO THE
Red House

©Copyright Seibert Architects, P.A. All Rights Reserved

Date:	SEPTEMBER 3, 2026
Project:	2601
Rev. 1:	
Rev. 2:	
Rev. 3:	
Rev. 4	

A1.0-1

Sheet No.

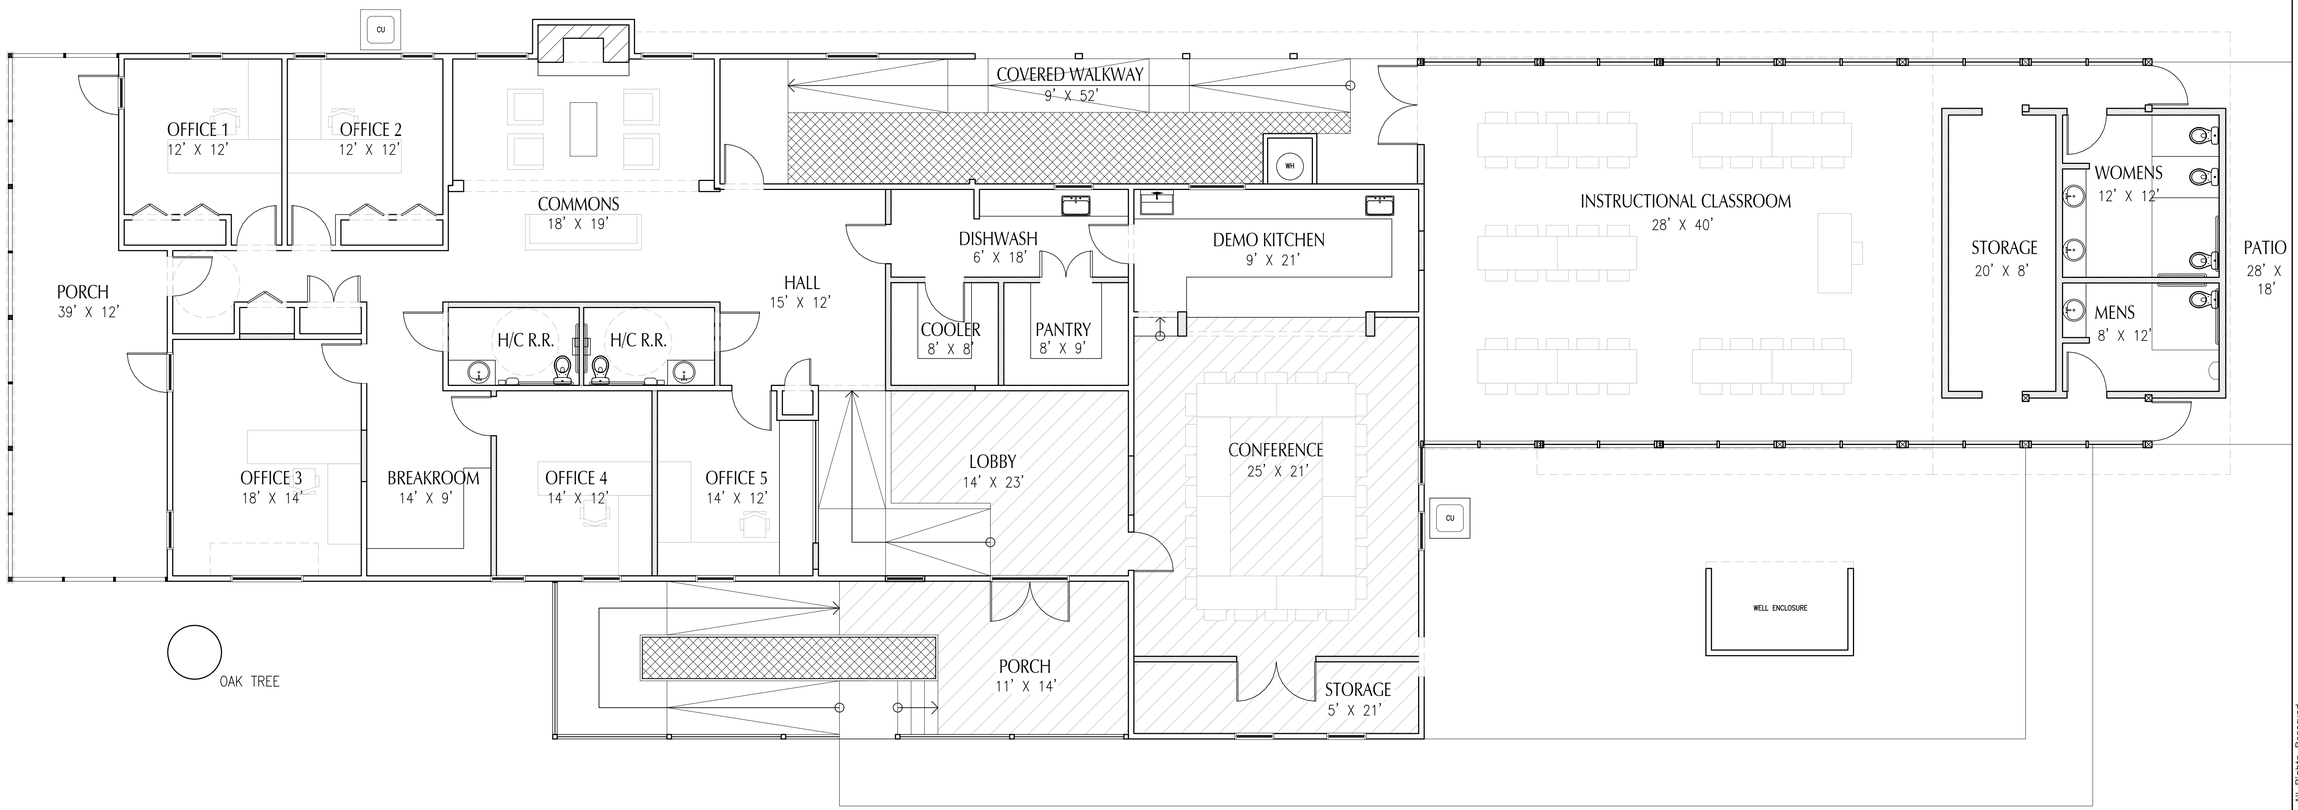

FLOOR PLAN - LEVEL 2

SCALE 3/16" = 1'-0"

LOWER FLOOR AREA

NEW WALLS

SeibertArchitects PA
1373 Fifth Street Sarasota Florida 34236
tel 941.366.9765 fax 941.365.0902 lic AA C000070
www.seibertarchitects.com


RENOVATIONS TO THE
Red House

© Copyright Seibert Architects, P.A. All Rights Reserved

Date:	SEPTEMBER 3, 2026
Project:	2601
Rev. 1:	
Rev. 2:	
Rev. 3:	
Rev. 4	

A1.0-2

Sheet No.

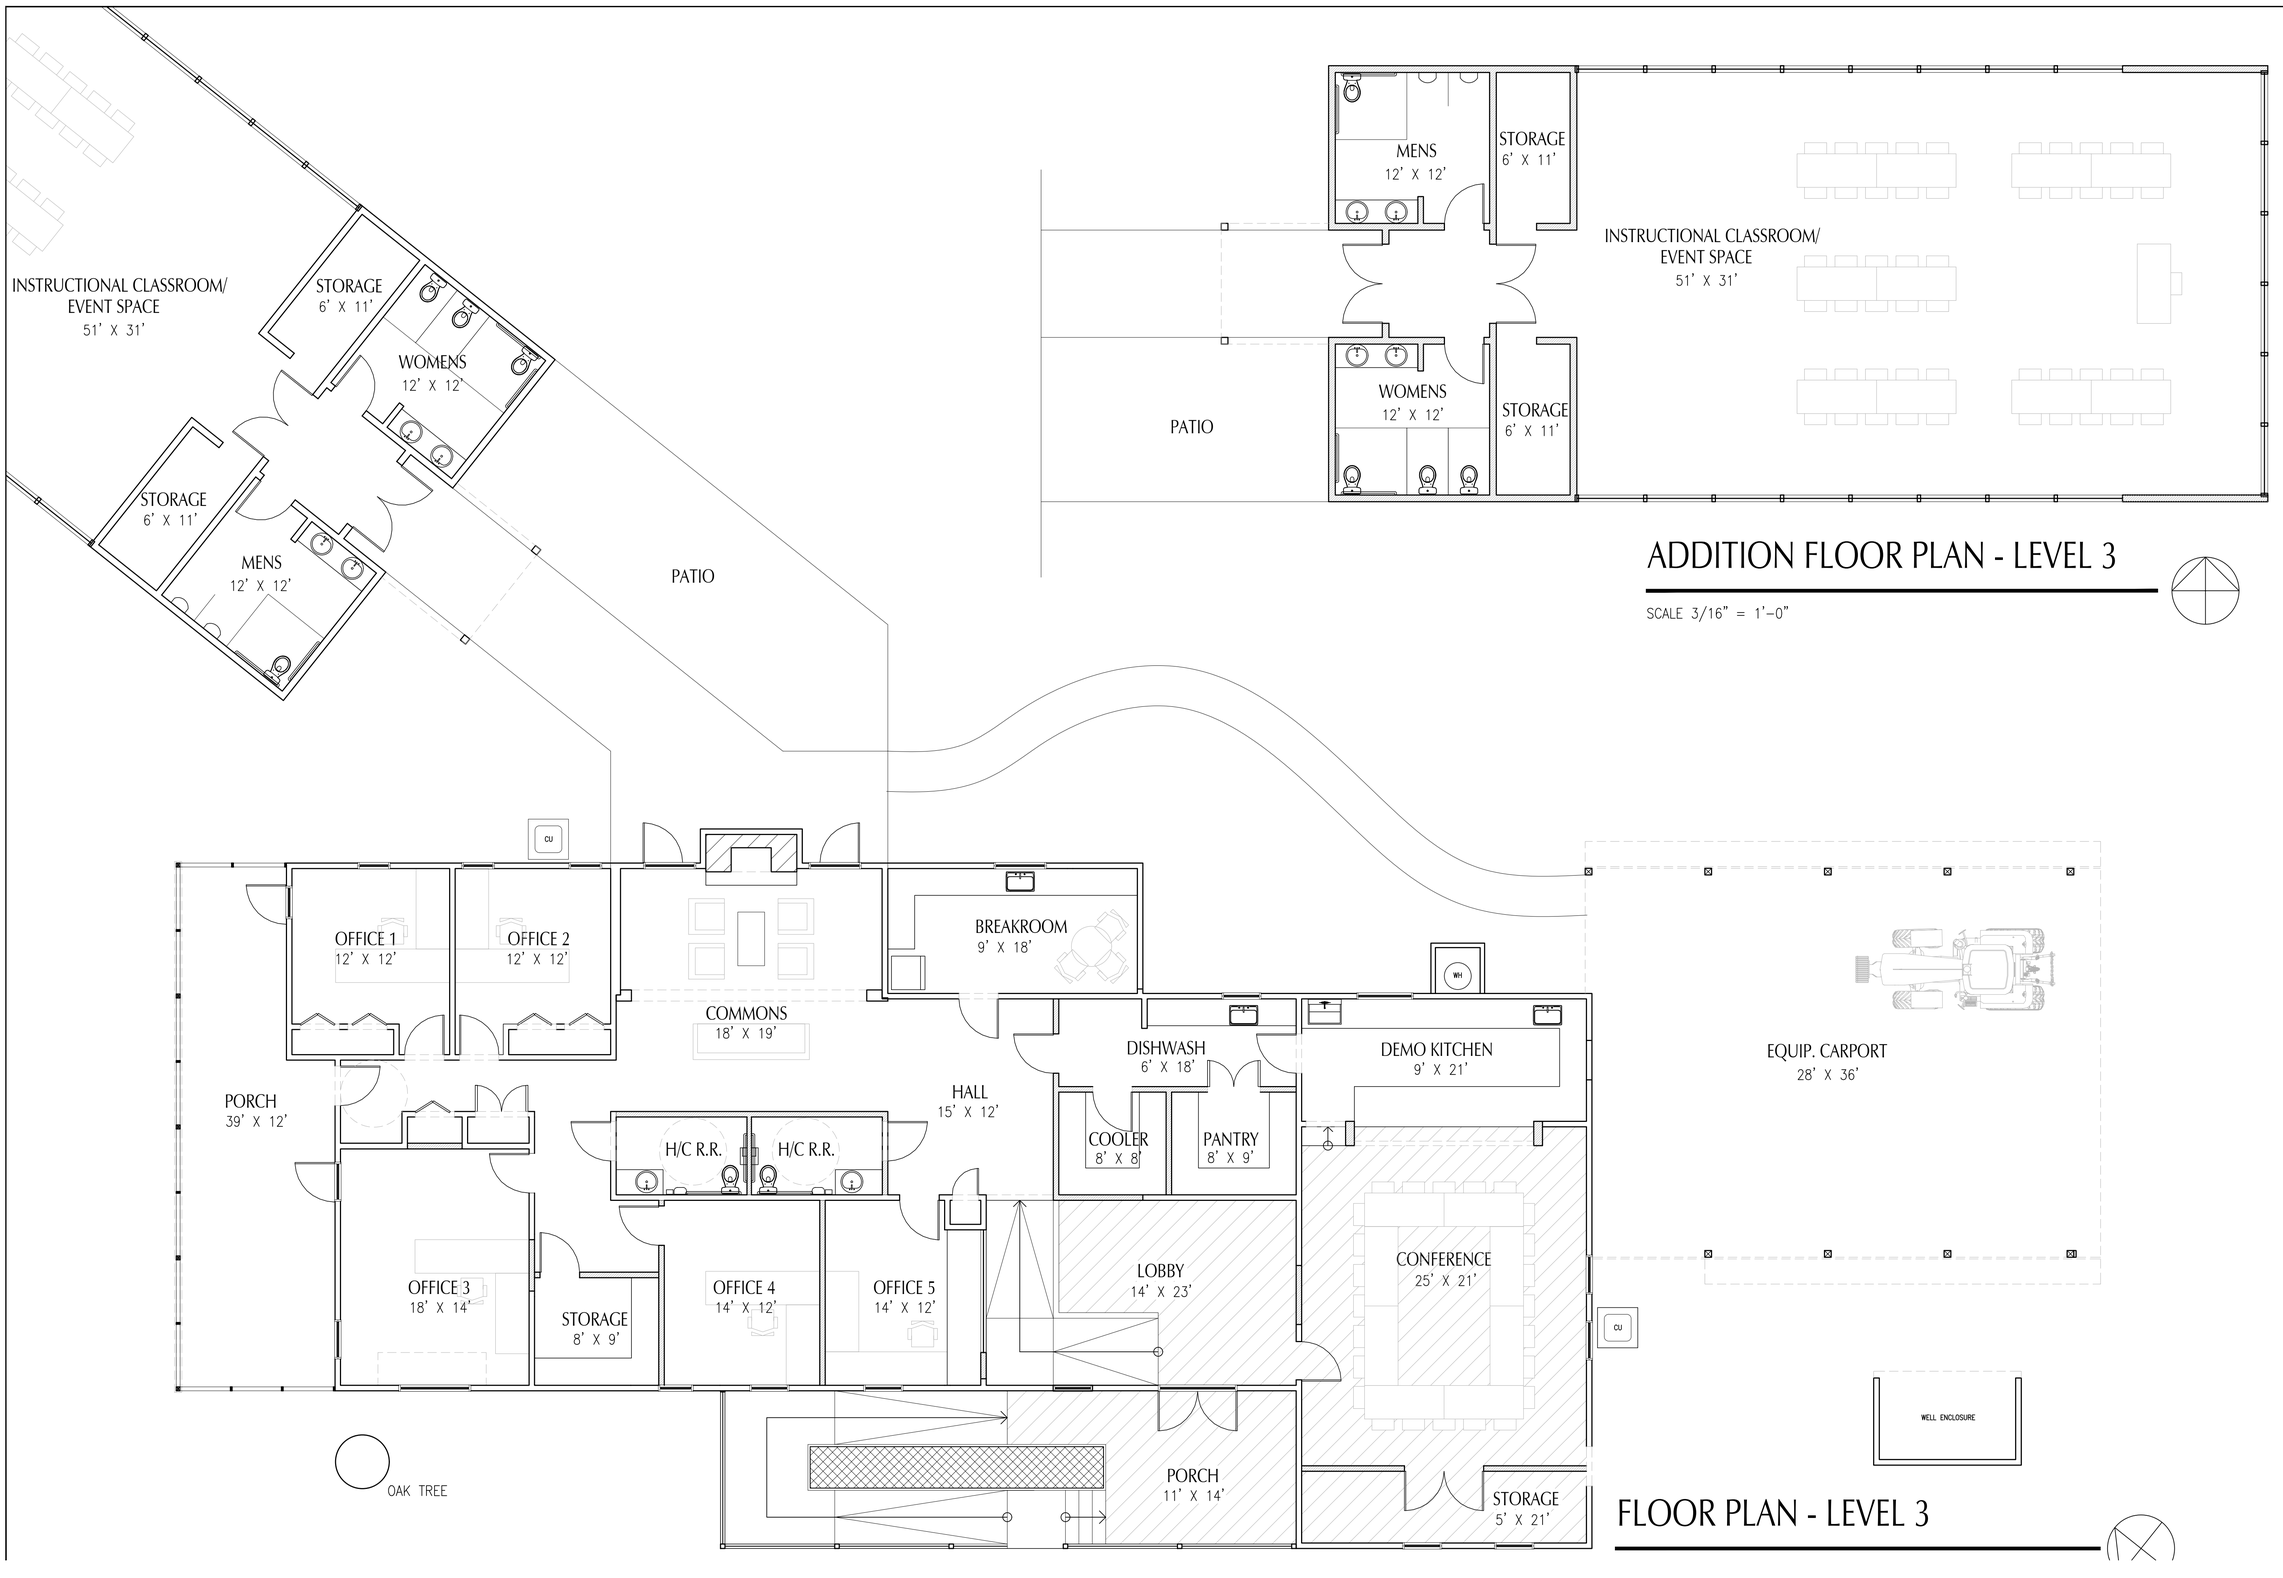

ADDITION FLOOR PLAN - LEVEL 3

SCALE 3/16" = 1'-0"

FLOOR PLAN - LEVEL 3

SeibertArchitects PA
1373 Fifth Street Sarasota Florida 34236
tel 941.366.9161 fax 941.365.0902 lic AA-C000070
www.seibertarchitects.com

RENOVATIONS TO THE
Red House

Architects, P.A. All Rights Reserved

Date:	SEPTEMBER 3, 2026
Project:	2601
Rev. 1:	
Rev. 2:	
Rev. 3:	
Rev. 4	