
MAP OF SPECIFIC PURPOSE SURVEY

LYING IN SECTION 22, & 27, TOWNSHIP 37 SOUTH, RANGE 19 EAST,
SARASOTA COUNTY, FLORIDA.

LEGEND

These standard symbols and abbreviations can be found herein.

- Benchmark, as denoted
- "X"/Cross Cut found
- Corner set, Nail & Disk, or 5/8" Iron Rod & Cap (LB7731).
- Corner found, as denoted.
- Monument set, 4" Concrete (LB7731)
- Monument found, as denoted
- Mail Box
- Bollard Post, as denoted
- Wood Sign Post
- Metal Sign Post
- Yard Drain
- Storm Grate Inlet
- Underdrain Cleanout
- Sanitary Sewer Cleanout
- Backflow preventer
- Water Meter
- Reuse Water Meter
- Irrigation Control Valve
- Well
- Septic Tank Lid
- Fire Hydrant
- Gate Valve, as denoted
- Sanitary Sewer Manhole
- Storm Sewer Manhole
- Electric Manhole
- Utility Manhole
- Unknown Manhole
- Wood Power Pole
- Concrete Power Pole
- Metal Power Pole
- Metal Light Pole
- Wood Light Pole
- Flood/Yard Light
- Metal Flag Pole
- Concrete Light Pole
- Guy Wire Anchor
- Cross-walk Signal Post
- Power Transformer pad
- Utility Pull Box
- Utility Hand Hole
- Utility Riser
- Utility Cabinet
- Bore Sample Location
- Gas Valve
- Gas line marker
- Palm Tree
- Oak Tree
- Pine Tree
- Citrus Tree
- Banyan Tree
- Unknown Tree
- Spot Elevation
- (R) Radial
- (NR) Non-Radial
- (D) Deed
- (P) Plat
- (F) Field
- (C) Calculated.
- CB Chord Bearing
- CH Chord Distance
- A Arc Distance
- D Delta
- L Line
- C Curve
- OA Overall
- N: Northing
- E: Easting
- STA Station
- OS Offset
- R Right Offset
- L Left Offset
- WIT Witness Corner
- POL Point on-line
- PCP Permanent Control Point
- PRM Permanent Reference Monument.
- PID Parcel Identification Number
- ORB Official Records Book.
- ORI Official Records Instrument
- PG Page.
- FB Field Book.
- PB Plat Book.
- DB Deed Book.
- CCR Certified Corner Record
- NGS National Geodetic Survey
- FDEP Dept. of Environmental Protection
- FDOT Dept. of Transportation
- FIRM Flood Insurance Rate Map
- BFE Base Flood Elevation
- NAD North American Datum
- NAVD North American Vertical Datum
- NGVD National Geodetic Vertical Datum
- LS Licensed Surveyor
- LB Licensed Business.
- PLS Professional Land Surveyor.
- RLS Registered Land Surveyor.
- PSM Professional Surveyor & Mapper
- MTS Minimum Technical Standards
- A/C Air Conditioner
- FF Finish Floor Elevation
- GF Garage Floor Elevation
- WIN Weir Invert
- INV Pipe Invert
- MES Mitered End Section
- EOP End of Pipe
- GAS Gas Main
- STM Storm Drain
- SAN Sanitary Main
- SFM Sanitary Force Main
- RUW Reuse Water Main
- IRR Irrigation Line
- W Water Main
- FS Fire Service
- FDC Fire Department Connection
- UGE Underground Electric
- UGT Underground Telephone
- UGTV Underground Television
- OE Overhead Electric
- UNK Unknown

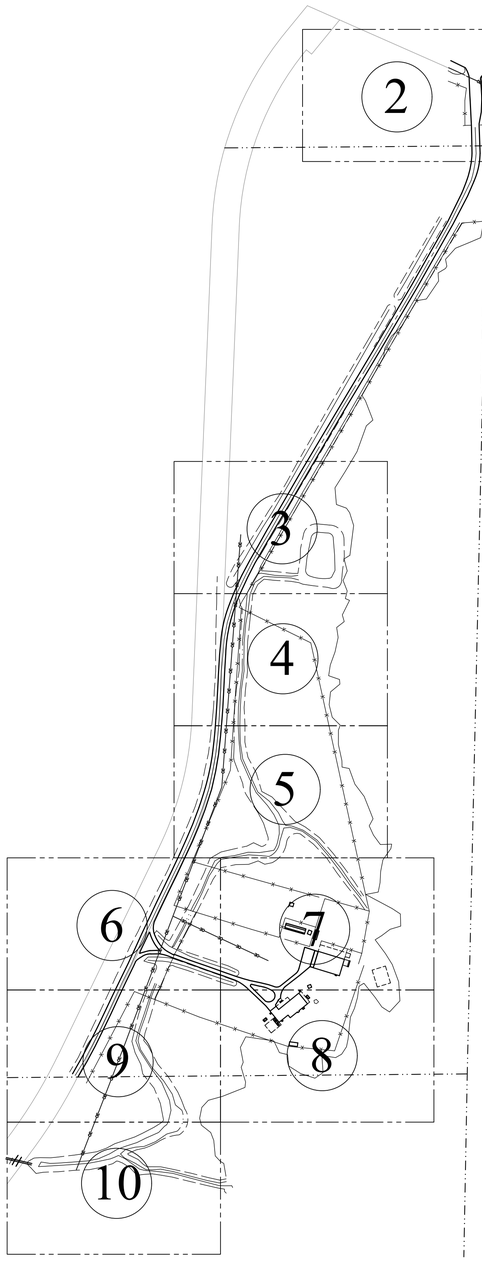

KEY MAP
Not to Scale

SURVEYOR'S REPORT

1. SURVEY TYPE: This map represents a Specific Purpose Survey. depicting visible, above ground, and permanently fixed improvements, above ground evidence for utilities, surface surface spot elevations only. Ownership of fences and/or any other improvements shown hereon has not been determined as a part of this survey.

2. BEARING BASIS: Bearings shown hereon are based on Grid, Florida State Plane Coordinate System, Zone West (FL-W), North American Datum of 1983 (NAD83), horizontal adjustment year 2011. Derived by redundant GPS RTK observation, using FDOT Virtual Real-time Network Solution.

3. UTILITIES/UNDERGROUND LOCATIONS: Underground improvements and/or utilities, those including, but not limited to; foundations, stem-walls, septic tanks, drainfields, wells, conduits, irrigation, and/or other utilities, which are not visible above ground and therefore have not been included as a part of this survey, unless as shown hereon. Those utilities shown herein have been identified while conducting the fieldwork only. No excavation was performed by the firm for the purpose of this survey. No other information regarding underground utility locations has been provided to, nor pursued by the undersigned for the purpose of this survey. Underground utility information is subject to field verification.

4. TITLE COMMITMENT: This map has been prepared without the benefit of a Commitment for Title Insurance, or Title Policy Opinion. The survey shown herein is subject to those exceptions, covenants, conditions and restrictions of record that a subsequent title search may disclose.

5. FLOOD ZONE: The parcel described herein appears situated in Flood Zone A, and X, per FIRM 12115C0235 G, Map Effective Date March 27, 2024. Information shown herein is subject to topographic verification and has been scaled from said map.

6. ZONING REGULATIONS & SETBACKS: Information regarding Zoning and/or Setbacks have not been provided to, nor pursued by the undersigned Professional Land Surveyor, and therefore have not been included as a part of this survey.

7. SURVEY LIMITATIONS: Specific Purpose Surveys by no means represent a determination on whether properties will or will not flood. The land within the boundaries of this Specific Purpose Survey may or may not be subject to flooding and or standing water.

8. SURVEY VALIDITY NOTICE: Not valid without the original signature and embossed seal of a Professional Land Surveyor. Reuse of this survey for any purpose other than intended, without written authorization of the undersigned Professional Land Surveyor, will be solely at the risk of the user without liability to the undersigned. Nothing herein shall be construed to give any rights or benefits to anyone other than those certified to.

9. SURVEY ACCURACY STANDARD: The survey shown hereon has a classified expected use of "SUBURBAN". The minimum relative distance error for this classification of survey is 1 foot in 7,500 feet. The accuracy obtained by measurement and calculation of a closed geometric figure was found to exceed this requirement.

10. All distances shown herein are U.S. Survey Feet.

11. RIGHT-OF-WAYS REFERENCE: Right-of-Way for STATE ROAD 72 (CLARK ROAD), shown hereon referenced by Sarasota County Road Plat 1, Page 52, Public Records of Sarasota County, Florida.

12. ELEVATION DATUM REFERENCE: Elevations shown hereon reference the North American Vertical Datum of 1988 (NAVD88). Reference to NGS Benchmark PID: DL2124, Designations J 702, with a published elevation of 22.65'(NAVD88).

13. JURISDICTIONAL LANDS: There may or may not exist other, if any, wetlands and/or environmentally protected lands over or across the parcel described herein, which have not been identified or delineated as a part of this survey.

SURVEYOR'S CERTIFICATE

I, the undersigned registered Professional Land Surveyor, do hereby certify that a survey was performed, under my direct supervision, on the parcel described herein and for the purpose stated herein, also that, in my professional opinion, said survey meets the Standards of Practice, as set forth by the Board of Professional Surveyors and Mappers, in Chapter 5J-17, FAC. Furthermore the map shown hereon is a true and correct representation of said survey to the best of my knowledge and belief.

August 6, 2026
Field Survey Date

Harold E. Noon, Jr.
Professional Surveyor and Mapper: LS 6568

MAP OF SPECIFIC PURPOSE SURVEY

CERTIFIED TO:
SARASOTA COUNTY
FISHER ENGINEERING, INC.
SEIBERT ARCHITECTS

SITUS ADDRESS:
STATE ROAD 72,
SARASOTA, FLORIDA 34241

DATE: 8/06/26 FB: -- PG: --
PROJECT NO. 260036
SEC. 22,27 TWP 37 S RGE 19 E
PARCEL ID: 0294-00-4000

FIELD BC
DRAWN DC
CHECK HN

	REVISION	DRAWN	DATE
1.			
2.			
3.			
4.			

L:\Geosurv Company\Company Work Drive\Projects\260036\260036_SPS.dwg

GEOSURV SURVEYING & MAPPING
www.geosurveygroup.com L.B. 7731
5707 19th Street W.
Bradenton, Florida 34207
Tel. 877.407.5734
Fax. 866.624.5163
info@geosurveygroup.com

NOT VALID UNLESS CONTAINING ALL SHEETS

MAP OF SPECIFIC PURPOSE SURVEY


LYING IN SECTION 22, & 27, TOWNSHIP 37 SOUTH, RANGE 19 EAST,
SARASOTA COUNTY, FLORIDA.


LEGEND

These standard symbols and abbreviations can be found herein.

- Benchmark, as denoted
- "X"/Cross Cut found
- Corner set, Nail & Disk, or 5/8" Iron Rod & Cap (LB7731).
- Corner found, as denoted.
- Monument set, 4" Concrete (LB7731)
- Monument found, as denoted
- Mail Box
- Bollard Post, as denoted
- Wood Sign Post
- Metal Sign Post
- Yard Drain
- Storm Grate Inlet
- Underdrain Cleanout
- Sanitary Sewer Cleanout
- Backflow preventer
- Water Meter
- Reuse Water Meter
- Irrigation Control Valve
- Well
- Septic Tank Lid
- Fire Hydrant
- Gate Valve, as denoted
- Sanitary Sewer Manhole
- Storm Sewer Manhole
- Electric Manhole
- Utility Manhole
- Unknown Manhole
- Wood Power Pole
- Concrete Power Pole
- Metal Power Pole
- Metal Light Pole
- Wood Light Pole
- Flood/Yard Light
- Metal Flag Pole
- Concrete Light Pole
- Guy Wire Anchor
- Cross-walk Signal Post
- Power Transformer pad
- Utility Pull Box
- Utility Hand Hole
- Utility Riser
- Utility Cabinet
- Bore Sample Location
- Gas Valve
- Gas line marker
- Palm Tree
- Oak Tree
- Pine Tree
- Citrus Tree
- Banyan Tree
- Unknown Tree
- Spot Elevation

(R) Radial
(NR) Non-Radial
(D) Deed
(P) Plat
(F) Field
(C) Calculated.
CB Chord Bearing
CH Chord Distance
A Arc Distance
D Delta
L Line
C Curve
OA Overall
N: Northing
E: Easting
STA Station
OS Offset
R Right Offset
L Left Offset
WT Witness Corner
POL Point on-line
PCP Permanent Control Point
PRM Permanent Reference Monument.
PID Parcel Identification Number
ORB Official Records Book.
ORI Official Records Instrument
PG Page.
FB Field Book.
PB Plat Book.
DB Deed Book.
CCR Certified Corner Record
NGS National Geodetic Survey
FDEP Dept. of Environmental Protection
FDOT Dept. of Transportation
FIRM Flood Insurance Rate Map
BFE Base Flood Elevation
NAD North American Datum
NAVD North American Vertical Datum
NGVD National Geodetic Vertical Datum
LS Licensed Surveyor
LB Licensed Business.
PLS Professional Land Surveyor.
RLS Registered Land Surveyor.
PSM Professional Surveyor & Mapper
MTS Minimum Technical Standards
A/C Air Conditioner
FF Finish Floor Elevation
GF Garage Floor Elevation
WIN Weir Invert
INV Pipe Invert
MES Mitered End Section
EOP End of Pipe
GAS Gas Main
STM Storm Drain
SAN Sanitary Main
SFM Sanitary Force Main
RUW Reuse Water Main
IRR Irrigation Line
W Water Main
FS Fire Service
FDC Fire Department Connection
UGE Underground Electric
UGT Underground Telephone
UGTV Underground Television
OE Overhead Electric
UNK Unknown

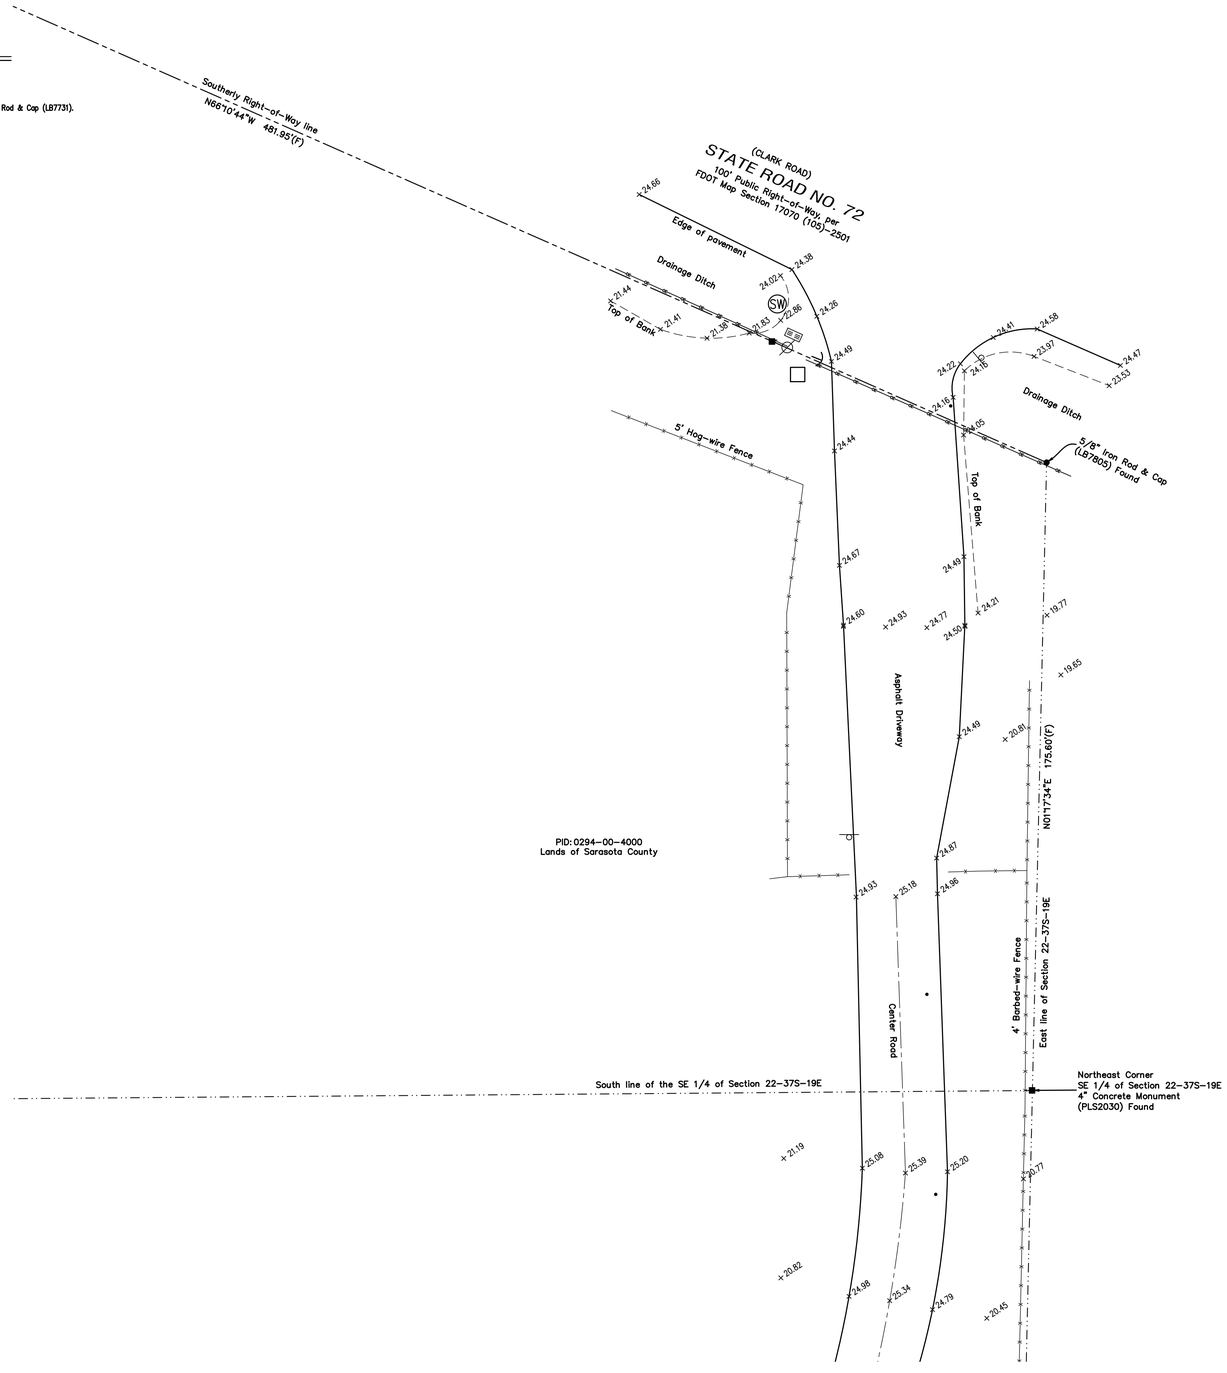

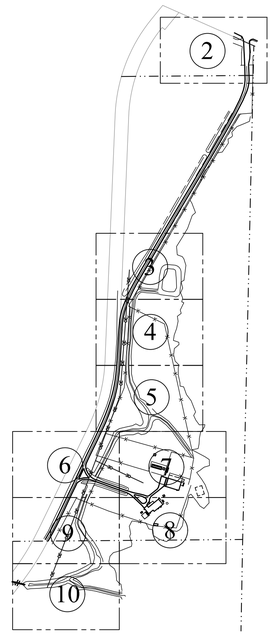

KEY MAP
Not to Scale

0' 20' 40'
GRAPHIC SCALE 1" = 20' (US Survey Feet)

© COPYRIGHT Geosurv, LLC, 2026. All Rights Reserved.

	REVISION	DRAWN	DATE
1.			
2.			
3.			
4.			

L:\Geosurv Company\Company Work Drive\Projects\260036\260036_SPS.dwg

NOT VALID UNLESS CONTAINING ALL SHEETS

GEOSURV SURVEYING & MAPPING
www.geosurveygroup.com L.B. 7731
5707 19th Street W.
Bradenton, Florida 34207
Tel. 877.407.3734
Fax 866.624.5163
info@geosurveygroup.com

MAP OF SPECIFIC PURPOSE SURVEY

LYING IN SECTION 22, & 27, TOWNSHIP 37 SOUTH, RANGE 19 EAST,
SARASOTA COUNTY, FLORIDA.

LEGEND

These standard symbols and abbreviations can be found herein.

- Benchmark, as denoted
- "X"/Cross Cut found
- Corner set, Nail & Disk, or 5/8" Iron Rod & Cap (LB7731).
- Corner found, as denoted.
- Monument set, 4" Concrete (LB7731)
- Monument found, as denoted
- Mail Box
- Bollard Post, as denoted
- Wood Sign Post
- Metal Sign Post
- Yard Drain
- Storm Grate Inlet
- Underdrain Cleanout
- Sanitary Sewer Cleanout
- Backflow preventer
- Water Meter
- Reuse Water Meter
- Irrigation Control Valve
- Well
- Septic Tank Lid
- Fire Hydrant
- Gate Valve, as denoted
- Sanitary Sewer Manhole
- Storm Sewer Manhole
- Electric Manhole
- Utility Manhole
- Unknown Manhole
- Wood Power Pole
- Concrete Power Pole
- Metal Power Pole
- Metal Light Pole
- Wood Light Pole
- Flood/Yard Light
- Metal Flag Pole
- Concrete Light Pole
- Guy Wire Anchor
- Cross-walk Signal Post
- Power Transformer pad
- Utility Pull Box
- Utility Hand Hole
- Utility Riser
- Utility Cabinet
- Bore Sample Location
- Gas Valve
- Gas line marker
- Palm Tree
- Oak Tree
- Pine Tree
- Citrus Tree
- Banyan Tree
- Unknown Tree
- Spot Elevation
- (R) Radial
- (NR) Non-Radial
- (D) Deed
- (P) Plat
- (F) Field
- (C) Calculated.
- CB Chord Bearing
- CH Chord Distance
- A Arc Distance
- D Delta
- L Line
- C Curve
- OA Overall
- N: Northing
- E: Easting
- STA Station
- OS Offset
- R Right Offset
- L Left Offset
- WT Witness Corner
- POL Point on-line
- PCP Permanent Control Point
- PRM Permanent Reference Monument.
- PID Parcel Identification Number
- ORB Official Records Book.
- ORI Official Records Instrument
- PG Page.
- FB Field Book.
- PB Plat Book.
- DB Deed Book.
- CCR Certified Corner Record
- NGS National Geodetic Survey
- FDEP Dept. of Environmental Protection
- FDOT Dept. of Transportation
- FIRM Flood Insurance Rate Map
- BFE Base Flood Elevation
- NAD North American Datum
- NAVD North American Vertical Datum
- NGVD National Geodetic Vertical Datum
- LS Licensed Surveyor
- LB Licensed Business.
- PLS Professional Land Surveyor.
- RLS Registered Land Surveyor.
- PSM Professional Surveyor & Mapper
- MTS Minimum Technical Standards
- A/C Air Conditioner
- FF Finish Floor Elevation
- GF Garage Floor Elevation
- MIN Weir Invert
- INV Pipe Invert
- MES Mitered End Section
- EOP End of Pipe
- GAS Gas Main
- STM Storm Drain
- SAN Sanitary Main
- SFM Sanitary Force Main
- RUW Reuse Water Main
- IRR Irrigation Line
- W Water Main
- FS Fire Service
- FDC Fire Department Connection
- UGE Underground Electric
- UGT Underground Telephone
- UGTV Underground Television
- OE Overhead Electric
- UNK Unknown

PID:0294-00-4000
Lands of Sarasota County

(SURVEY THIS AREA, NOT INCLUDED)

Centerline Canal Easement, per ORB 527/PG 36

COWPEN SLOUGH
160' wide Canal Easement, per ORB 527/PG 36

East line of Easement
S0°22'10"W 1,450.99'(F)

80.0'

GEOBM-01
NGS "J702" Iron Rod Found
22.65'(NAVD88)

Top of Bank
Center Swale
Edge of Pavement
±19' Asphalt Road
Center Road
Edge of Pavement
Top of Bank
Center Swale
4' Barbed-wire Fence
Top of Bank
Tree/Vegetation Line
Heavily Wooded Area
Top of Bank
Toe of Slope
Toe of Slope
Top of Bank
4' Barbed-wire Fence
Edge of Water
Existing Retention Pond
Edge of Water Elevation ±14.3'
located in field on 7/20/26
Approximate Flood Zone Line, scaled from FIRM
ZONE A
ZONE X

KEY MAP
Not to Scale

MATCH LINE SHEET 4

0' 20' 40'
GRAPHIC SCALE 1" = 20' (US Survey Feet)

© COPYRIGHT Geosurv, LLC, 2026. All Rights Reserved.

NOT VALID UNLESS CONTAINING ALL SHEETS

	REVISION	DRAWN	DATE
1.			
2.			
3.			
4.			


L:\Geosurv Company\Company Work Drive\Projects\260036\260036_SPS.dwg

GEOSURV SURVEYING & MAPPING
www.geosurveygroup.com L.B. 7731
5707 19th Street W.
Bradenton, Florida 34207
Tel. 877.407.3734
Fax 866.624.5163
info@geosurveygroup.com

MAP OF SPECIFIC PURPOSE SURVEY

LYING IN SECTION 22, & 27, TOWNSHIP 37 SOUTH, RANGE 19 EAST,
SARASOTA COUNTY, FLORIDA.

MATCH LINE SHEET 3

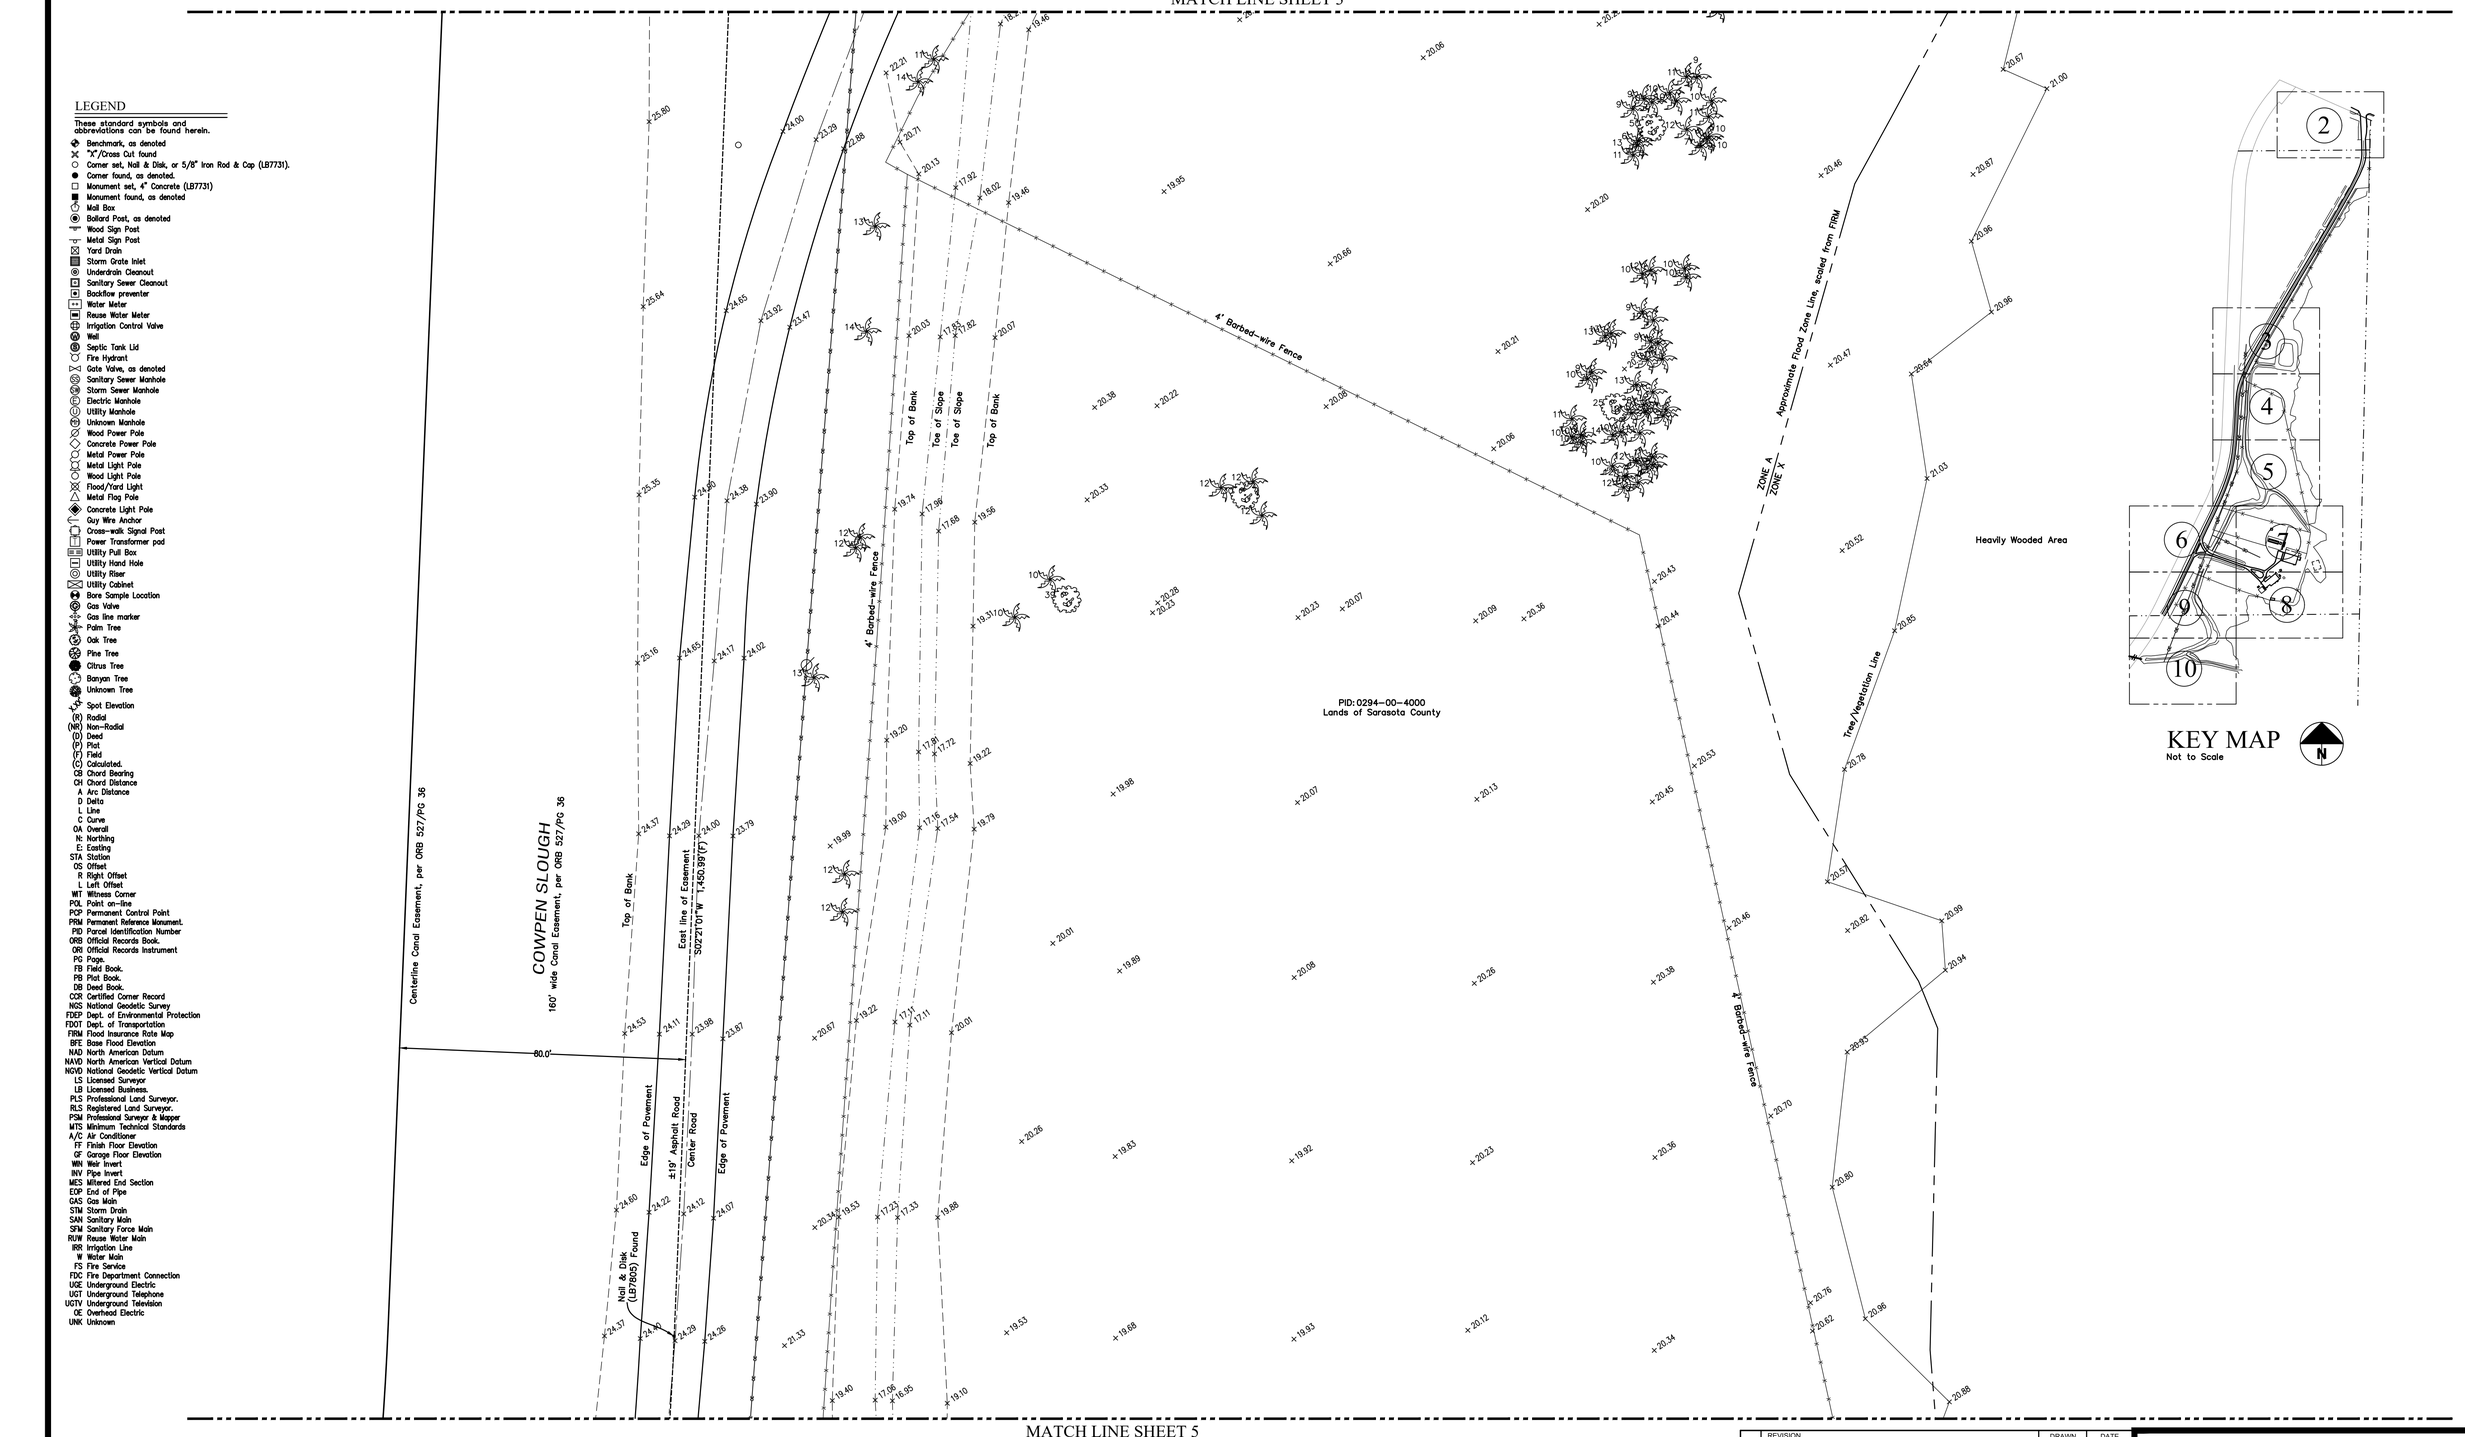

KEY MAP
Not to Scale

MATCH LINE SHEET 5

LEGEND

These standard symbols and abbreviations can be found herein.

- Benchmark, as denoted
- "X"/Cross Cut found
- Corner set, Nail & Disk, or 5/8" Iron Rod & Cap (LB7731).
- Corner found, as denoted.
- Monument set, 4" Concrete (LB7731)
- Monument found, as denoted
- Mail Box
- Bollard Post, as denoted
- Wood Sign Post
- Metal Sign Post
- Yard Drain
- Storm Grate Inlet
- Underdrain Cleanout
- Sanitary Sewer Cleanout
- Backflow preventer
- Water Meter
- Reuse Water Meter
- Irrigation Control Valve
- Well
- Septic Tank Lid
- Fire Hydrant
- Gate Valve, as denoted
- Sanitary Sewer Manhole
- Storm Sewer Manhole
- Electric Manhole
- Utility Manhole
- Unknown Manhole
- Wood Power Pole
- Concrete Power Pole
- Metal Power Pole
- Metal Light Pole
- Wood Light Pole
- Flood/Yard Light
- Metal Flag Pole
- Concrete Light Pole
- Guy Wire Anchor
- Cross-walk Signal Post
- Power Transformer pad
- Utility Pull Box
- Utility Hand Hole
- Utility Riser
- Utility Cabinet
- Bore Sample Location
- Gas Valve
- Gas line marker
- Palm Tree
- Oak Tree
- Pine Tree
- Citrus Tree
- Banyan Tree
- Unknown Tree
- Spot Elevation

(R) Radial
(NR) Non-Radial
(D) Deed
(P) Plat
(F) Field
(C) Calculated.
CB Chord Bearing
CH Chord Distance
A Arc Distance
D Delta
L Line
C Curve
OA Overall
N: Northing
E: Easting
STA Station
OS Offset
R Right Offset
L Left Offset
WT Witness Corner
POL Point on-line
PCP Permanent Control Point
PRM Permanent Reference Monument.
PID Parcel Identification Number
ORB Official Records Book.
ORI Official Records Instrument
PG Page.
FB Field Book.
PB Plat Book.
DB Deed Book.
CCR Certified Corner Record
NGS National Geodetic Survey
FDEP Dept. of Environmental Protection
FDOT Dept. of Transportation
FIRM Flood Insurance Rate Map
BFE Base Flood Elevation
NAD North American Datum
NAVD North American Vertical Datum
NGVD National Geodetic Vertical Datum
LS Licensed Surveyor
LB Licensed Business.
PLS Professional Land Surveyor.
RLS Registered Land Surveyor.
PSM Professional Surveyor & Mapper
MTS Minimum Technical Standards
A/C Air Conditioner
FF Finish Floor Elevation
GF Garage Floor Elevation
WIN Weir Invert
INV Pipe Invert
MES Mitered End Section
EOP End of Pipe
GAS Gas Main
STM Storm Drain
SAN Sanitary Main
SFM Sanitary Force Main
RUW Reuse Water Main
IRR Irrigation Line
W Water Main
FS Fire Service
FDC Fire Department Connection
UGE Underground Electric
UGT Underground Telephone
UGTV Underground Television
OE Overhead Electric
UNK Unknown

0' 20' 40'
GRAPHIC SCALE 1" = 20' (US Survey Feet)

© COPYRIGHT Geosurv, LLC, 2026. All Rights Reserved.

NOT VALID UNLESS CONTAINING ALL SHEETS

	REVISION	DRAWN	DATE
1.			
2.			
3.			
4.			


L:\Geosurv Company\Company Work Drive\Projects\260036\260036_SPS.dwg

GEOSURV SURVEYING & MAPPING
5707 19th Street W.
Bradenton, Florida 34207
Tel. 877.407.3734
Fax 866.624.5163
www.geosurveygroup.com L.B. 7731 info@geosurveygroup.com

MAP OF SPECIFIC PURPOSE SURVEY

LYING IN SECTION 22, & 27, TOWNSHIP 37 SOUTH, RANGE 19 EAST,
SARASOTA COUNTY, FLORIDA.

MATCH LINE SHEET 4

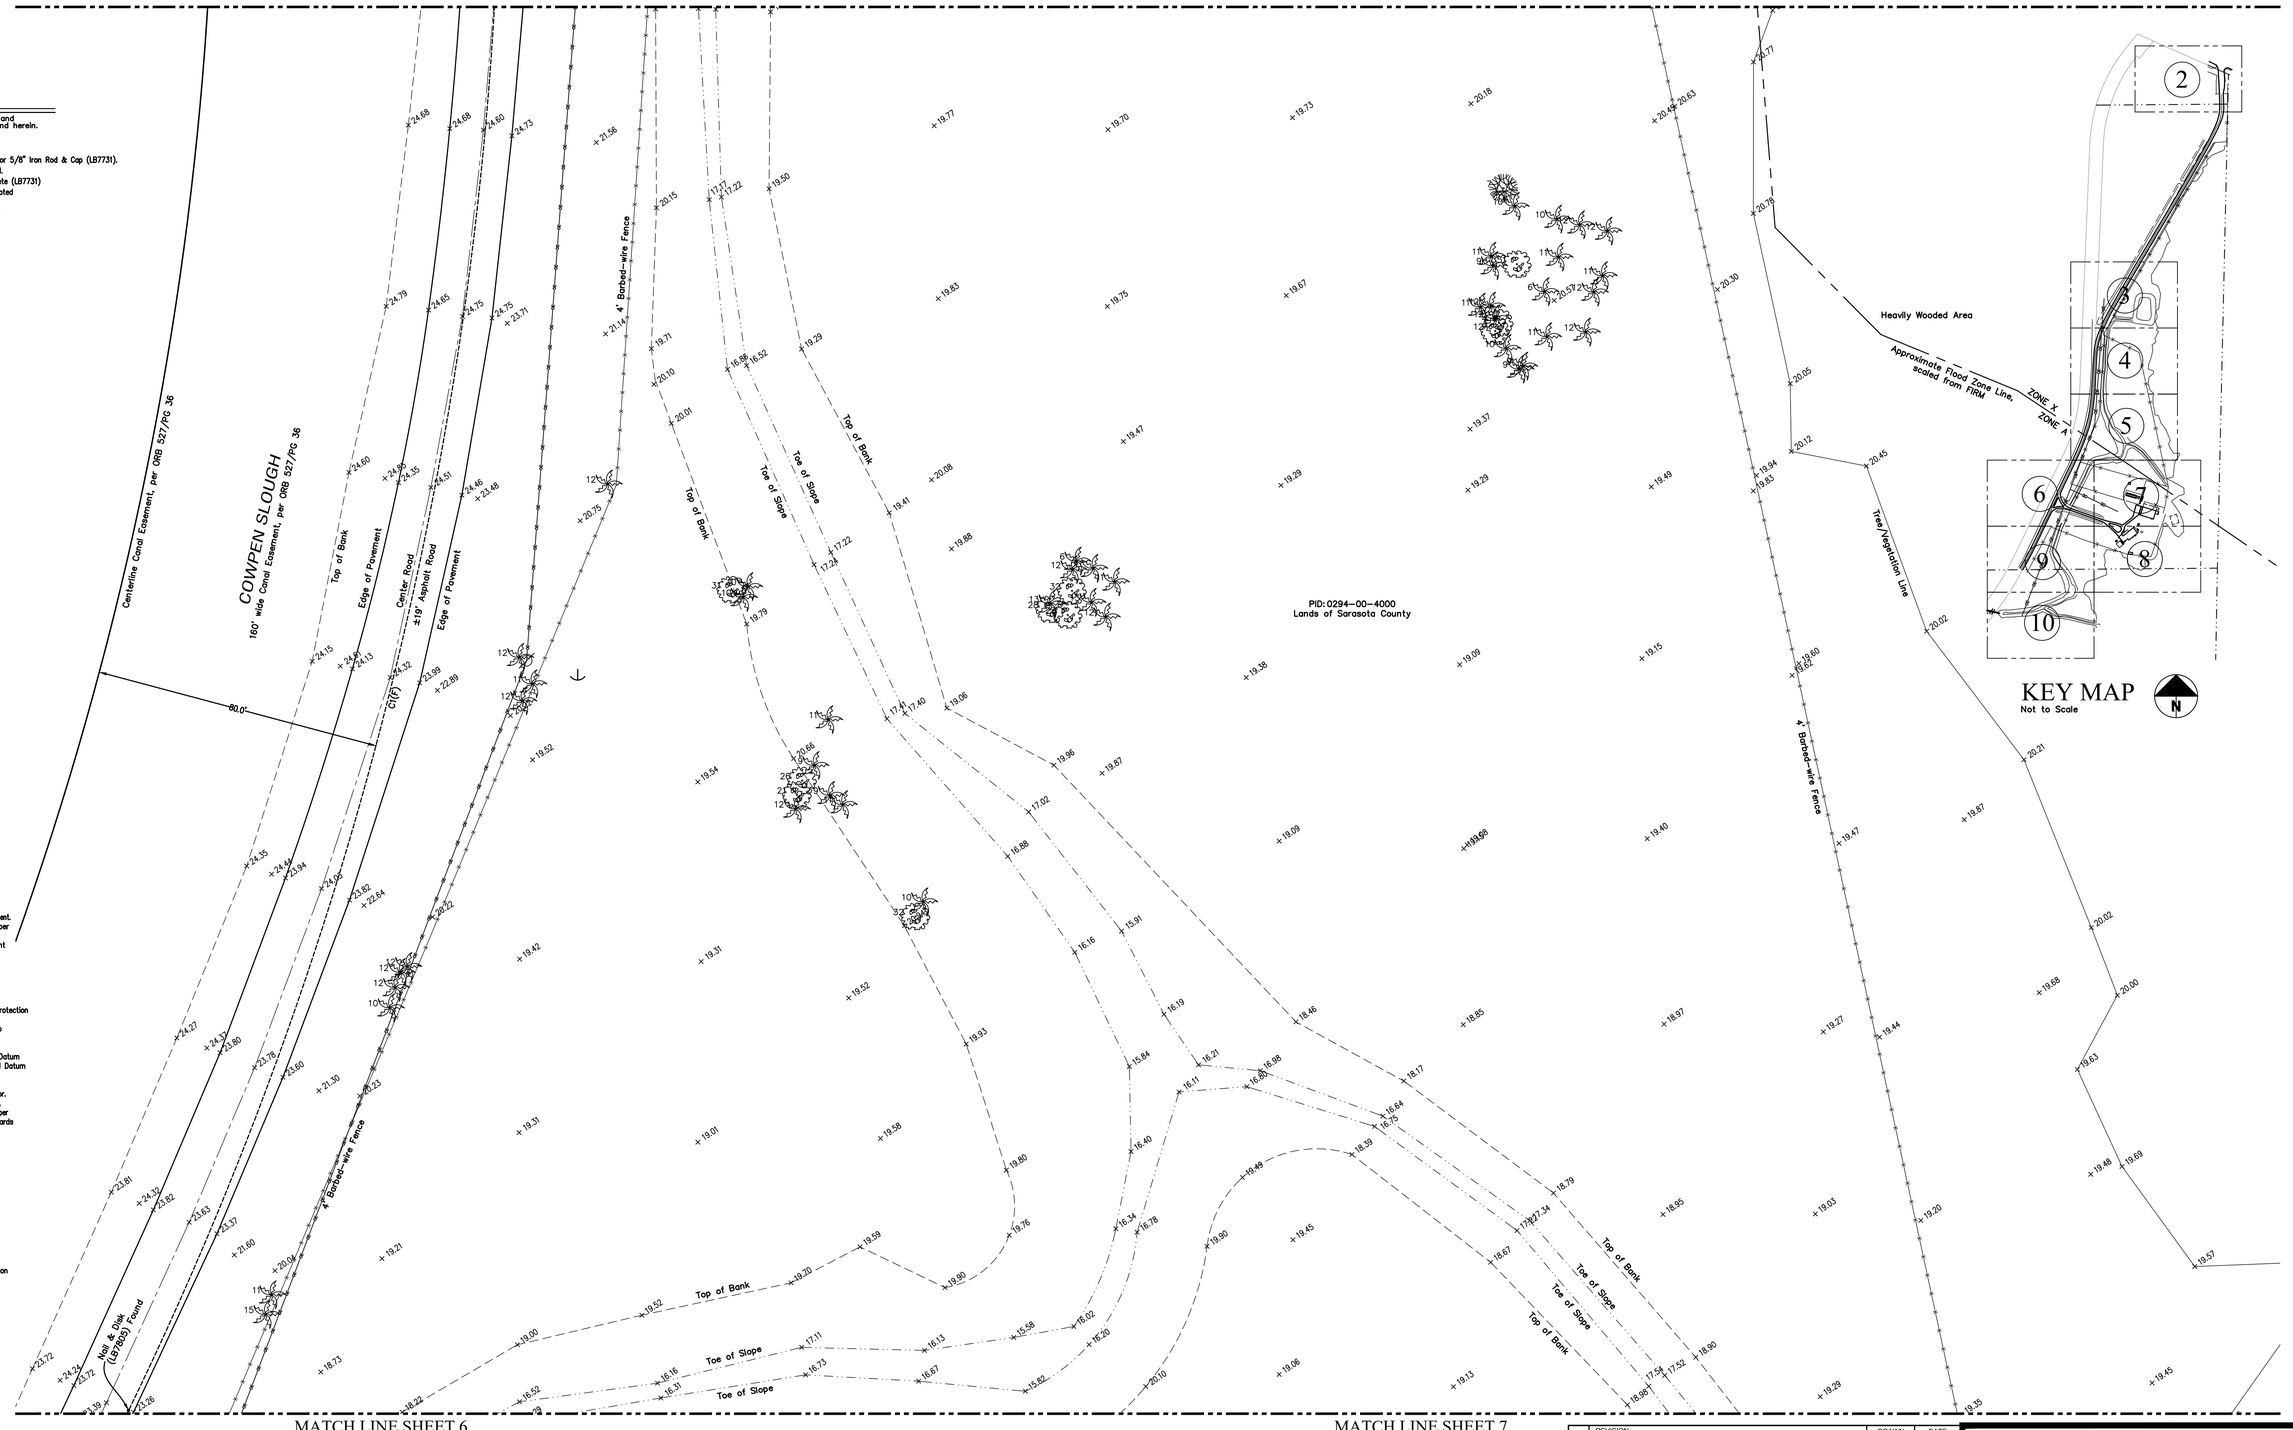

KEY MAP

Not to Scale

LEGEND

These standard symbols and abbreviations can be found herein.

- Benchmark, as denoted
- "X"/Cross Cut found
- Corner set, Nail & Disk, or 5/8" Iron Rod & Cap (LB7731).
- Corner found, as denoted.
- Monument set, 4" Concrete (LB7731)
- Monument found, as denoted
- Mail Box
- Bollard Post, as denoted
- Wood Sign Post
- Metal Sign Post
- Yard Drain
- Storm Grate Inlet
- Underdrain Cleanout
- Sanitary Sewer Cleanout
- Backflow preventer
- Water Meter
- Reuse Water Meter
- Irrigation Control Valve
- Well
- Septic Tank Lid
- Fire Hydrant
- Gate Valve, as denoted
- Sanitary Sewer Manhole
- Storm Sewer Manhole
- Electric Manhole
- Utility Manhole
- Unknown Manhole
- Wood Power Pole
- Concrete Power Pole
- Metal Power Pole
- Metal Light Pole
- Wood Light Pole
- Flood/Yard Light
- Metal Flag Pole
- Concrete Light Pole
- Guy Wire Anchor
- Cross-walk Signal Post
- Power Transformer pad
- Utility Pull Box
- Utility Hand Hole
- Utility Riser
- Utility Cabinet
- Bore Sample Location
- Gas Valve
- Gas line marker
- Palm Tree
- Oak Tree
- Pine Tree
- Citrus Tree
- Banyan Tree
- Unknown Tree
- Spot Elevation

(R) Radial
(NR) Non-Radial
(D) Deed
(P) Plat
(F) Field
(C) Calculated.
CB Chord Bearing
CH Chord Distance
A Arc Distance
D Delta
L Line
C Curve
OA Overall
N: Northing
E: Easting
STA Station
OS Offset
R Right Offset
L Left Offset
WT Witness Corner
POL Point on-line
PCP Permanent Control Point
PRM Permanent Reference Monument.
PID Parcel Identification Number
ORB Official Records Book.
OR Official Records Instrument
PG Page.
FB Field Book.
PB Plat Book.
DB Deed Book.
CCR Certified Corner Record
NGS National Geodetic Survey
FDEP Dept. of Environmental Protection
FDOT Dept. of Transportation
FIRM Flood Insurance Rate Map
BFE Base Flood Elevation
NAD North American Datum
NAVD North American Vertical Datum
NGVD National Geodetic Vertical Datum
LS Licensed Surveyor
LB Licensed Business.
PLS Professional Land Surveyor.
RLS Registered Land Surveyor.
PSM Professional Surveyor & Mapper
MTS Minimum Technical Standards
A/C Air Conditioner
FF Finish Floor Elevation
GF Garage Floor Elevation
WW Weir Invert
INV Pipe Invert
MES Mitered End Section
EOP End of Pipe
GAS Gas Main
STM Storm Drain
SAN Sanitary Main
SFM Sanitary Force Main
RUW Reuse Water Main
IRR Irrigation Line
W Water Main
FS Fire Service
FDC Fire Department Connection
UGE Underground Electric
UGT Underground Telephone
UGTV Underground Television
OE Overhead Electric
UNK Unknown

MATCH LINE SHEET 6

MATCH LINE SHEET 7

0' 20' 40'

GRAPHIC SCALE 1" = 20' (US Survey Feet)

© COPYRIGHT Geosurv, LLC, 2026. All Rights Reserved.

NOT VALID UNLESS CONTAINING ALL SHEETS

	REVISION	DRAWN	DATE
1.			
2.			
3.			
4.			

L:\Geosurv Company\Company Work Drive\Projects\260036\260036_SPS.dwg

GEOSURV SURVEYING & MAPPING
5707 19th Street W.
Bradenton, Florida 34207
Tel. 877.407.3734
Fax 866.624.5163
www.geosurveygroup.com L.B. 7731 info@geosurveygroup.com

MAP OF SPECIFIC PURPOSE SURVEY

LYING IN SECTION 22, & 27, TOWNSHIP 37 SOUTH, RANGE 19 EAST,
SARASOTA COUNTY, FLORIDA.


MATCH LINE SHEET 5

LEGEND


These standard symbols and abbreviations can be found herein.

- Benchmark, as denoted
- "X"/Cross Cut found
- Corner set, Nail & Disk, or 5/8" Iron Rod & Cap (LB7731).
- Corner found, as denoted.
- Monument set, 4" Concrete (LB7731)
- Monument found, as denoted
- Mail Box
- Bollard Post, as denoted
- Wood Sign Post
- Metal Sign Post
- Yard Drain
- Storm Grate Inlet
- Underdrain Cleanout
- Sanitary Sewer Cleanout
- Backflow preventer
- Water Meter
- Reuse Water Meter
- Irrigation Control Valve
- Well
- Septic Tank Lid
- Fire Hydrant
- Gate Valve, as denoted
- Sanitary Sewer Manhole
- Storm Sewer Manhole
- Electric Manhole
- Utility Manhole
- Unknown Manhole
- Wood Power Pole
- Concrete Power Pole
- Metal Power Pole
- Metal Light Pole
- Wood Light Pole
- Flood/Yard Light
- Metal Flag Pole
- Concrete Light Pole
- Guy Wire Anchor
- Cross-walk Signal Post
- Power Transformer pad
- Utility Pull Box
- Utility Hand Hole
- Utility Riser
- Utility Cabinet
- Bore Sample Location
- Gas Valve
- Gas line marker
- Palm Tree
- Oak Tree
- Pine Tree
- Citrus Tree
- Banyan Tree
- Unknown Tree
- Spot Elevation

(R) Radial
(NR) Non-Radial
(D) Deed
(P) Plat
(F) Field
(C) Calculated.
CB Chord Bearing
CH Chord Distance
A Arc Distance
D Delta
L Line
C Curve
OA Overall
N: Northing
E: Easting
STA Station
OS Offset
R Right Offset
L Left Offset
WT Witness Corner
POL Point on-line
PCP Permanent Control Point
PRM Permanent Reference Monument.
PID Parcel Identification Number
ORB Official Records Book.
ORI Official Records Instrument
PG Page.
FB Field Book.
PB Plat Book.
DB Deed Book.
CCR Certified Corner Record
NGS National Geodetic Survey
FDEP Dept. of Environmental Protection
FDOT Dept. of Transportation
FIRM Flood Insurance Rate Map
BFE Base Flood Elevation
NAD North American Datum
NAVD North American Vertical Datum
NGVD National Geodetic Vertical Datum
LS Licensed Surveyor
LB Licensed Business.
PLS Professional Land Surveyor.
RLS Registered Land Surveyor.
PSM Professional Surveyor & Mapper
MTS Minimum Technical Standards
A/C Air Conditioner
FF Finish Floor Elevation
GF Garage Floor Elevation
WIN Weir Invert
INV Pipe Invert
MES Mitered End Section
EOP End of Pipe
GAS Gas Main
STM Storm Drain
SAN Sanitary Main
SFM Sanitary Force Main
RUW Reuse Water Main
IRR Irrigation Line
W Water Main
FS Fire Service
FDC Fire Department Connection
UGE Underground Electric
UGT Underground Telephone
UGTV Underground Television
OE Overhead Electric
UNK Unknown

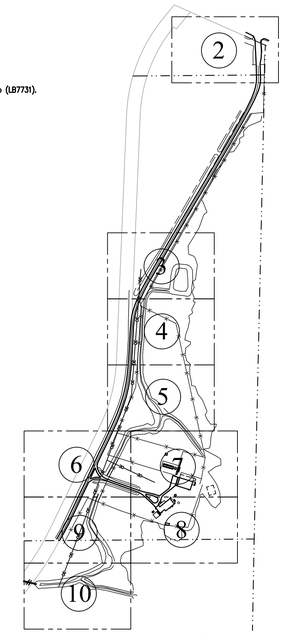

KEY MAP
Not to Scale

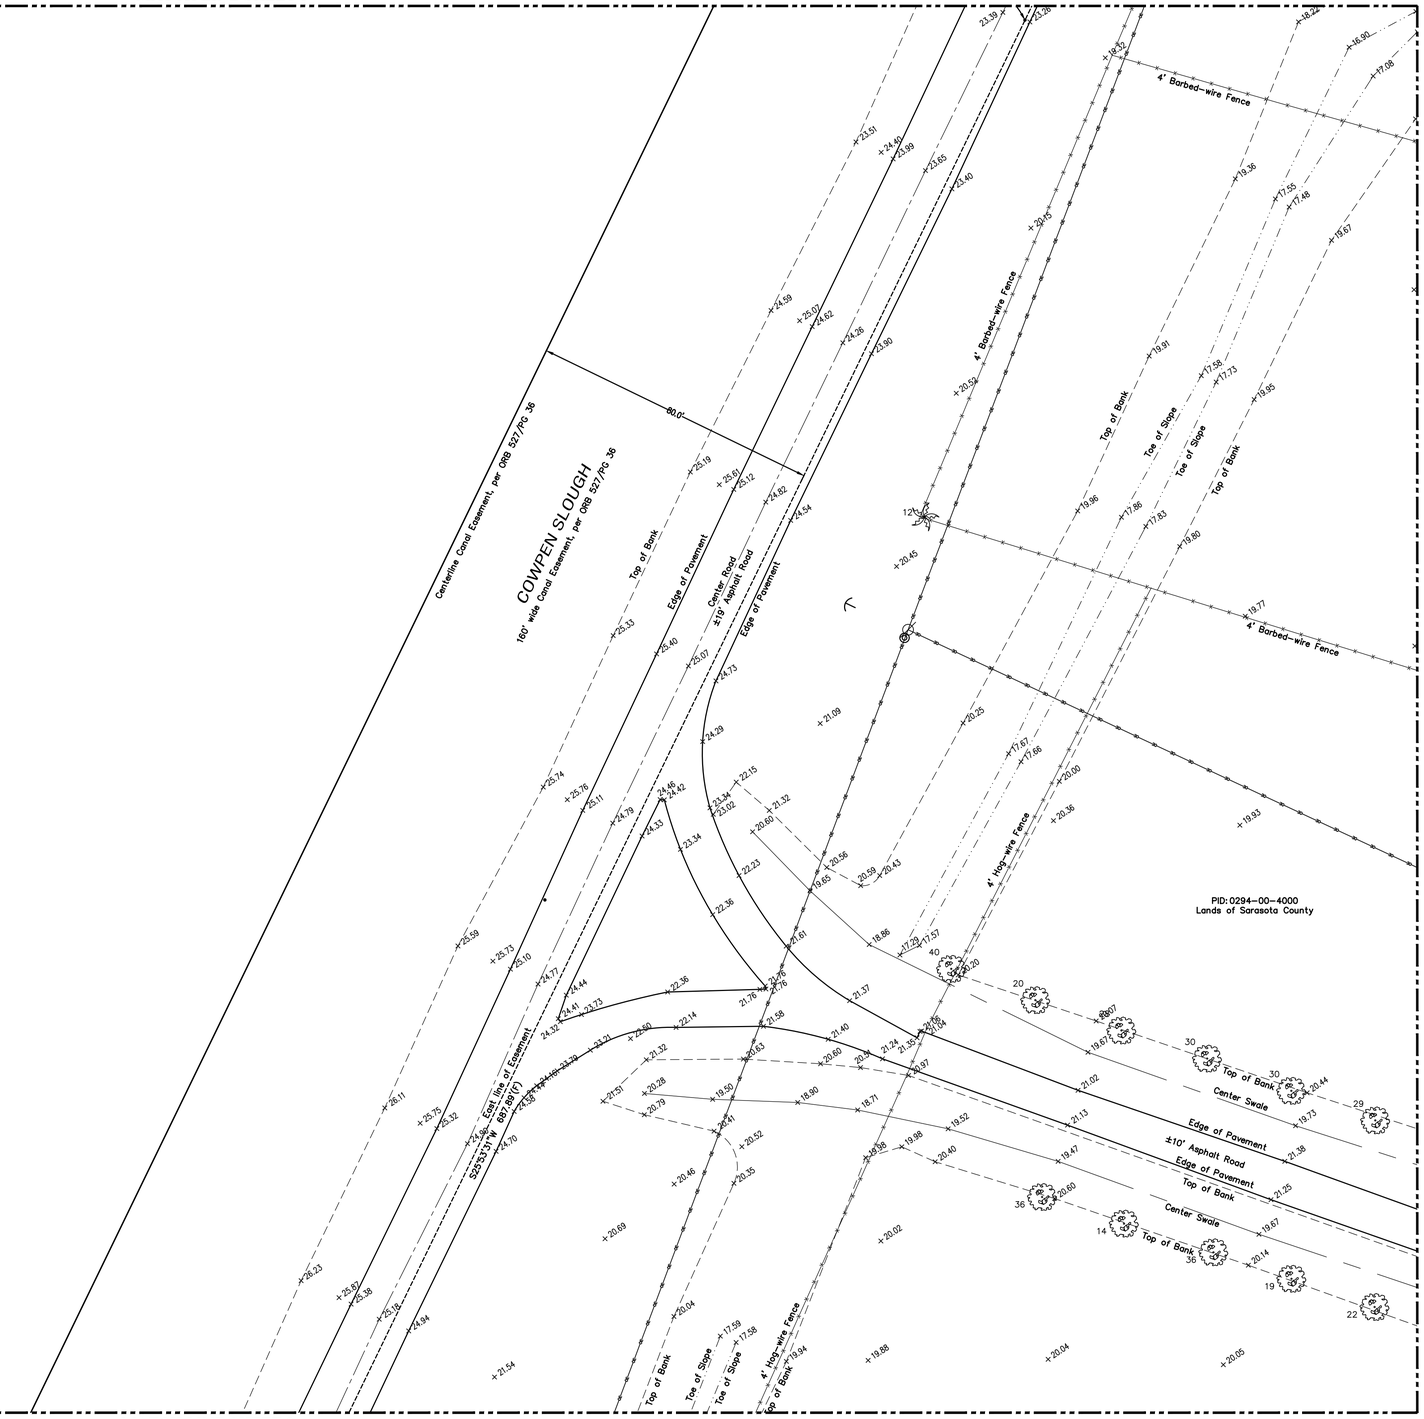

MATCH LINE SHEET 7

MATCH LINE SHEET 9

0' 20' 40'
GRAPHIC SCALE 1" = 20' (US Survey Feet)

© COPYRIGHT Geosurv, LLC, 2026. All Rights Reserved.

NOT VALID UNLESS CONTAINING ALL SHEETS

	REVISION	DRAWN	DATE
1.			
2.			
3.			
4.			

L:\Geosurv Company\Company Work Drive\Projects\260036\260036_SPS.dwg

GEOSURV SURVEYING & MAPPING
5707 19th Street W.
Bradenton, Florida 34207
Tel. 877.407.3734
Fax 866.624.5163
www.geosurveygroup.com L.B. 7731 info@geosurveygroup.com

MAP OF SPECIFIC PURPOSE SURVEY

LYING IN SECTION 22, & 27, TOWNSHIP 37 SOUTH, RANGE 19 EAST,
SARASOTA COUNTY, FLORIDA.

MATCH LINE SHEET 5

MATCH LINE SHEET 6

MATCH LINE SHEET 8

LEGEND

These standard symbols and abbreviations can be found herein.

- Benchmark, as denoted
- "X"/Cross Cut found
- Corner set, Nail & Disk, or 5/8" Iron Rod & Cap (LB7731).
- Corner found, as denoted.
- Monument set, 4" Concrete (LB7731)
- Monument found, as denoted
- Mail Box
- Bollard Post, as denoted
- Wood Sign Post
- Metal Sign Post
- Yard Drain
- Storm Grate Inlet
- Underdrain Cleanout
- Sanitary Sewer Cleanout
- Backflow preventer
- Water Meter
- Reuse Water Meter
- Irrigation Control Valve
- Well
- Septic Tank Lid
- Fire Hydrant
- Gate Valve, as denoted
- Sanitary Sewer Manhole
- Storm Sewer Manhole
- Electric Manhole
- Utility Manhole
- Unknown Manhole
- Wood Power Pole
- Concrete Power Pole
- Metal Power Pole
- Metal Light Pole
- Wood Light Pole
- Flood/Yard Light
- Metal Flag Pole
- Concrete Light Pole
- Guy Wire Anchor
- Cross-walk Signal Post
- Power Transformer pad
- Utility Pull Box
- Utility Hand Hole
- Utility Riser
- Utility Cabinet
- Bore Sample Location
- Gas Valve
- Gas line marker
- Palm Tree
- Oak Tree
- Pine Tree
- Citrus Tree
- Banyan Tree
- Unknown Tree
- Spot Elevation

(R) Radial
(NR) Non-Radial
(D) Deed
(P) Plat
(F) Field
(C) Calculated.
CB Chord Bearing
CH Chord Distance
A Arc Distance
D Delta
L Line
C Curve
OA Overall
N: Northing
E: Easting
STA Station
OS Offset
R Right Offset
L Left Offset
WT Witness Corner
POL Point on-line
PCP Permanent Control Point
PRM Permanent Reference Monument.
PID Parcel Identification Number
ORB Official Records Book.
ORI Official Records Instrument
PG Page.
FB Field Book.
PB Plat Book.
DB Deed Book.
CCR Certified Corner Record
NGS National Geodetic Survey
FDEP Dept. of Environmental Protection
FDOT Dept. of Transportation
FIRM Flood Insurance Rate Map
BFE Base Flood Elevation
NAD North American Datum
NAVD North American Vertical Datum
NGVD National Geodetic Vertical Datum
LS Licensed Surveyor
LB Licensed Business.
PLS Professional Land Surveyor.
RLS Registered Land Surveyor.
PSM Professional Surveyor & Mapper
MTS Minimum Technical Standards
A/C Air Conditioner
FF Finish Floor Elevation
GF Garage Floor Elevation
WIN Weir Invert
INV Pipe Invert
MES Mitered End Section
EOP End of Pipe
GAS Gas Main
STM Storm Drain
SAN Sanitary Main
SFM Sanitary Force Main
RUW Reuse Water Main
IRR Irrigation Line
W Water Main
FS Fire Service
FDC Fire Department Connection
UGE Underground Electric
UGT Underground Telephone
UGTV Underground Television
OE Overhead Electric
UNK Unknown

Top of Bank
Toe of Slope
4' Barbed-wire Fence
4' Hog-wire Fence
6' Wooden Fence
Tree/Vegetation Line
Heavily Wooded Area
Edge of Pavement
Asphalt Road
Concrete slab
Metal Shed
Hog pens
Frame/Screen Greenhouse
Concrete pad
Building Overhang line
Covered Dirt Floor/Horse Barn
ONE Story Wood Frame Garage
21.60FF
Covered Concrete
Wood Frame Shed
Covered Dirt Floor Horse Barn
PID:0294--00--4000
Lands of Sarasota County

KEY MAP
Not to Scale

0' 20' 40'
GRAPHIC SCALE 1" = 20' (US Survey Feet)

© COPYRIGHT Geosurv, LLC, 2026. All Rights Reserved.

NOT VALID UNLESS CONTAINING ALL SHEETS

	REVISION	DRAWN	DATE
1.			
2.			
3.			
4.			

L:\Geosurv Company\Company Work Drive\Projects\260036\260036_SPS.dwg

GEOSURV SURVEYING & MAPPING
5707 19th Street W.
Bradenton, Florida 34207
Tel. 877.407.3734
Fax 866.624.5163
www.geosurveygroup.com L.B. 7731 info@geosurveygroup.com

MAP OF SPECIFIC PURPOSE SURVEY

LYING IN SECTION 22, & 27, TOWNSHIP 37 SOUTH, RANGE 19 EAST,
SARASOTA COUNTY, FLORIDA.

MATCH LINE SHEET 7

MATCH LINE SHEET 9

LEGEND

These standard symbols and abbreviations can be found herein.

- Benchmark, as denoted
- "X"/Cross Cut found
- Corner set, Nail & Disk, or 5/8" Iron Rod & Cap (LB7731).
- Corner found, as denoted.
- Monument set, 4" Concrete (LB7731)
- Monument found, as denoted
- Mail Box
- Bollard Post, as denoted
- Wood Sign Post
- Metal Sign Post
- Yard Drain
- Storm Grate Inlet
- Underdrain Cleanout
- Sanitary Sewer Cleanout
- Backflow preventer
- Water Meter
- Reuse Water Meter
- Irrigation Control Valve
- Well
- Septic Tank Lid
- Fire Hydrant
- Gate Valve, as denoted
- Sanitary Sewer Manhole
- Storm Sewer Manhole
- Electric Manhole
- Utility Manhole
- Unknown Manhole
- Wood Power Pole
- Concrete Power Pole
- Metal Power Pole
- Metal Light Pole
- Wood Light Pole
- Flood/Yard Light
- Metal Flag Pole
- Concrete Light Pole
- Guy Wire Anchor
- Cross-walk Signal Post
- Power Transformer pad
- Utility Pull Box
- Utility Hand Hole
- Utility Riser
- Utility Cabinet
- Bore Sample Location
- Gas Valve
- Gas line marker
- Palm Tree
- Oak Tree
- Pine Tree
- Citrus Tree
- Banyan Tree
- Unknown Tree
- Spot Elevation
- (R) Radial
- (NR) Non-Radial
- (D) Deed
- (P) Plat
- (F) Field
- (C) Calculated.
- CB Chord Bearing
- CH Chord Distance
- A Arc Distance
- D Delta
- L Line
- C Curve
- OA Overall
- N: Northing
- E: Easting
- STA Station
- OS Offset
- R Right Offset
- L Left Offset
- WT Witness Corner
- POL Point on-line
- PCP Permanent Control Point
- PRM Permanent Reference Monument.
- PID Parcel Identification Number
- ORB Official Records Book.
- ORI Official Records Instrument
- PG Page.
- FB Field Book.
- PB Plat Book.
- DB Deed Book.
- CCR Certified Corner Record
- NGS National Geodetic Survey
- FDEP Dept. of Environmental Protection
- FDOT Dept. of Transportation
- FIRM Flood Insurance Rate Map
- BFE Base Flood Elevation
- NAD North American Datum
- NAVD North American Vertical Datum
- NGVD National Geodetic Vertical Datum
- LS Licensed Surveyor
- LB Licensed Business.
- PLS Professional Land Surveyor.
- RLS Registered Land Surveyor.
- PSM Professional Surveyor & Mapper
- MTS Minimum Technical Standards
- A/C Air Conditioner
- FF Finish Floor Elevation
- GF Garage Floor Elevation
- WIN Weir Invert
- INV Pipe Invert
- MES Mitered End Section
- EOP End of Pipe
- GAS Gas Main
- STM Storm Drain
- SAN Sanitary Main
- SFM Sanitary Force Main
- RUW Reuse Water Main
- IRR Irrigation Line
- W Water Main
- FS Fire Service
- FDC Fire Department Connection
- UGE Underground Electric
- UGT Underground Telephone
- UGTV Underground Television
- OE Overhead Electric
- UNK Unknown

PID: 0294-00-4000
Lands of Sarasota County

Edge of Pavement
Asphalt Road
Edge of Pavement

Wood steps
Brick pavers
Wood steps
Covered Wood Deck
43.5'
11.8'
76.6'
ONE Story Wood Frame Residence
24.19'FF
6.2' Covered/Screen Wood Deck
40.3'
Wood steps
Conc.
Rock Fire pit


Wood Frame
Well house
Wood steps
42.3'
Concrete
A/C pad
Water Heater
Closet
33.7'
38.1'
Covered Shell
Building Overhang
29.1'
38.0'
Wood steps
22.6'
12.1'
10.1'
27.0'
2.6'
2.6'
6.0'
37.4'
Concrete
A/C pad

ZONE A
ZONE X
Approximate Flood Zone Line, scaled from FIRM
4' Hog-wire Fence
Tree/Vegetation Line
Heavily Wooded Area

Rabbit
Kennels
24.3'
10.9'
4' Hog-wire Fence
Heavily Wooded Area
Tree/Vegetation Line

South line of Section 22-37S-19E

ZONE X
ZONE A
Approximate Flood Zone Line, scaled from FIRM
Tree/Vegetation Line

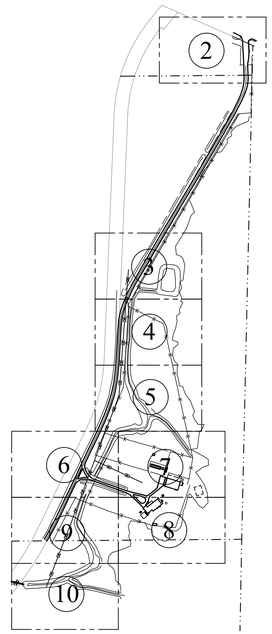

KEY MAP
Not to Scale

0' 20' 40'
GRAPHIC SCALE 1" = 20' (US Survey Feet)

© COPYRIGHT Geosurv, LLC, 2026. All Rights Reserved.

NOT VALID UNLESS CONTAINING ALL SHEETS

	REVISION	DRAWN	DATE
1.			
2.			
3.			
4.			

L:\Geosurv Company\Company Work Drive\Projects\260036\260036_SPS.dwg

GEOSURV SURVEYING & MAPPING
www.geosurveygroup.com L.B. 7731
5707 19th Street W.
Bradenton, Florida 34207
Tel. 877.407.3734
Fax 866.624.5163
info@geosurveygroup.com

MAP OF SPECIFIC PURPOSE SURVEY


LYING IN SECTION 22, & 27, TOWNSHIP 37 SOUTH, RANGE 19 EAST,
SARASOTA COUNTY, FLORIDA.

MATCH LINE SHEET 6

LEGEND

These standard symbols and abbreviations can be found herein.

- Benchmark, as denoted
- "X"/Cross Cut found
- Corner set, Nail & Disk, or 5/8" Iron Rod & Cap (LB7731).
- Corner found, as denoted.
- Monument set, 4" Concrete (LB7731)
- Monument found, as denoted
- Mail Box
- Bollard Post, as denoted
- Wood Sign Post
- Metal Sign Post
- Yard Drain
- Storm Grate Inlet
- Underdrain Cleanout
- Sanitary Sewer Cleanout
- Backflow preventer
- Water Meter
- Reuse Water Meter
- Irrigation Control Valve
- Well
- Septic Tank Lid
- Fire Hydrant
- Gate Valve, as denoted
- Sanitary Sewer Manhole
- Storm Sewer Manhole
- Electric Manhole
- Utility Manhole
- Unknown Manhole
- Wood Power Pole
- Concrete Power Pole
- Metal Power Pole
- Metal Light Pole
- Wood Light Pole
- Flood/Yard Light
- Metal Flag Pole
- Concrete Light Pole
- Guy Wire Anchor
- Cross-walk Signal Post
- Power Transformer pad
- Utility Pull Box
- Utility Hand Hole
- Utility Riser
- Utility Cabinet
- Bore Sample Location
- Gas Valve
- Gas line marker
- Palm Tree
- Oak Tree
- Pine Tree
- Citrus Tree
- Banyan Tree
- Unknown Tree
- Spot Elevation
- (R) Radial
- (NR) Non-Radial
- (D) Deed
- (P) Plat
- (F) Field
- (C) Calculated.
- CB Chord Bearing
- CH Chord Distance
- A Arc Distance
- D Delta
- L Line
- C Curve
- OA Overall
- N: Northing
- E: Easting
- STA Station
- OS Offset
- R Right Offset
- L Left Offset
- WT Witness Corner
- POL Point on-line
- PCP Permanent Control Point
- PRM Permanent Reference Monument.
- PID Parcel Identification Number
- ORB Official Records Book.
- OR Official Records Instrument
- PG Page.
- FB Field Book.
- PB Plat Book.
- DB Deed Book.
- CCR Certified Corner Record
- NGS National Geodetic Survey
- FDEP Dept. of Environmental Protection
- FDOT Dept. of Transportation
- FIRM Flood Insurance Rate Map
- BFE Base Flood Elevation
- NAD North American Datum
- NAVD North American Vertical Datum
- NGVD National Geodetic Vertical Datum
- LS Licensed Surveyor
- LB Licensed Business.
- PLS Professional Land Surveyor.
- RLS Registered Land Surveyor.
- PSM Professional Surveyor & Mapper
- MTS Minimum Technical Standards
- A/C Air Conditioner
- FF Finish Floor Elevation
- GF Garage Floor Elevation
- WN Weir Invert
- INV Pipe Invert
- MES Mitered End Section
- EOP End of Pipe
- GAS Gas Main
- STM Storm Drain
- SAN Sanitary Main
- SFM Sanitary Force Main
- RUW Reuse Water Main
- IRR Irrigation Line
- W Water Main
- FS Fire Service
- FDC Fire Department Connection
- USE Underground Electric
- UGT Underground Telephone
- UGTV Underground Television
- OE Overhead Electric
- UNK Unknown

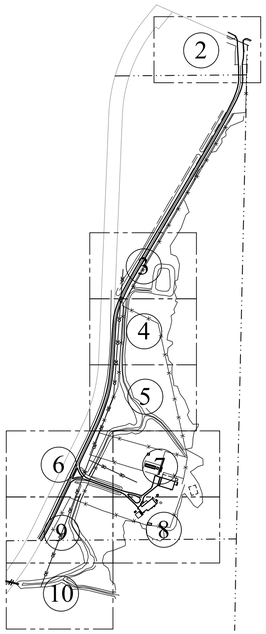

KEY MAP
Not to Scale

Centerline Canal Easement, per ORB 527/PG 36
COWPEN SLOUGH
160' Wide Canal Easement, per ORB 527/PG 36
80.0'
S25°53'31"W 697.88'(C)
Top of Bank
Edge of Pavement
±15' Asphalt Road
Center Road
Edge of Pavement
East line of Easement
4' Barbed-wire Fence
4' Hog-wire Fence
Top of Bank
Toe of Slope
Toe of Slope
Top of Bank
Nail & Disk (LB7805) Found
PID:0294-00-4000
Lands of Sarasota County
South line of Section 22-37S-19E
(SURVEY THIS AREA, NOT INCLUDED)
Heavily Wooded Area

MATCH LINE SHEET 8

MATCH LINE SHEET 10

0' 20' 40'
GRAPHIC SCALE 1" = 20' (US Survey Feet)

© COPYRIGHT Geosurv, LLC, 2026. All Rights Reserved.

NOT VALID UNLESS CONTAINING ALL SHEETS

	REVISION	DRAWN	DATE
1.			
2.			
3.			
4.			


L:\Geosurv Company\Company Work Drive\Projects\260036\260036_SPS.dwg

GEOSURV SURVEYING & MAPPING
5707 19th Street W.
Bradenton, Florida 34207
Tel. 877.407.3734
Fax 866.624.5163
www.geosurveygroup.com L.B. 7731 info@geosurveygroup.com

MAP OF SPECIFIC PURPOSE SURVEY

LYING IN SECTION 22, & 27, TOWNSHIP 37 SOUTH, RANGE 19 EAST,
SARASOTA COUNTY, FLORIDA.

MATCH LINE SHEET 9

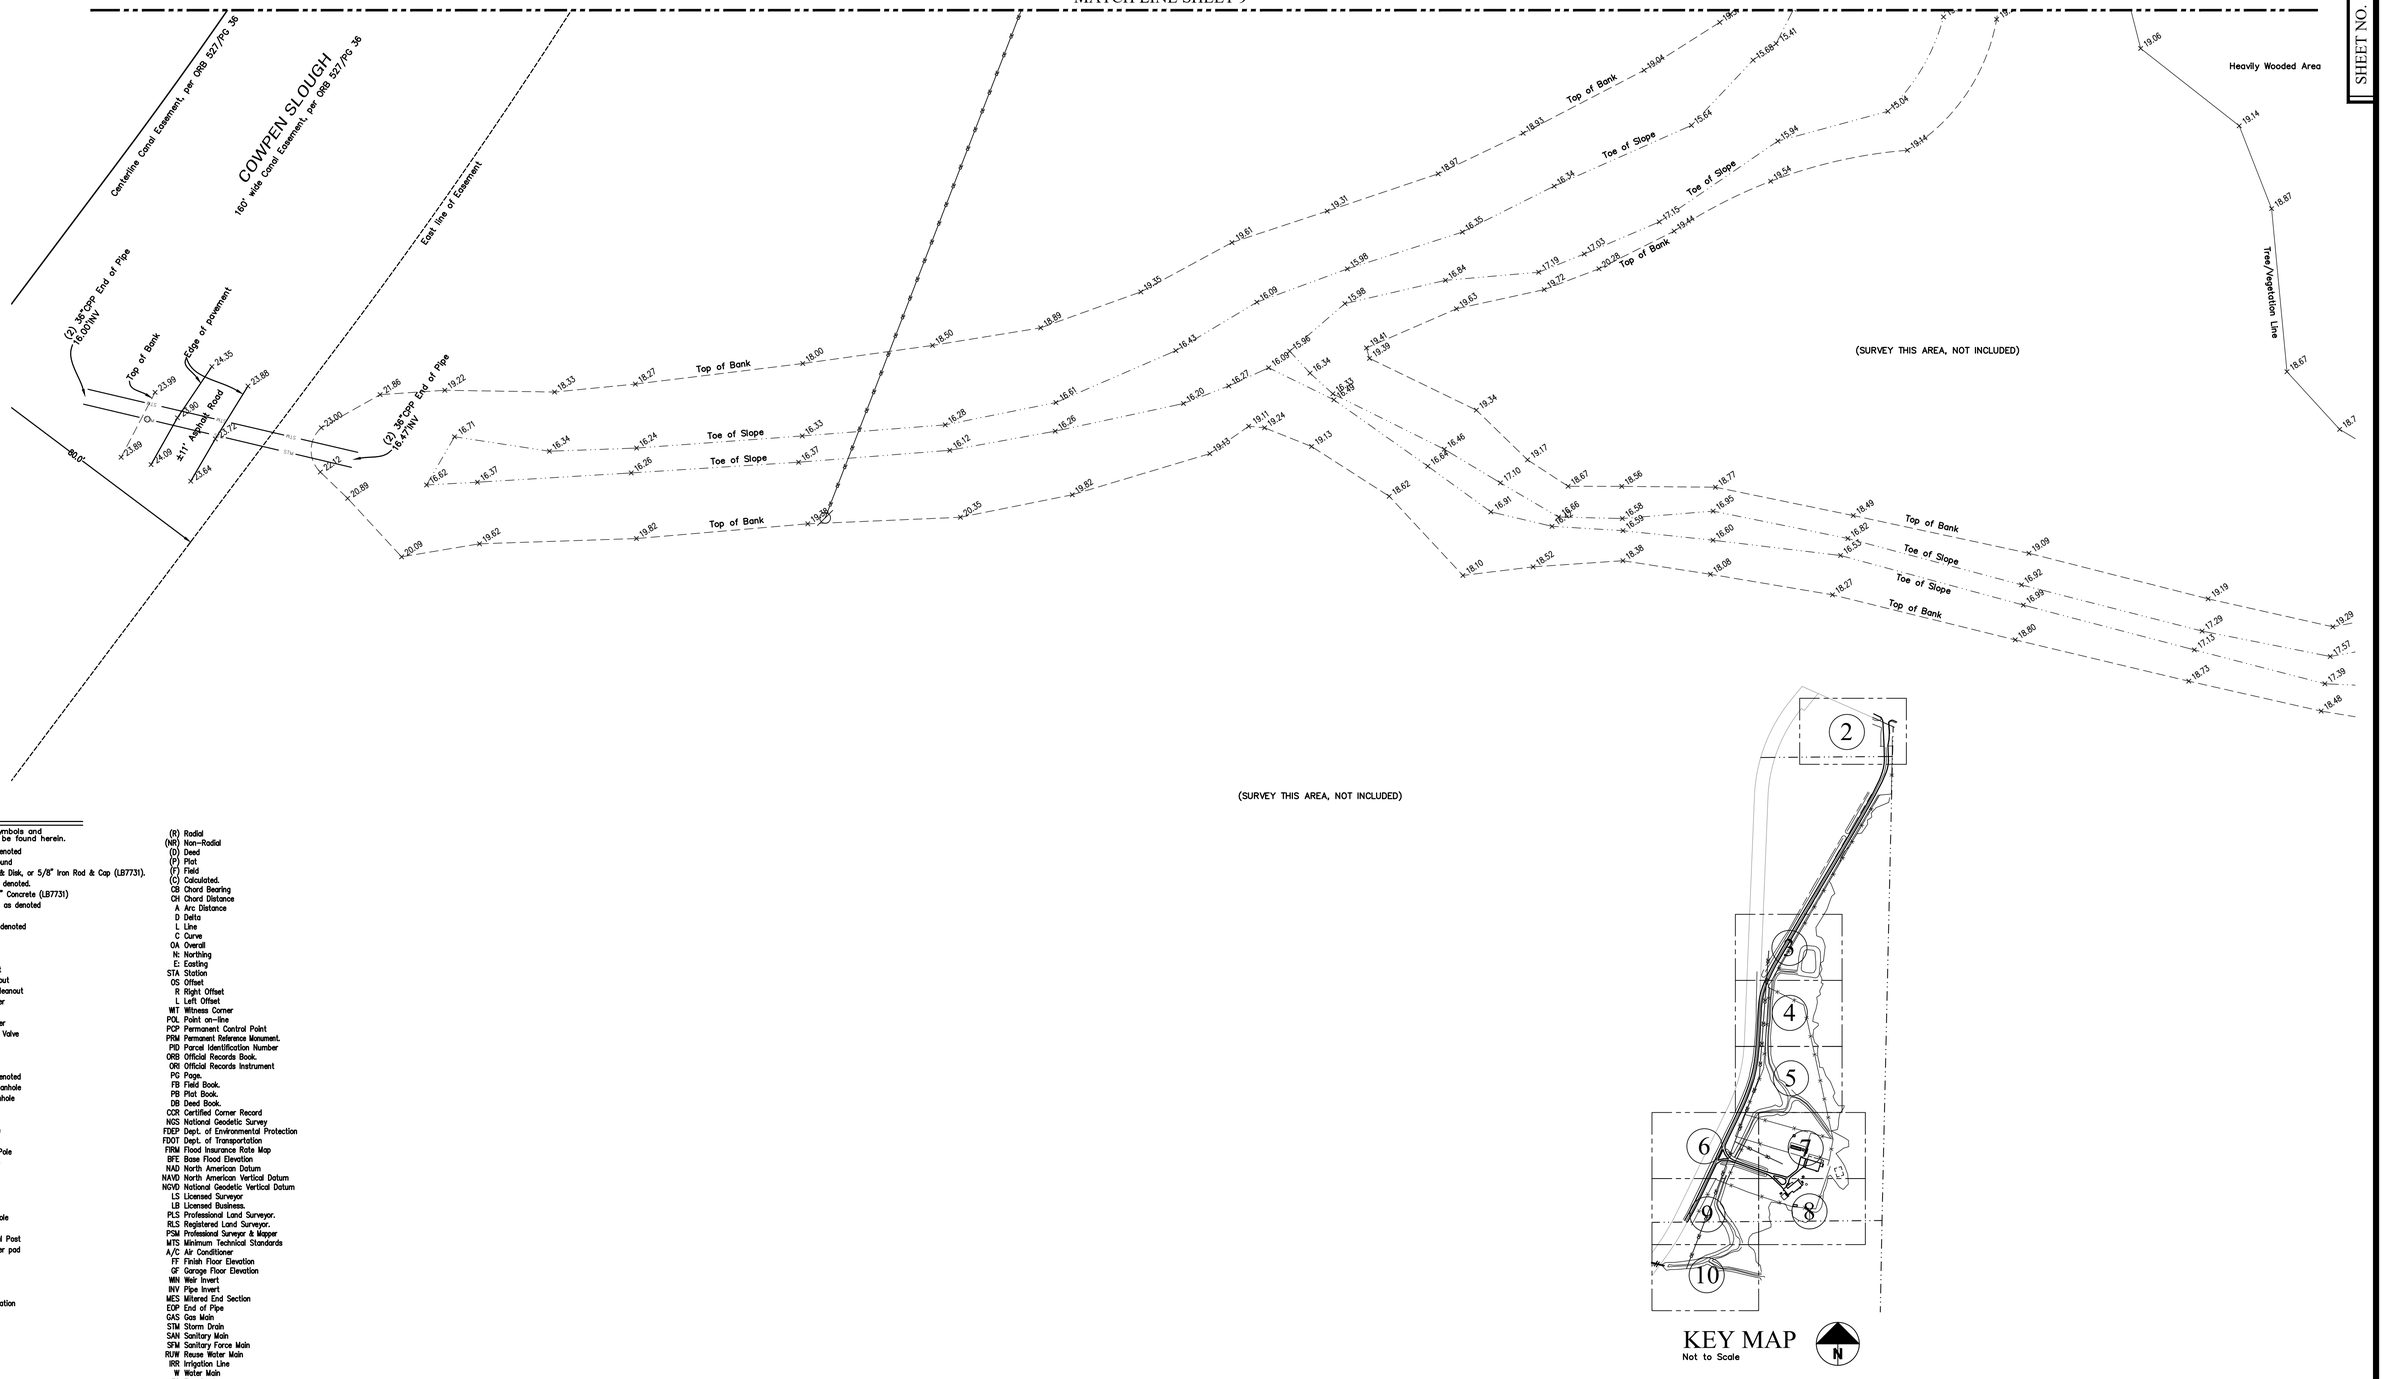

LEGEND

These standard symbols and abbreviations can be found herein.

- Benchmark, as denoted
- "X"/Cross Cut found
- Corner set, Nail & Disk, or 5/8" Iron Rod & Cap (LB7731).
- Corner found, as denoted.
- Monument set, 4" Concrete (LB7731)
- Monument found, as denoted
- Mail Box
- Bollard Post, as denoted
- Wood Sign Post
- Metal Sign Post
- Yard Drain
- Storm Grate Inlet
- Underdrain Cleanout
- Sanitary Sewer Cleanout
- Backflow preventer
- Water Meter
- Reuse Water Meter
- Irrigation Control Valve
- Well
- Septic Tank Lid
- Fire Hydrant
- Gate Valve, as denoted
- Sanitary Sewer Manhole
- Storm Sewer Manhole
- Electric Manhole
- Utility Manhole
- Unknown Manhole
- Wood Power Pole
- Concrete Power Pole
- Metal Power Pole
- Metal Light Pole
- Wood Light Pole
- Flood/Yard Light
- Metal Flag Pole
- Concrete Light Pole
- Guy Wire Anchor
- Cross-walk Signal Post
- Power Transformer pad
- Utility Pull Box
- Utility Hand Hole
- Utility Riser
- Utility Cabinet
- Bore Sample Location
- Gas Valve
- Gas line marker
- Palm Tree
- Oak Tree
- Pine Tree
- Citrus Tree
- Banyan Tree
- Unknown Tree
- Spot Elevation

(R)	Radial
(NR)	Non-Radial
(D)	Deed
(P)	Plat
(F)	Field
(C)	Calculated.
CB	Chord Bearing
CH	Chord Distance
A	Arc Distance
D	Delta
L	Line
C	Curve
OA	Overall
N:	Northing
E:	Easting
STA	Station
OS	Offset
R	Right Offset
L	Left Offset
WIT	Witness Corner
POL	Point on-line
PCP	Permanent Control Point
PRM	Permanent Reference Monument.
PID	Parcel Identification Number
ORB	Official Records Book.
ORI	Official Records Instrument
PG	Page.
FB	Field Book.
PB	Plat Book.
DB	Deed Book.
CCR	Certified Corner Record
NGS	National Geodetic Survey
FDEP	Dept. of Environmental Protection
FDOT	Dept. of Transportation
FIRM	Flood Insurance Rate Map
BFE	Base Flood Elevation
NAD	North American Datum
NAVD	North American Vertical Datum
NGVD	National Geodetic Vertical Datum
LS	Licensed Surveyor
LB	Licensed Business.
PLS	Professional Land Surveyor.
RLS	Registered Land Surveyor.
PSM	Professional Surveyor & Mapper
MTS	Minimum Technical Standards
A/C	Air Conditioner
FF	Finish Floor Elevation
GF	Garage Floor Elevation
WIN	Weir Invert
INV	Pipe Invert
MES	Mitered End Section
EOP	End of Pipe
GAS	Gas Main
STM	Storm Drain
SAN	Sanitary Main
SFM	Sanitary Force Main
RUW	Reuse Water Main
IRR	Irrigation Line
W	Water Main
FS	Fire Service
FDC	Fire Department Connection
UGE	Underground Electric
UGT	Underground Telephone
UGTV	Underground Television
OE	Overhead Electric
UNK	Unknown

KEY MAP
Not to Scale

0' 20' 40'
GRAPHIC SCALE 1" = 20' (US Survey Feet)

© COPYRIGHT Geosurv, LLC, 2026. All Rights Reserved.

NOT VALID UNLESS CONTAINING ALL SHEETS

	REVISION	DRAWN	DATE
1.			
2.			
3.			
4.			

L:\Geosurv Company\Company Work Drive\Projects\260036\260036_SPS.dwg

GEOSURV SURVEYING & MAPPING
www.geosurveygroup.com L.B. 7731
5707 19th Street W.
Bradenton, Florida 34207
Tel. 877.407.3734
Fax 866.624.5163
info@geosurveygroup.com