
PRE-ENGINEERED BUILDING SYSTEM (PEB) NOTES:

1. THESE DRAWINGS ARE INTENDED TO ILLUSTRATE DESIGN INTENT ONLY AND DO NOT ILLUSTRATE ALL COMPONENTS REQUIRED FOR A COMPLETE BUILDING SYSTEM. PROVIDE AND INSTALL ALL COMPONENTS WITHIN VENDOR SCOPE REQUIRED FOR A COMPLETE BUILDING SYSTEM IN COMPLIANCE WITH THESE DRAWINGS, SPECIFICATIONS (REFER TO SECTION 13 34 00) APPLICABLE CODES AND MANUFACTURER'S RECOMMENDATIONS.
2. SEE PLANS, ELEVATIONS, SECTIONS AND DETAILS FOR LOCATION AND CONFIGURATION OF SYSTEM COLUMNS, BAR JOISTS, FRAMING, OPENINGS, CLADDING AND FINISHES AND FOR RELATIONSHIP OF PRE-ENGINEERED SYSTEM TO OTHER SYSTEMS.
3. CONTRACTOR TO SUBMIT SHOP DRAWINGS TO ARCHITECT FOR APPROVAL PRIOR TO FABRICATION. SHOP DRAWINGS TO INCLUDE CALCULATIONS CERTIFIED BY A FLORIDA LICENSED ENGINEER'S SIGNATURE AND SEAL THAT DEMONSTRATE SYSTEM'S STRUCTURAL DESIGN COMPLIES WITH WIND LOAD CRITERIA PER FBC 2020(SEVENTH EDITION). THIS INCLUDES THE DESIGN OF THE CONCRETE FOOTINGS(CONCRETE FLOOR SLABS BY OTHERS)
4. TO BE INCLUDED IN VENDOR PACKAGE:
   - FOOTING DESIGN
   - 8" X 8" NOM. PT WD COLUMNS
   - PRE-MANUFACTURED STEEL ROOF TRUSSES
   - 2X ROOF FRAMING
   - GALVALUME METAL ROOF PANELS
   - METAL CLOSURE TRIM AT TOP, BOTTOM, AND CORNERS, RIDGE, FASCIA, ETC.
5. NOT INCLUDED IN VENDOR PACKAGE TO BE PROVIDED BY CONTRACTOR:
   - CONCRETE FOR FOOTINGS
   - CONCRETE FLOOR SLABS- SEE STRUCTURAL
   - GUTTERS AND DOWNSPOUTS
   - GATES AND PANELS
   - ELECTRICAL, TECHNOLOGY, AND LIGHTING CONDUIT, WIRING, AND EQUIPMENT - SEE ELECTRICAL DRAWINGS
   - PLUMBING FIXTURES, PIPING, AND FLOOR DRAINS - SEE PLUMBING DWGS
   - SIGNAGE

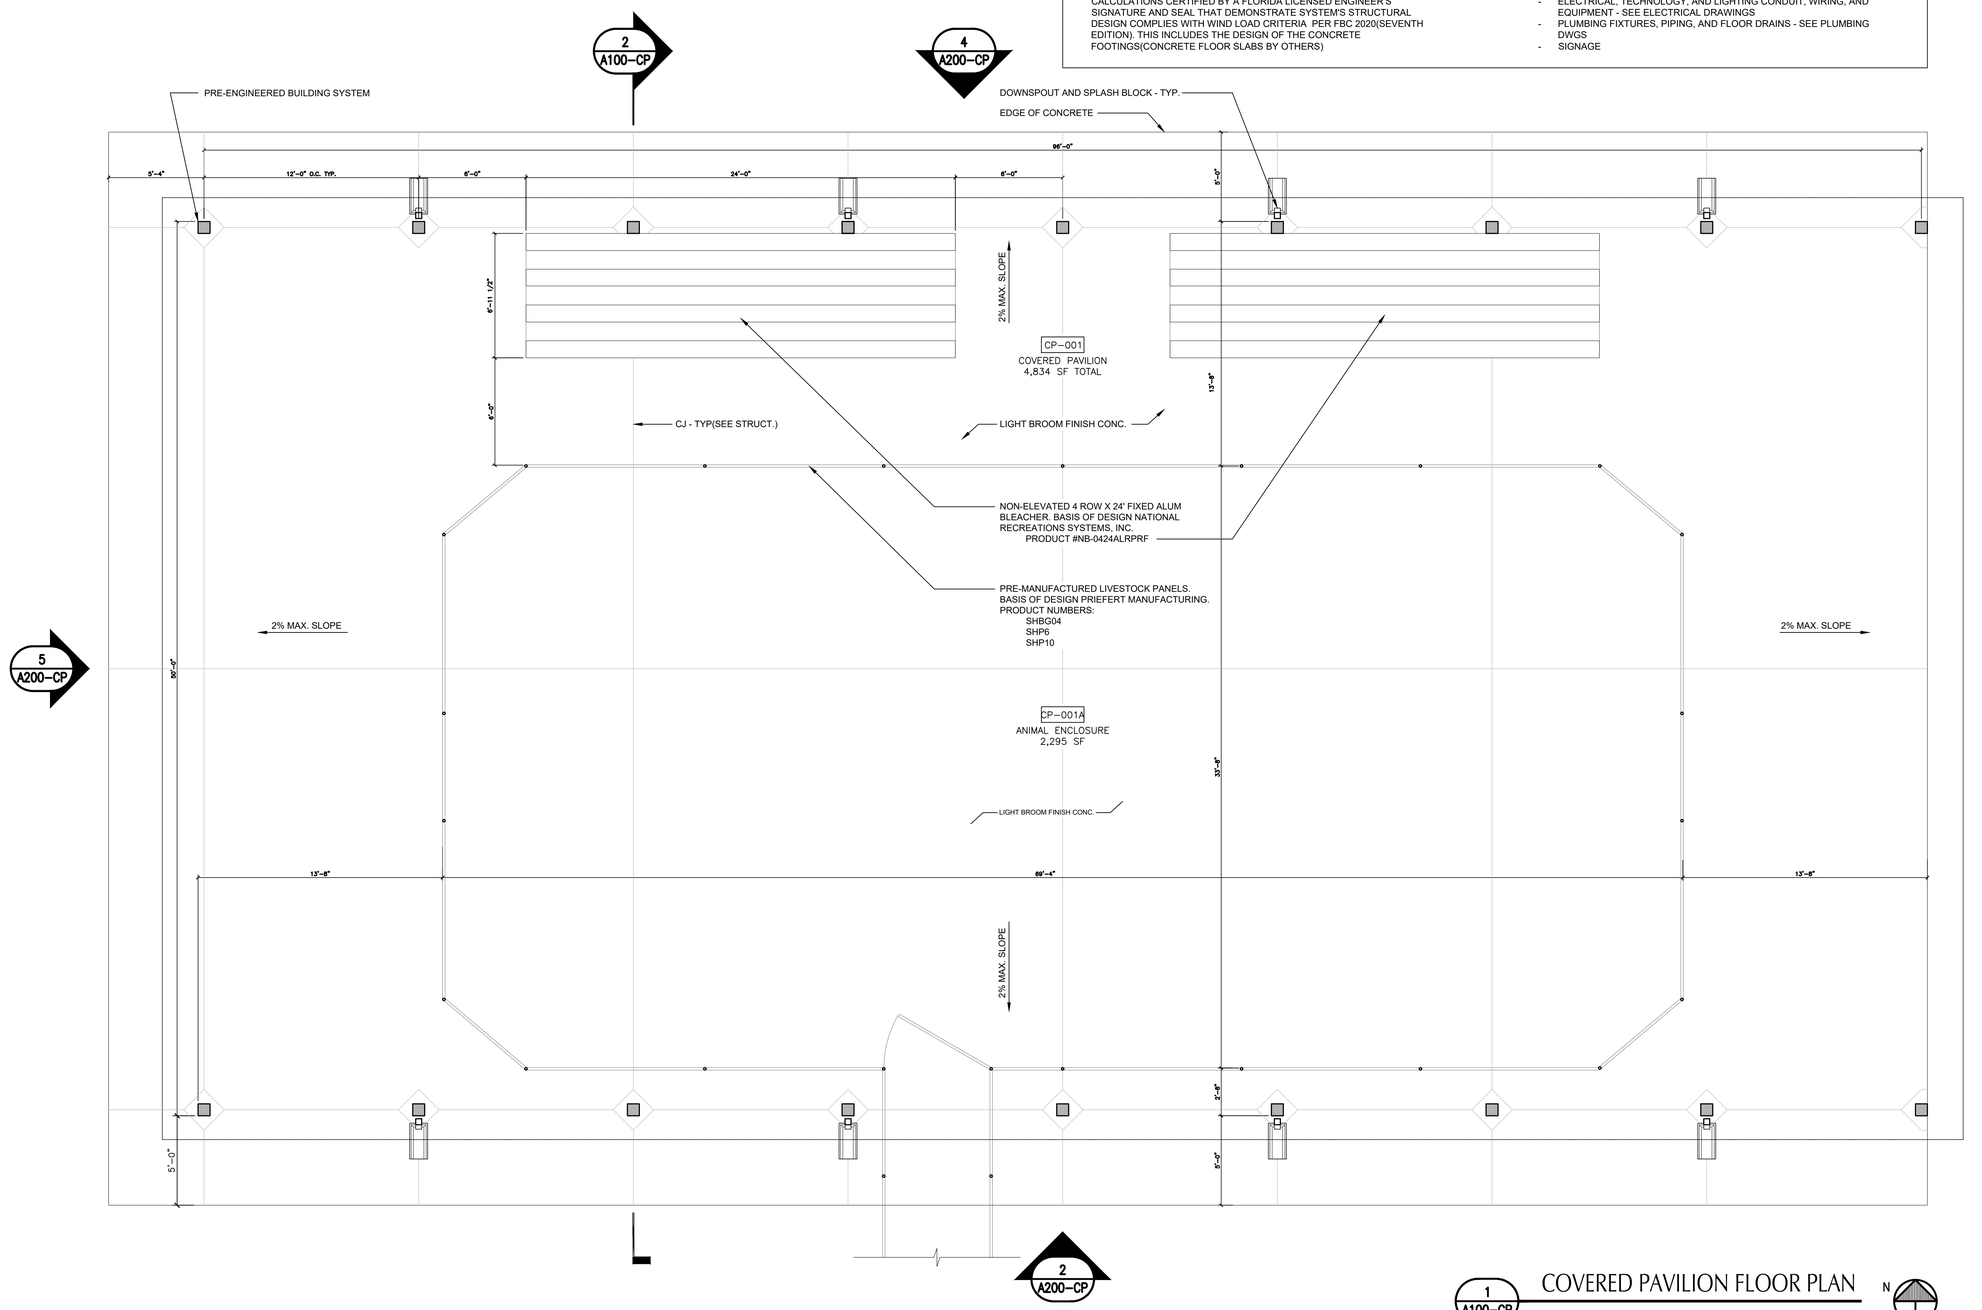

1 A100–CP — COVERED PAVILION FLOOR PLAN

SCALE 1/4" = 1'-0"

N

These plans are protected by Federal Copyright protection. Unauthorized replication, use, or distribution may result in infringement or legal action. THIS SHEET SIZE IS 24X36 - PRINTING TO OTHER SIZES WILL NOT BE TO SCALE

THE SCHOOL BOARD OF SARASOTA COUNTY

CONSTRUCTION SERVICES DEPARTMENT
phone (941) 361-6680 fax (941) 361-6684

DRAWN BY:	WJC
DATE DRAWN:	Mar. 10, 26
CHK'D BY:	SCH
BUILDING NO:	TBD
FLOOR NO:	-
S.C.S.B. PROJ. NO:	TBD
ARCH/ENG. PROJ. NO:	2217
PROJECT PHASE:	SUBMITTED:
CONCEPTUAL PHASE	OCT 20, 2021
SCHEMATIC PHASE	DEC 9, 2022
DESIGN DEV. PHASE	MAR 3, 2023
ISSUED FOR BID	-
ISSUED FOR CONST.	JUN 30, 2023
ISSUED FOR REV.	-
RECORD DRAWINGS	-

DRAWING PHASE: CONSTRUCTION DRAWINGS

REVISION/DESCRIPTION:	DATE
1	-
2	-
3	-
4	-
5	-
6	-
7	-
8	-
9	-
10	-

ARCHITECT/ENGINEER FIRM INFO:
seibert architects
1373 5th Street · Sarasota, FL
34236-4915 - seibertarchitects.com
T 941.366.9161 · F 941.365.0902
Lic. AA-C000070

ARCHITECT/ENGINEER/DESIGN PROF. OF RECORD:
WILLIAM J. CRAIG, AIA AR99330

KEY PLAN:


PROJECT INFORMATION:
MCINTOSH MIDDLE SCHOOL
NEW AGRICULTURAL CENTER

651 MCINTOSH ROAD
SARASOTA FL 34240

SHEET DESCRIPTION:
COVERED PAVILION FLOOR PLAN

DATE PRINTED: -
CAD DWG FILE: -
SHEET: 7 OF: 105

A-100-CP

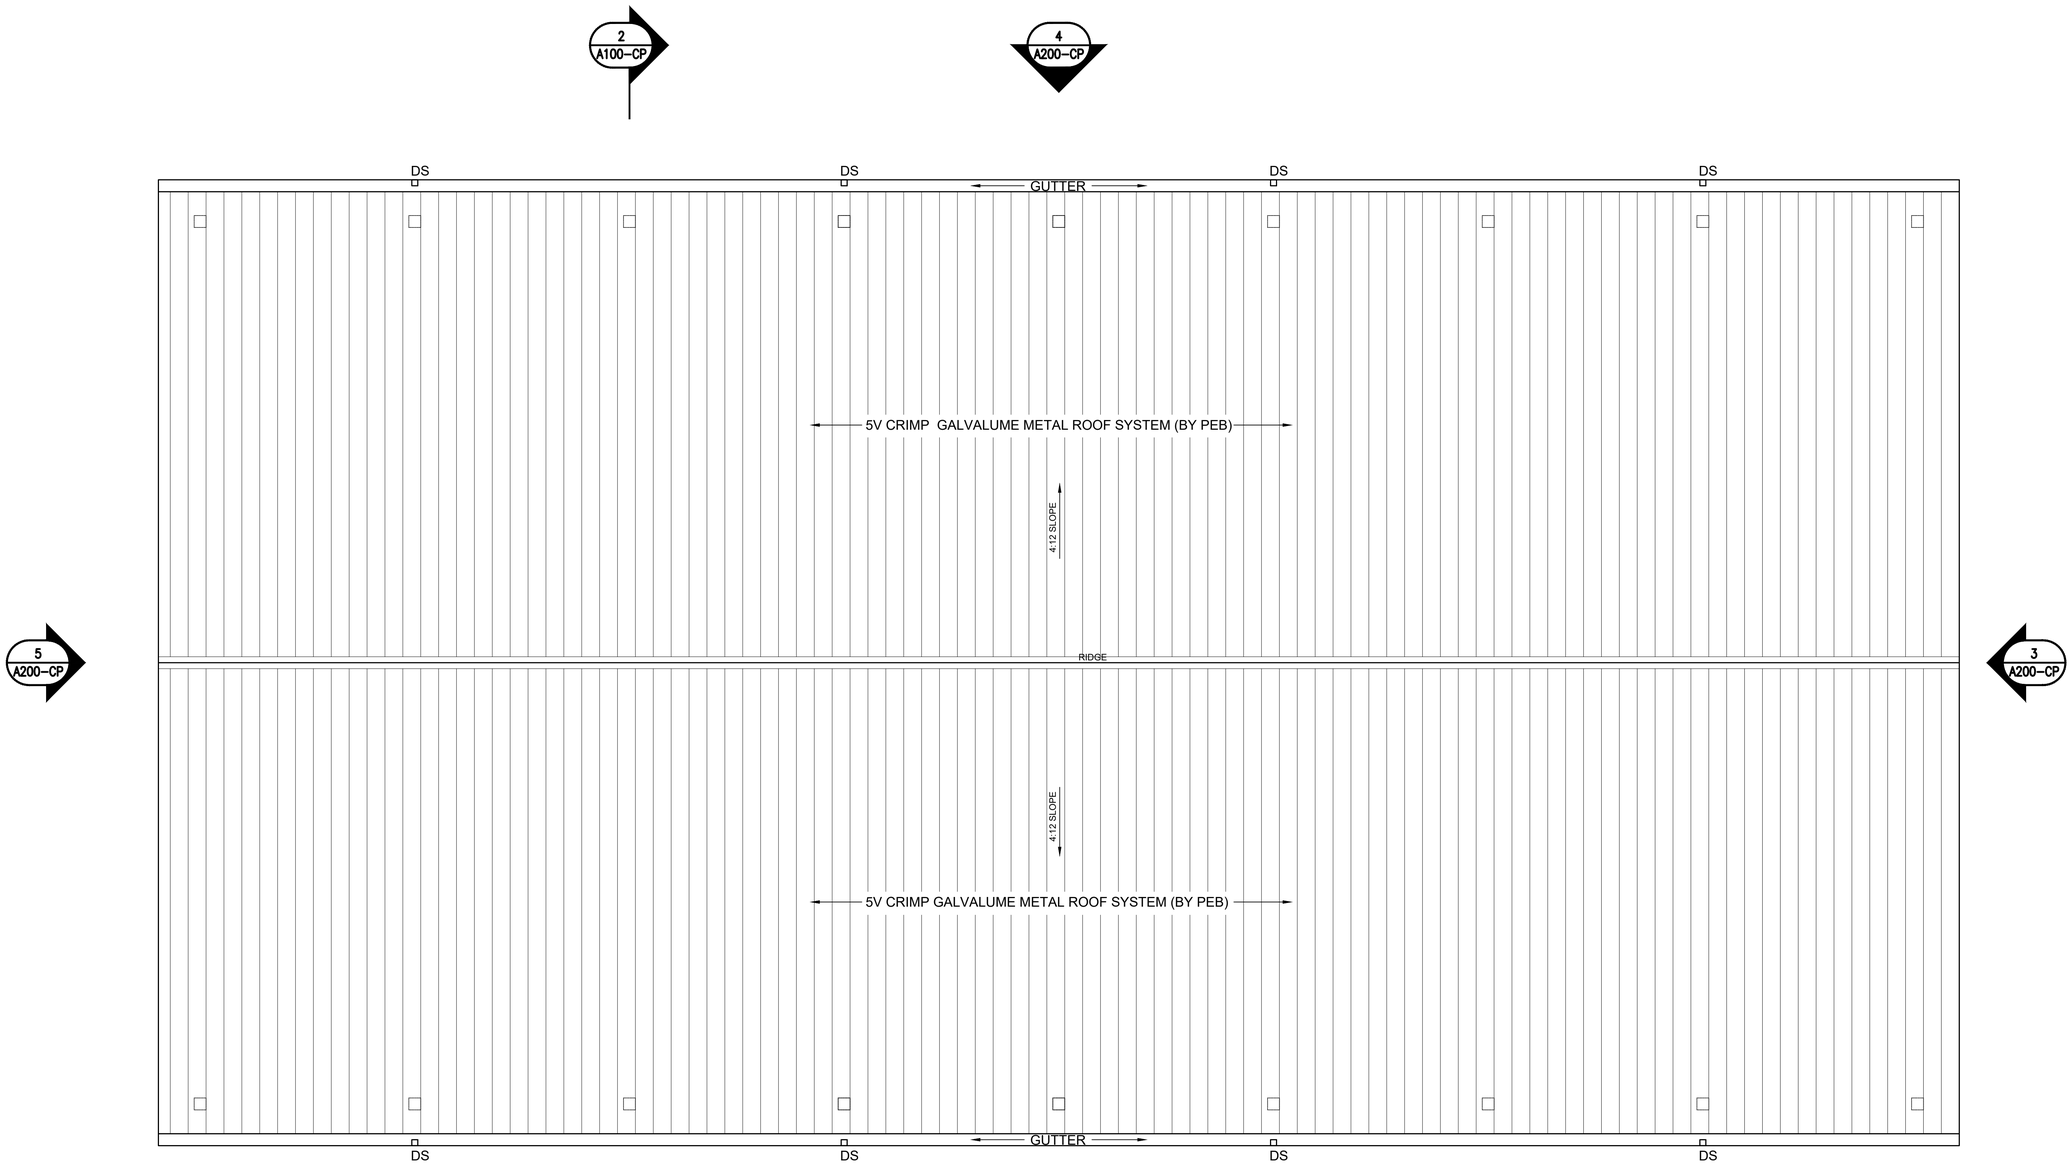

1 A101–CP **COVERED PAVILION ROOF PLAN**

SCALE 1/4" = 1'-0"

N

These plans are protected by Federal Copyright protection. Unauthorized replication, use, or distribution may result in infringement or legal action. THIS SHEET SIZE IS 24X36 - PRINTING TO OTHER SIZES WILL NOT BE TO SCALE

THE SCHOOL BOARD OF SARASOTA COUNTY

CONSTRUCTION SERVICES DEPARTMENT
phone (941) 361-6680 fax (941) 361-6684

DRAWN BY:	WJC
DATE DRAWN:	Mar. 10, 26
CHK'D BY:	SCH
BUILDING NO:	TBD
FLOOR NO:	-
S.C.S.B. PROJ. NO:	TBD
ARCH/ENG. PROJ. NO:	2217
PROJECT PHASE:	SUBMITTED:
CONCEPTUAL PHASE	OCT 20, 2021
SCHEMATIC PHASE	DEC 9, 2022
DESIGN DEV. PHASE	MAR 3, 2023
ISSUED FOR BID	-
ISSUED FOR CONST.	JUN 30, 2023
ISSUED FOR REV.	-
RECORD DRAWINGS	-

DRAWING PHASE: CONSTRUCTION DRAWINGS

DATE	REVISION/DESCRIPTION:
-	-
1	-
2	-
3	-
4	-
5	-
6	-
7	-
8	-
9	-
10	-

ARCHITECT/ENGINEER FIRM INFO:
seibert architects
1373 5th Street - Sarasota, FL
34236-4915 - seibertarchitects.com
T 941.366.9161 - F 941.365.0902
Lic. AA-C000070

ARCHITECT/ENGINEER/DESIGN PROF. OF RECORD:
WILLIAM J. CRAIG, AIA AR99330

KEY PLAN:


PROJECT INFORMATION:
MCINTOSH MIDDLE SCHOOL
NEW AGRICULTURAL CENTER

651 MCINTOSH ROAD
SARASOTA FL 34240

SHEET DESCRIPTION:
COVERED PAVILION ROOF PLAN


DATE PRINTED: -
CAD DWG FILE: -
SHEET: 7 OF: 105

A-101-CP

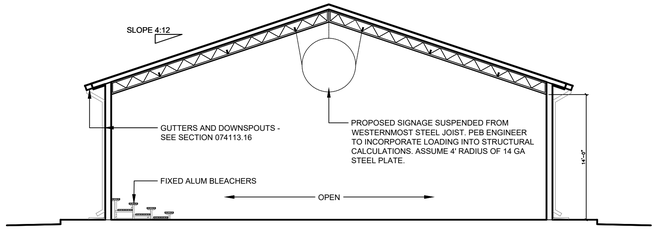


5 A200–CP COVERED PAVILION WEST ELEVATION

SCALE 1/8" = 1'-0"

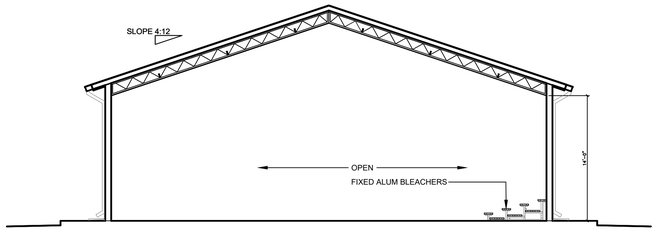


3 A200–CP COVERED PAVILION EAST ELEVATION

SCALE 1/8" = 1'-0"

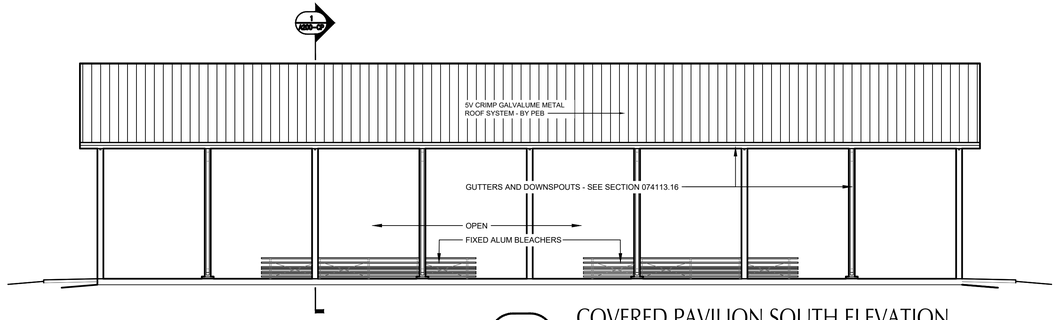

4 A200–CP COVERED PAVILION SOUTH ELEVATION


SCALE 1/8" = 1'-0"

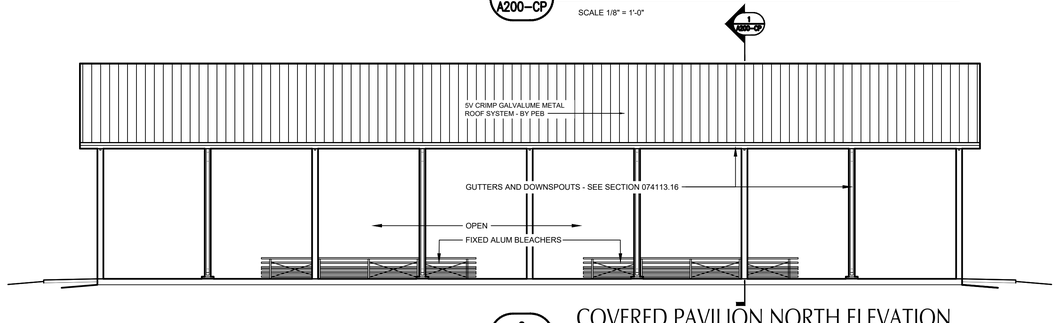

2 A200–CP COVERED PAVILION NORTH ELEVATION

SCALE 1/8" = 1'-0"

PRE-ENGINEERED BUILDING SYSTEM (PEB) NOTES:

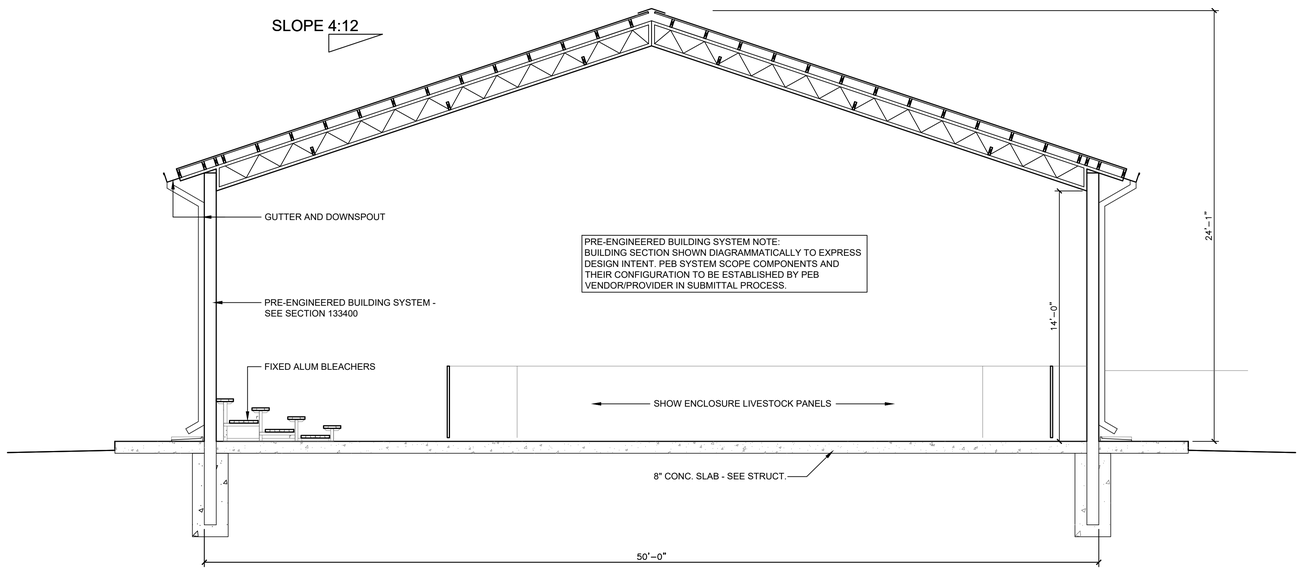

1 A200–CP COVERED PAVILION SECTION

SCALE 1/4" = 1'-0"

THE SCHOOL BOARD OF SARASOTA COUNTY

CONSTRUCTION SERVICES DEPARTMENT
phone (941) 361-6680 fax (941) 361-6684

DRAWN BY:	WJC
DATE DRAWN:	Mar. 10, 26
CHK'D BY:	SCH
BUILDING NO:	TBD
FLOOR NO:	-
S.C.S.B. PROJ. NO:	TBD
ARCH/ENG. PROJ. NO:	2217
PROJECT PHASE:	SUBMITTED:
CONCEPTUAL PHASE	OCT 20, 2021
SCHEMATIC PHASE	DEC 9, 2022
DESIGN DEV. PHASE	MAR 3, 2023
ISSUED FOR BID	-
ISSUED FOR CONST.	JUN 30, 2023
ISSUED FOR REV.	-
RECORD DRAWINGS	-

DRAWING PHASE: CONSTRUCTION DRAWINGS

NO	DATE	REVISION/DESCRIPTION:
1	-	-
2	-	-
3	-	-
4	-	-
5	-	-
6	-	-
7	-	-
8	-	-
9	-	-
10	-	-

ARCHITECT/ENGINEER FIRM INFO:
seibert architects
1373 5th Street • Sarasota, FL
34236-4915 - seibertarchitects.com
T 941.366.9161 • F 941.365.0902
Lic. AA-C000070

ARCHITECT/ENGINEER/DESIGN PROF. OF RECORD:
WILLIAM J. CRAIG, AIA AR99330

KEY PLAN:

PROJECT INFORMATION:
MCINTOSH MIDDLE SCHOOL
NEW AGRICULTURAL CENTER


651 MCINTOSH ROAD
SARASOTA FL 34240

SHEET DESCRIPTION:
COVERED PAVILION ELEVATIONS AND SECTION

DATE PRINTED: -
CAD DWG FILE: -
SHEET: 11 OF: 105

A-200-CP

These plans are protected by Federal Copyright protection. Unauthorized replication, use, or distribution may result in infringement or legal action. THIS SHEET SIZE IS 24X36 - PRINTING TO OTHER SIZES WILL NOT BE TO SCALE

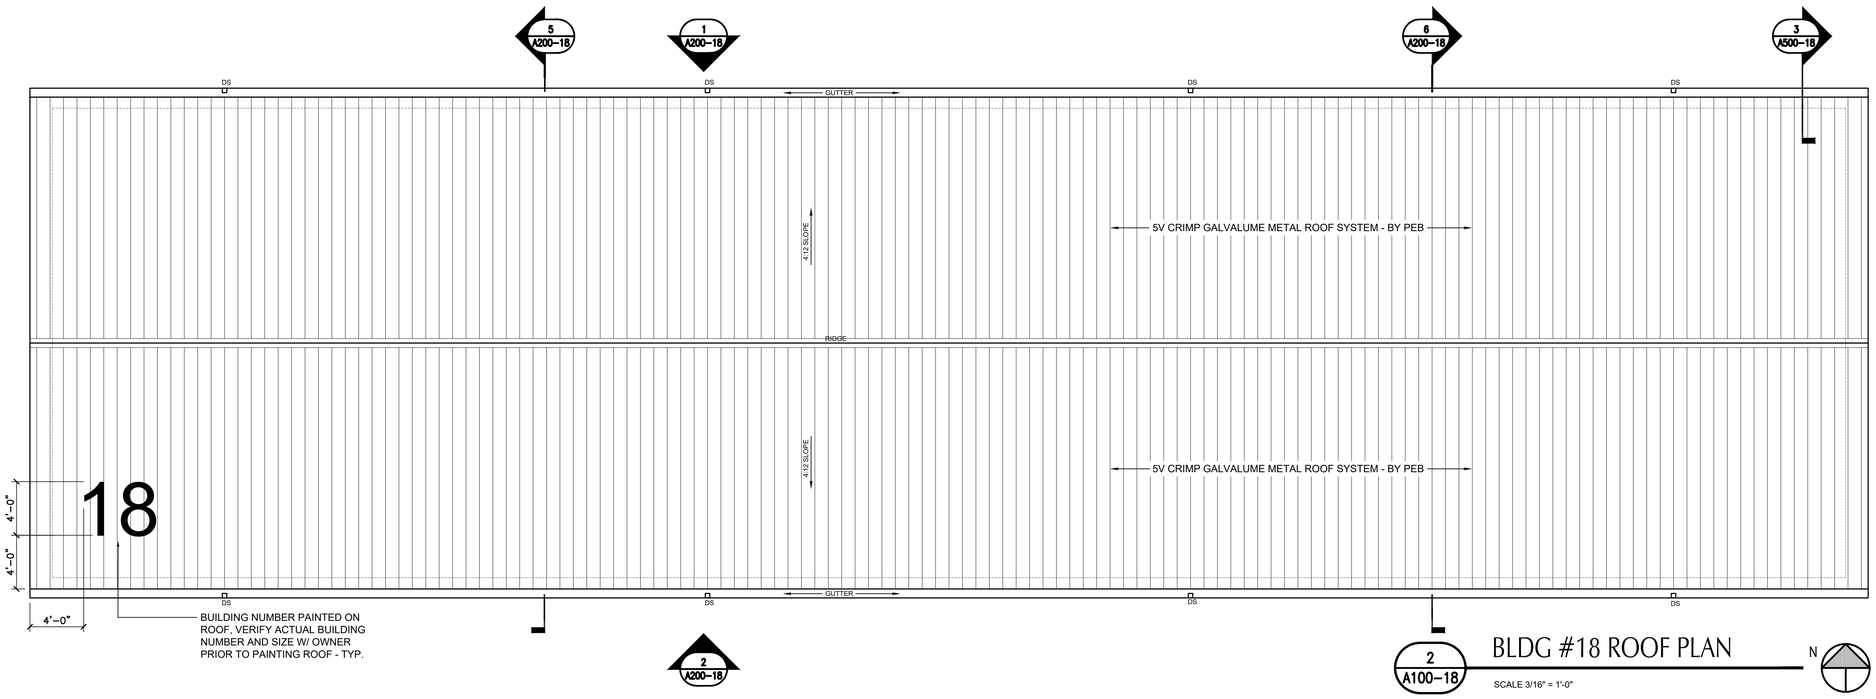

BLDG #18 ROOF PLAN

SCALE 3/16" = 1'-0"

2 A100–18


N

PRE-ENGINEERED BUILDING SYSTEM (PEB) NOTES:

1. THESE DRAWINGS ARE INTENDED TO ILLUSTRATE DESIGN INTENT ONLY AND DO NOT ILLUSTRATE ALL COMPONENTS REQUIRED FOR A COMPLETE BUILDING SYSTEM. PROVIDE AND INSTALL ALL COMPONENTS WITHIN VENDOR SCOPE REQUIRED FOR A COMPLETE BUILDING SYSTEM IN COMPLIANCE WITH THESE DRAWINGS, SPECIFICATIONS (REFER TO SECTION 13 34 00) APPLICABLE CODES AND MANUFACTURER'S RECOMMENDATIONS.
2. SEE PLANS, ELEVATIONS, SECTIONS AND DETAILS FOR LOCATION AND CONFIGURATION OF SYSTEM COLUMNS, BAR JOISTS, FRAMING, OPENINGS, CLADDING AND FINISHES AND FOR RELATIONSHIP OF PRE-ENGINEERED SYSTEM TO OTHER SYSTEMS.
3. CONTRACTOR TO SUBMIT SHOP DRAWINGS TO ARCHITECT FOR APPROVAL PRIOR TO FABRICATION. SHOP DRAWINGS TO INCLUDE CALCULATIONS CERTIFIED BY A FLORIDA LICENSED ENGINEER'S SIGNATURE AND SEAL THAT DEMONSTRATE SYSTEM'S STRUCTURAL DESIGN COMPLIES WITH WIND LOAD CRITERIA PER FBC 2020(SEVENTH EDITION); THIS INCLUDES THE DESIGN OF THE CONCRETE FOOTINGS(CONCRETE FLOOR SLABS BY OTHERS)
4. TO BE INCLUDED IN VENDOR PACKAGE:
   - FOOTING DESIGN
   - 8" X 8" NOM. PT WD COLUMNS
   - PRE-MANUFACTURED STEEL ROOF TRUSSES
   - 2X WALL FRAMING
   - 2X ROOF FRAMING
   - GALVALUME METAL WALL PANELS (26 GA)
   - GALVALUME METAL ROOF PANELS (29 GA)
   - METAL CLOSURE TRIM AT TOP, BOTTOM, AND CORNERS, RIDGE, FASCIA, ETC.
   - 3/4" PT PLYWOOD (WALL FINISH)
5. NOT INCLUDED IN VENDOR PACKAGE TO BE PROVIDED BY CONTRACTOR:
   - CONCRETE FOR FOOTINGS
   - CONCRETE FLOOR SLABS- SEE STRUCTURAL
   - INSULATION
   - DOORS - SEE DOOR SCHEDULE
   - LOUVERS - SEE MECHANICAL DWGS
   - GUTTERS AND DOWNSPOUTS
   - ROLL UP CURTAINS
   - GATES AND PANELS
   - LOCKERS
   - SHELVING
   - ELECTRICAL, TECHNOLOGY, AND LIGHTING CONDUIT, WIRING, AND EQUIPMENT - SEE ELECTRICAL DRAWINGS
   - MECHANICAL DUCTS AND EQUIPMENT- SEE MECHANICAL DWGS
   - PLUMBING FIXTURES, PIPING, AND FLOOR DRAINS - SEE PLUMBING DWGS

LOCKER NOTES:

- UNIT DIMENSIONS: 24" WIDE, 72" HEIGHT, 24" DEEP
- BASIS OF DESIGN: SALSBURY VENTED GEAR METAL LOCKER(ASSEMBLED)
- MODEL #72024BL-A
- COLOR: GRAY
- ALTERNATE: WIRECRAFTERS TA-50 MILITARY STORAGE LOCKERS, CUSTOM (ASSEMBLED)
- OPTIONS: SINGLE HINGED, ONE SHELF, THREE HOOKS, WELDED ASSEMBLY
- SBSC GUIDELINES REQUIRE THAT LOCKERS SHALL BE MOUNTED ON CONCRETE BASE 4" TO 8" HIGH WITH TWO (2) TREATED WOOD SLEEPERS.

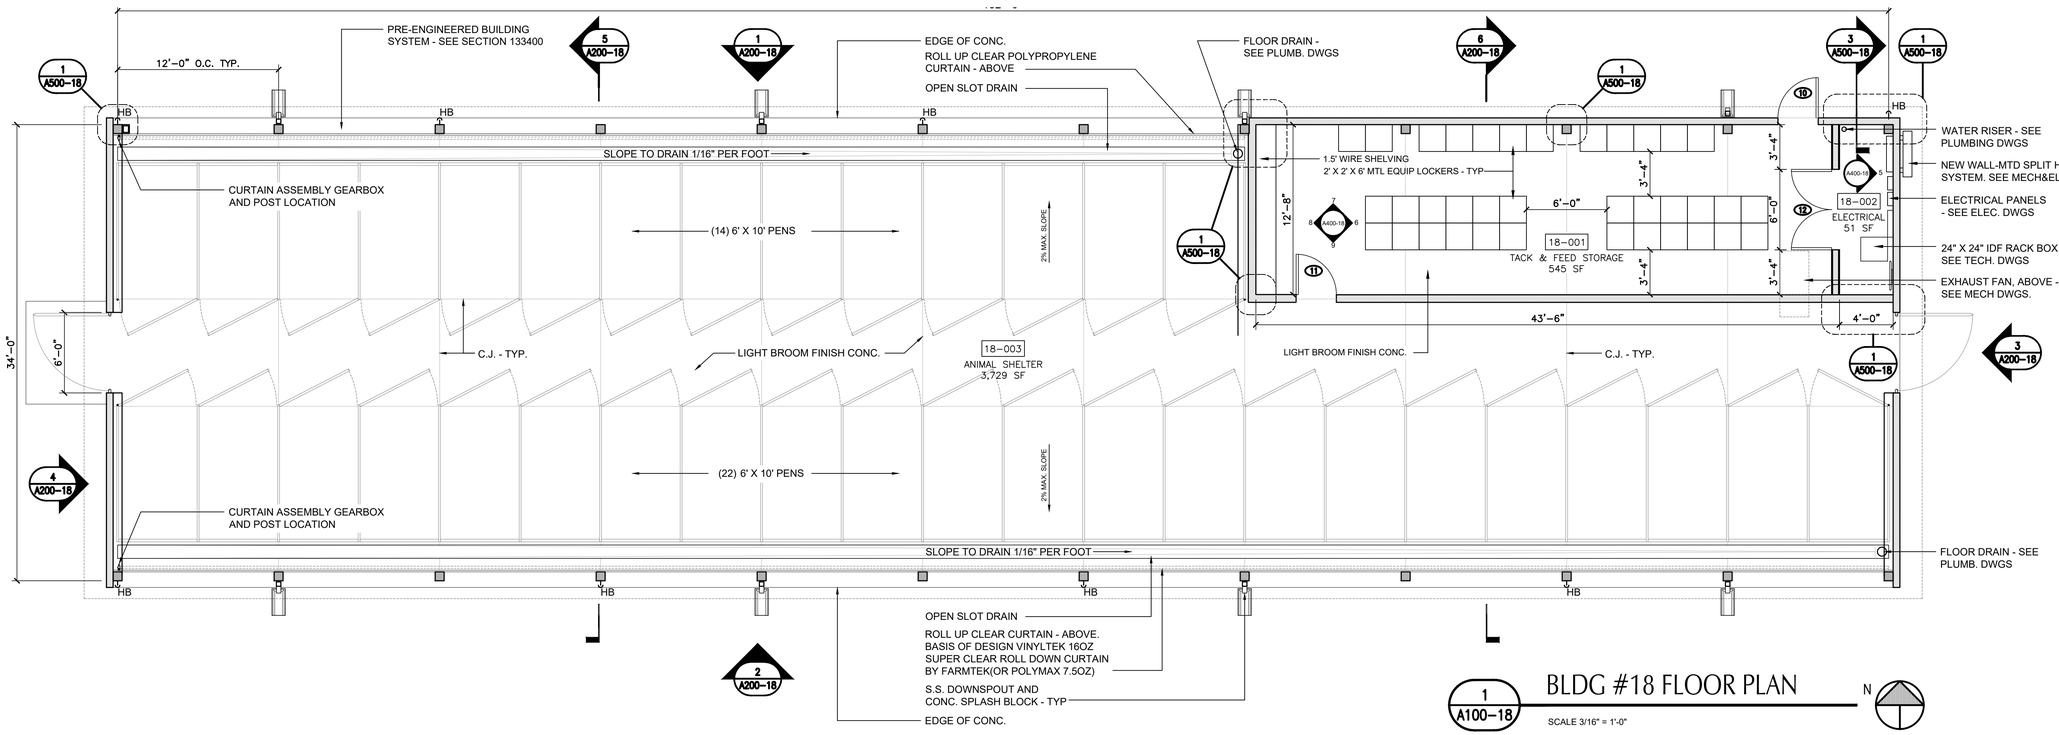

BLDG #18 FLOOR PLAN

SCALE 3/16" = 1'-0"

1 A100–18

N

THE SCHOOL BOARD OF SARASOTA COUNTY

CONSTRUCTION SERVICES DEPARTMENT
phone (941) 361-6680 fax (941) 361-6684

DRAWN BY:	WJC
DATE DRAWN:	Mar. 10, 26
CHK'D BY:	SCH
BUILDING NO:	TBD
FLOOR NO:	.
S.C.S.B. PROJ. NO:	TBD
ARCH/ENG. PROJ. NO:	2217
PROJECT PHASE:	SUBMITTED:
CONCEPTUAL PHASE	OCT 20, 2021
SCHEMATIC PHASE	DEC 9, 2022
DESIGN DEV. PHASE	MAR 3, 2023
ISSUED FOR BID	.
ISSUED FOR CONST.	JUN 30, 2023
ISSUED FOR REV.	.
RECORD DRAWINGS	.

DRAWING PHASE: CONSTRUCTION DRAWINGS

NO	DATE	REVISION/DESCRIPTION
1	-	-
2	-	-
3	-	-
4	-	-
5	-	-
6	-	-
7	-	-
8	-	-
9	-	-
10	-	-

ARCHITECT/ENGINEER FIRM INFO:
seibert architects
1373 5th Street • Sarasota, FL
34236-4915 - seibertarchitects.com
T 941.366.9161 • F 941.365.0902
Lic. AA-C000070

ARCHITECT/ENGINEER/DESIGN PROF. OF RECORD:
WILLIAM J. CRAIG, AIA AR99330

KEY PLAN:

PROJECT INFORMATION:
MCINTOSH MIDDLE SCHOOL
NEW AGRICULTURAL CENTER

651 MCINTOSH ROAD
SARASOTA FL 34240


SHEET DESCRIPTION:
BUILDING 18 FLOOR PLAN AND ROOF PLAN

DATE PRINTED: -
CAD DWG FILE: -
SHEET: 8 OF: 105

A-100-18

These plans are protected by Federal Copyright protection. Unauthorized replication, use, or distribution may result in infringement or legal action. THIS SHEET SIZE IS 24X36 - PRINTING TO OTHER SIZES WILL NOT BE TO SCALE

PRE-ENGINEERED BUILDING SYSTEM NOTE:
BUILDING SECTION SHOWN DIAGRAMMATICALLY TO EXPRESS DESIGN INTENT. PEB SYSTEM SCOPE COMPONENTS AND THEIR CONFIGURATION TO BE ESTABLISHED BY PEB VENDOR/PROVIDER IN SUBMITTAL PROCESS.

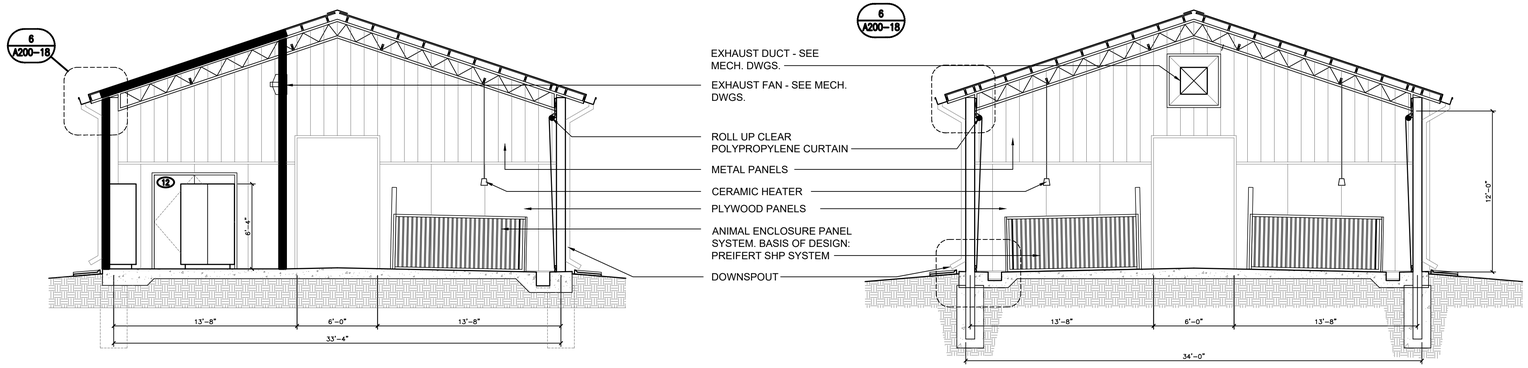


6 A200–18 BLDG #18 SECTION 3

SCALE 3/16" = 1'-0"

5 A200–18 BLDG #18 SECTION 2

SCALE 3/16" = 1'-0"

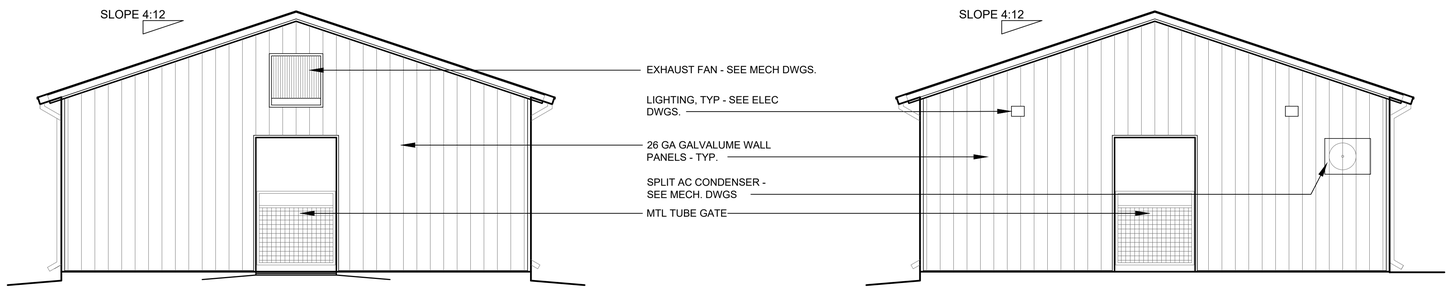


4 A200–18 BLDG #18 WEST ELEVATION

SCALE 3/16" = 1'-0"


3 A200–18 BLDG #18 EAST ELEVATION

SCALE 3/16" = 1'-0"

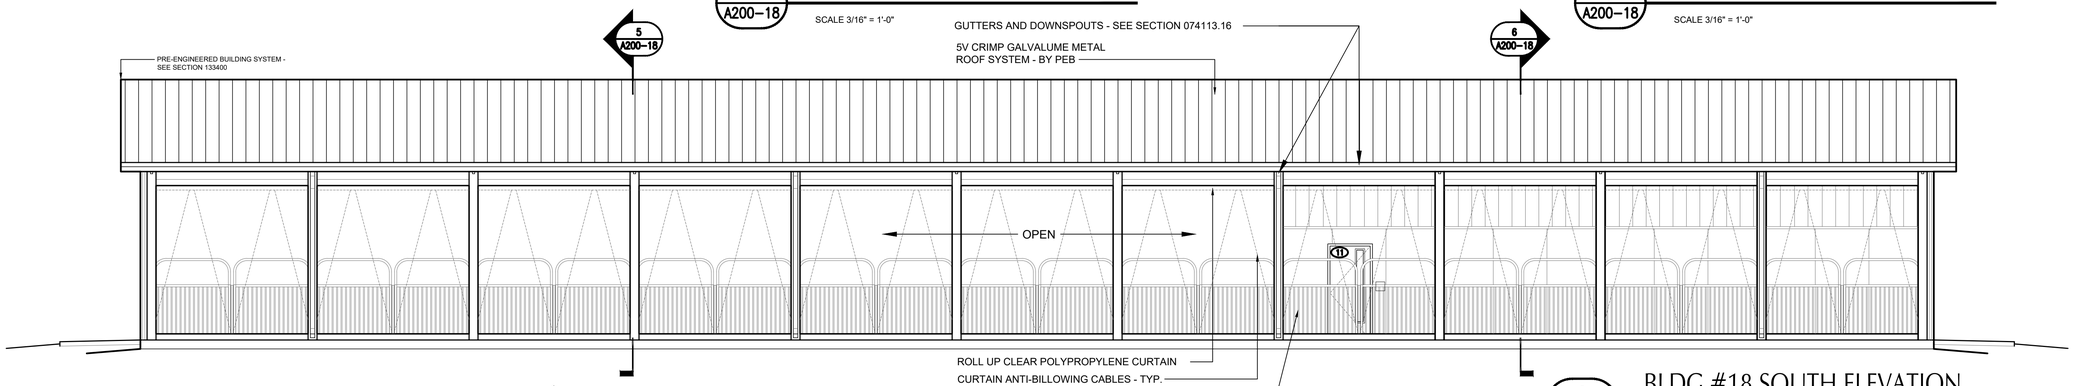

2 A200–18 BLDG #18 SOUTH ELEVATION

SCALE 3/16" = 1'-0"

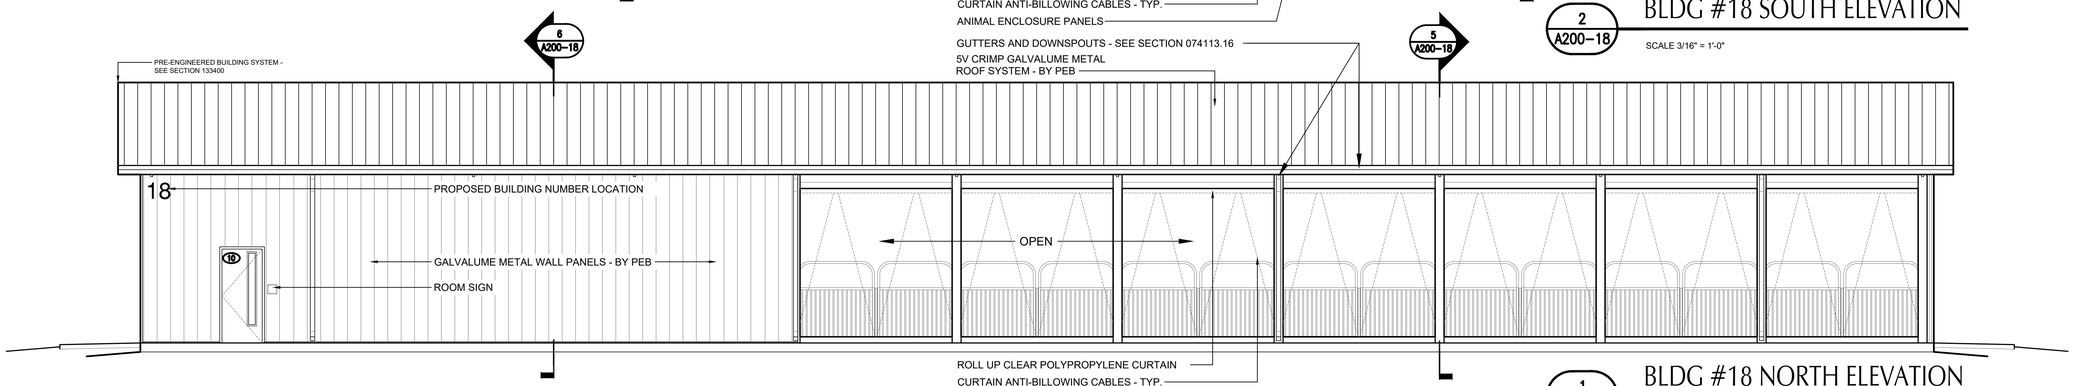

1 A200–18 BLDG #18 NORTH ELEVATION

SCALE 3/16" = 1'-0"

THE SCHOOL BOARD OF SARASOTA COUNTY

CONSTRUCTION SERVICES DEPARTMENT
phone (941) 361-6680 fax (941) 361-6684

DRAWN BY:	WJC
DATE DRAWN:	Mar. 10, 26
CHK'D BY:	SCH
BUILDING NO:	TBD
FLOOR NO:	-
S.C.S.B. PROJ. NO:	TBD
ARCH/ENG. PROJ. NO:	2217
PROJECT PHASE:	SUBMITTED:
CONCEPTUAL PHASE	OCT 20, 2021
SCHEMATIC PHASE	DEC 9, 2022
DESIGN DEV. PHASE	MAR 3, 2023
ISSUED FOR BID	-
ISSUED FOR CONST.	JUN 30, 2023
ISSUED FOR REV.	-
RECORD DRAWINGS	-

DRAWING PHASE: CONSTRUCTION DRAWINGS

NO	REVISION/DESCRIPTION:	DATE
1	-	-
2	-	-
3	-	-
4	-	-
5	-	-
6	-	-
7	-	-
8	-	-
9	-	-
10	-	-

ARCHITECT/ENGINEER FIRM INFO:
seibert architects
1373 5th Street - Sarasota, FL
34236-4915 - seibertarchitects.com
T 941.366.9161 - F 941.365.0902
Lic. AA-C000070

ARCHITECT/ENGINEER/DESIGN PROF. OF RECORD:
WILLIAM J. CRAIG, AIA AR99330

KEY PLAN:

PROJECT INFORMATION:
MCINTOSH MIDDLE SCHOOL
NEW AGRICULTURAL CENTER


651 MCINTOSH ROAD
SARASOTA FL 34240

SHEET DESCRIPTION:
BLDG 18 (AS2)
ELEVATIONS

DATE PRINTED: -
CAD DWG FILE: -
SHEET: 12 OF: 105


A-200-18

These plans are protected by Federal Copyright protection. Unauthorized replication, use, or distribution may result in infringement or legal action. THIS SHEET SIZE IS 24X36 - PRINTING TO OTHER SIZES WILL NOT BE TO SCALE

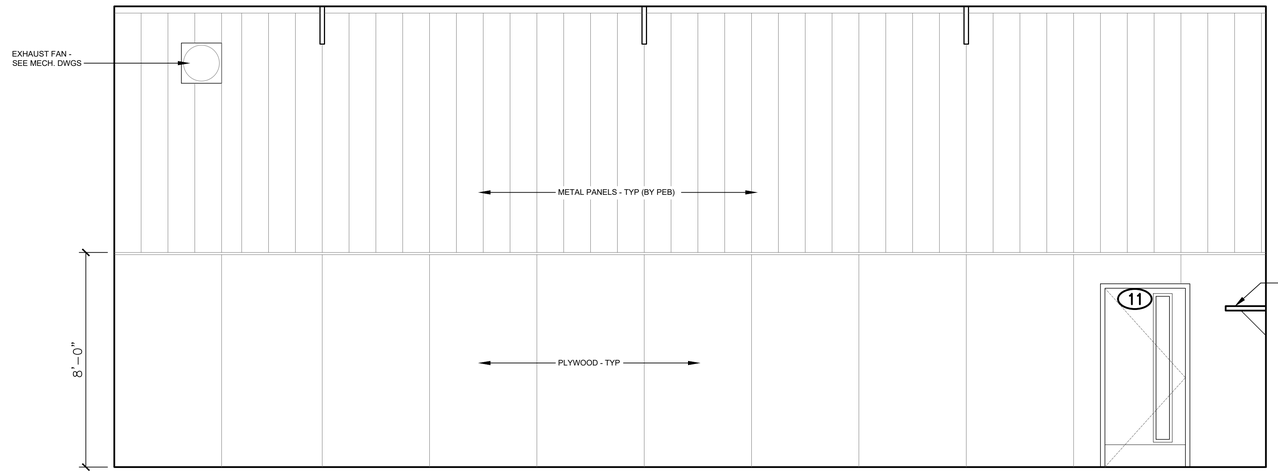


9 A400-18 INTERIOR ELEVATION

SCALE 3/8" = 1'-0" 0 1' 2' 4'

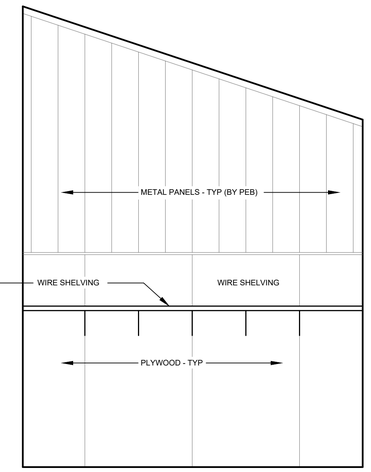


8 A400-18 INTERIOR ELEVATION

SCALE 3/8" = 1'-0" 0 1' 2' 4'

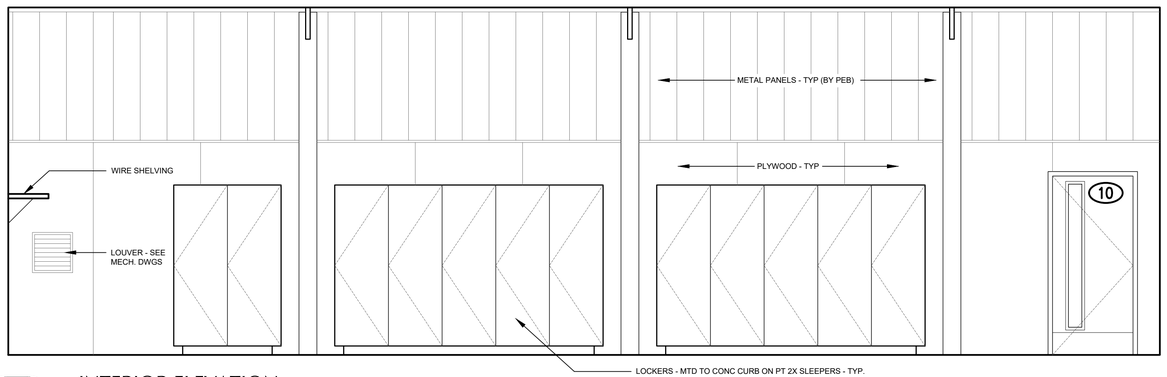


7 A400-18 INTERIOR ELEVATION

SCALE 3/8" = 1'-0" 0 1' 2' 4'

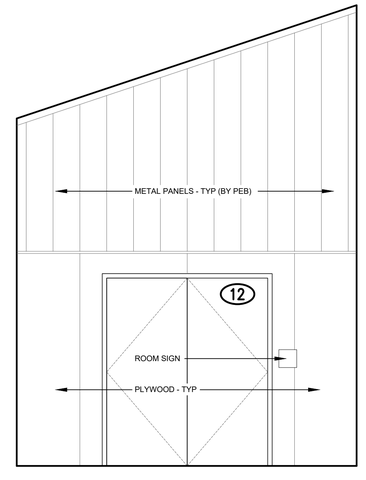


6 A400-18 INTERIOR ELEVATION

SCALE 3/8" = 1'-0" 0 1' 2' 4'

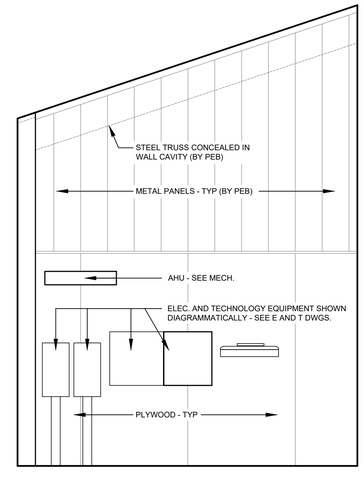


5 A400-18 INTERIOR ELEVATION

SCALE 3/8" = 1'-0" 0 1' 2' 4'

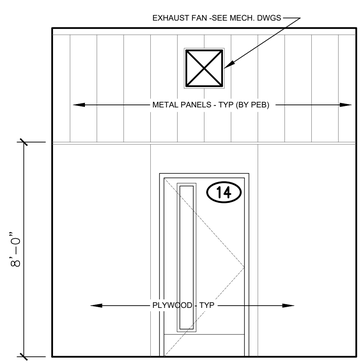


4 A400-18 INTERIOR ELEVATION

SCALE 3/8" = 1'-0" 0 1' 2' 4'

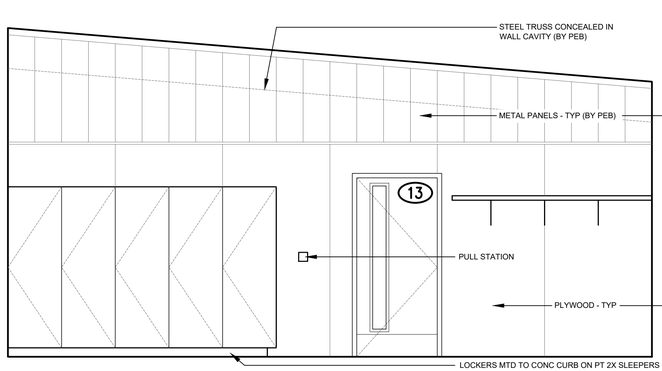


3 A400-18 INTERIOR ELEVATION

SCALE 3/8" = 1'-0" 0 1' 2' 4'

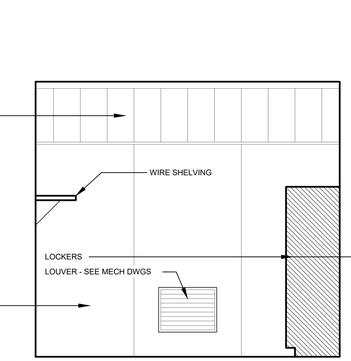

2 A400-18 INTERIOR ELEVATION

SCALE 3/8" = 1'-0" 0 1' 2' 4'

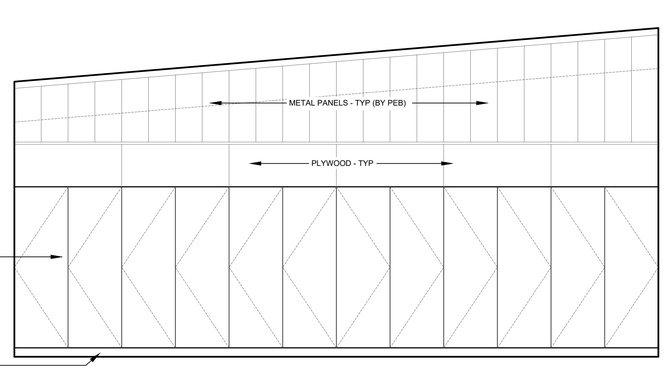

1 A400-18 INTERIOR ELEVATION

SCALE 3/8" = 1'-0" 0 1' 2' 4'

THE SCHOOL BOARD OF SARASOTA COUNTY

CONSTRUCTION SERVICES DEPARTMENT
phone (941) 361-6680 fax (941) 361-6684

DRAWN BY:	WJC
DATE DRAWN:	Mar. 10, 26
CHK'D BY:	SCH
BUILDING NO:	TBD
FLOOR NO:	-
S.C.S.B. PROJ. NO:	TBD
ARCH/ENG. PROJ. NO:	2217
PROJECT PHASE:	SUBMITTED:
CONCEPTUAL PHASE	OCT 20, 2021
SCHEMATIC PHASE	DEC 9, 2022
DESIGN DEV. PHASE	MAR 3, 2023
ISSUED FOR BID	-
ISSUED FOR CONST.	JUN 30, 2023
ISSUED FOR REV.	-
RECORD DRAWINGS	-

DRAWING PHASE: CONSTRUCTION DRAWINGS

NO	DATE	REVISION/DESCRIPTION:
1	-	-
2	-	-
3	-	-
4	-	-
5	-	-
6	-	-
7	-	-
8	-	-
9	-	-
10	-	-

ARCHITECT/ENGINEER FIRM INFO:
seibert architects
1373 5th Street - Sarasota, FL
34236-4915 - seibertarchitects.com
T 941.366.9161 - F 941.365.0902
Lic. AA-C000070

ARCHITECT/ENGINEER/DESIGN PROF. OF RECORD:
WILLIAM J. CRAIG, AIA AR99330

KEY PLAN:

PROJECT INFORMATION:
MCINTOSH MIDDLE SCHOOL
NEW AGRICULTURAL CENTER


651 MCINTOSH ROAD
SARASOTA FL 34240

SHEET DESCRIPTION:
BLDG 18 & 19
INTERIOR ELEVATIONS

DATE PRINTED: -
CAD DWG FILE: -
SHEET: 13 OF: 105

A-400-18

These plans are protected by Federal Copyright protection. Unauthorized replication, use, or distribution may result in infringement or legal action. THIS SHEET SIZE IS 24X36 - PRINTING TO OTHER SIZES WILL NOT BE TO SCALE

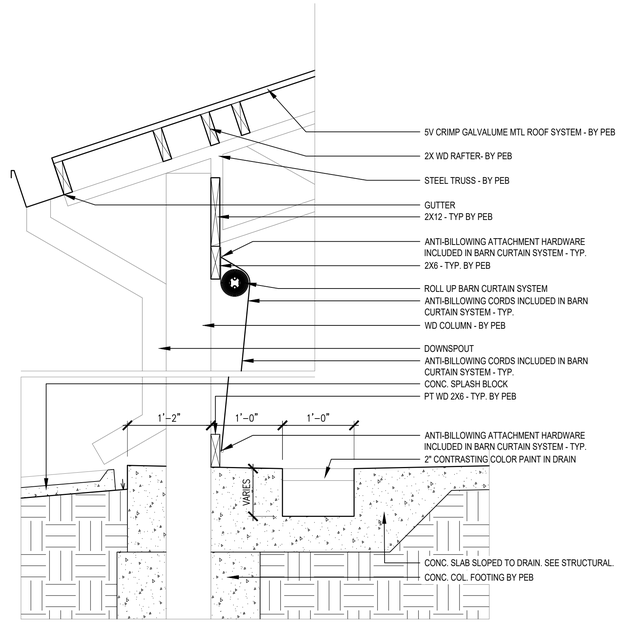


1
A500-18

WALL DETAIL @ SLAB TRENCH

SCALE 1" = 1'-0"

0 3" 6" 1' 2'

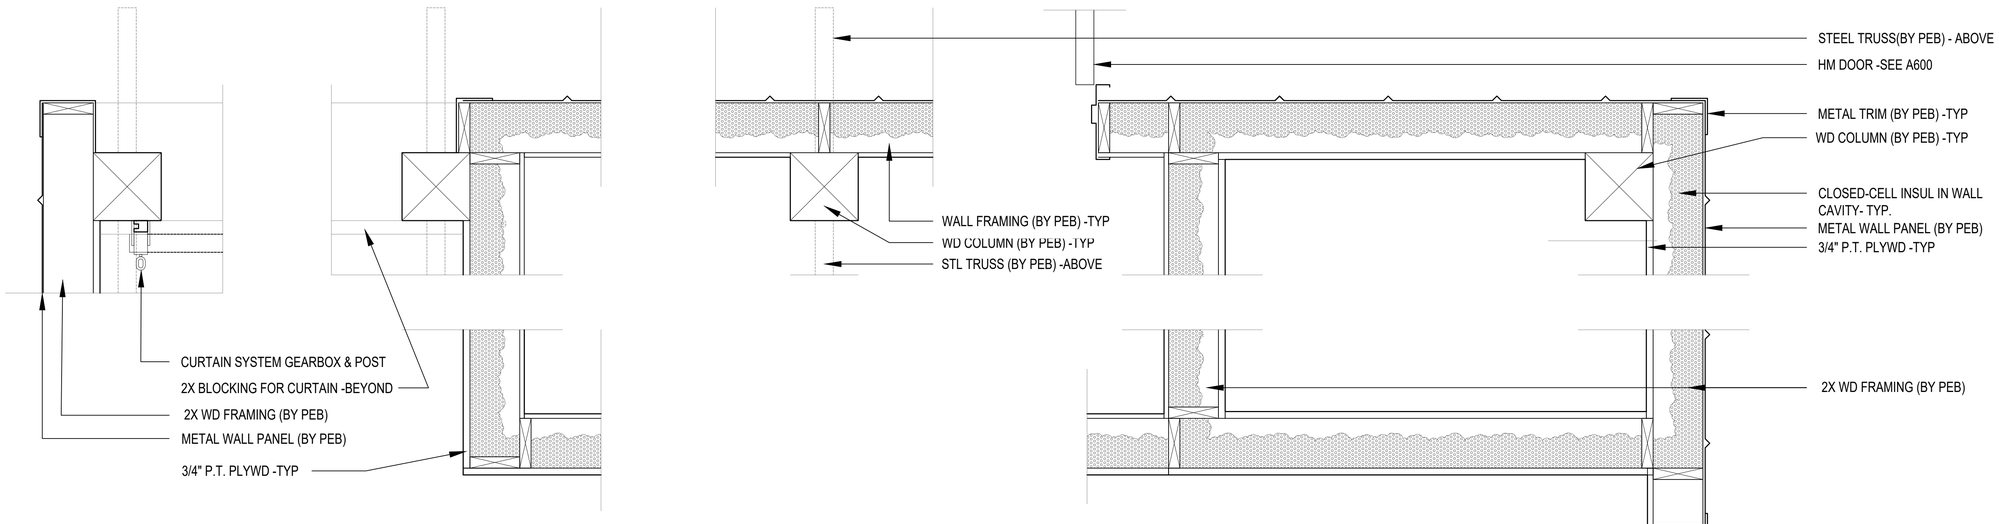

2
A500-18

BLDG #18 PLAN DETAILS

SCALE 1" = 1'-0"

0 3" 6" 1' 2'

THE SCHOOL BOARD OF SARASOTA COUNTY

CONSTRUCTION SERVICES DEPARTMENT
phone (941) 361-6680 fax (941) 361-6684

DRAWN BY:	WJC
DATE DRAWN:	Mar. 10, 26
CHK'D BY:	SCH
BUILDING NO:	TBD
FLOOR NO:	-
S.C.S.B. PROJ. NO:	TBD
ARCH/ENG. PROJ. NO:	2217
PROJECT PHASE:	SUBMITTED:
CONCEPTUAL PHASE	OCT 20, 2021
SCHEMATIC PHASE	DEC 9, 2022
DESIGN DEV. PHASE	MAR 3, 2023
ISSUED FOR BID	-
ISSUED FOR CONST.	JUN 30, 2023
ISSUED FOR REV.	-
RECORD DRAWINGS	-

DRAWING PHASE: CONSTRUCTION DRAWINGS

NO	DATE	REVISION/DESCRIPTION
1	-	-
2	-	-
3	-	-
4	-	-
5	-	-
6	-	-
7	-	-
8	-	-
9	-	-
10	-	-

ARCHITECT/ENGINEER FIRM INFO:
seibert architects
1373 5th Street · Sarasota, FL 34236-4915 - seibertarchitects.com
T 941.366.9161 · F 941.365.0902
Lic. AA-C000070

ARCHITECT/ENGINEER/DESIGN PROF. OF RECORD:
WILLIAM J. CRAIG, AIA AR99330

KEY PLAN:

PROJECT INFORMATION:
MCINTOSH MIDDLE SCHOOL
NEW AGRICULTURAL CENTER

651 MCINTOSH ROAD
SARASOTA FL 34240

SHEET DESCRIPTION:
BUILDING 18
DETAILS

DATE PRINTED: -
CAD DWG FILE: -
SHEET: 4 OF: 105

A-500-18

These plans are protected by Federal Copyright protection. Unauthorized replication, use, or distribution may result in infringement or legal action. THIS SHEET SIZE IS 24X36 - PRINTING TO OTHER SIZES WILL NOT BE TO SCALE