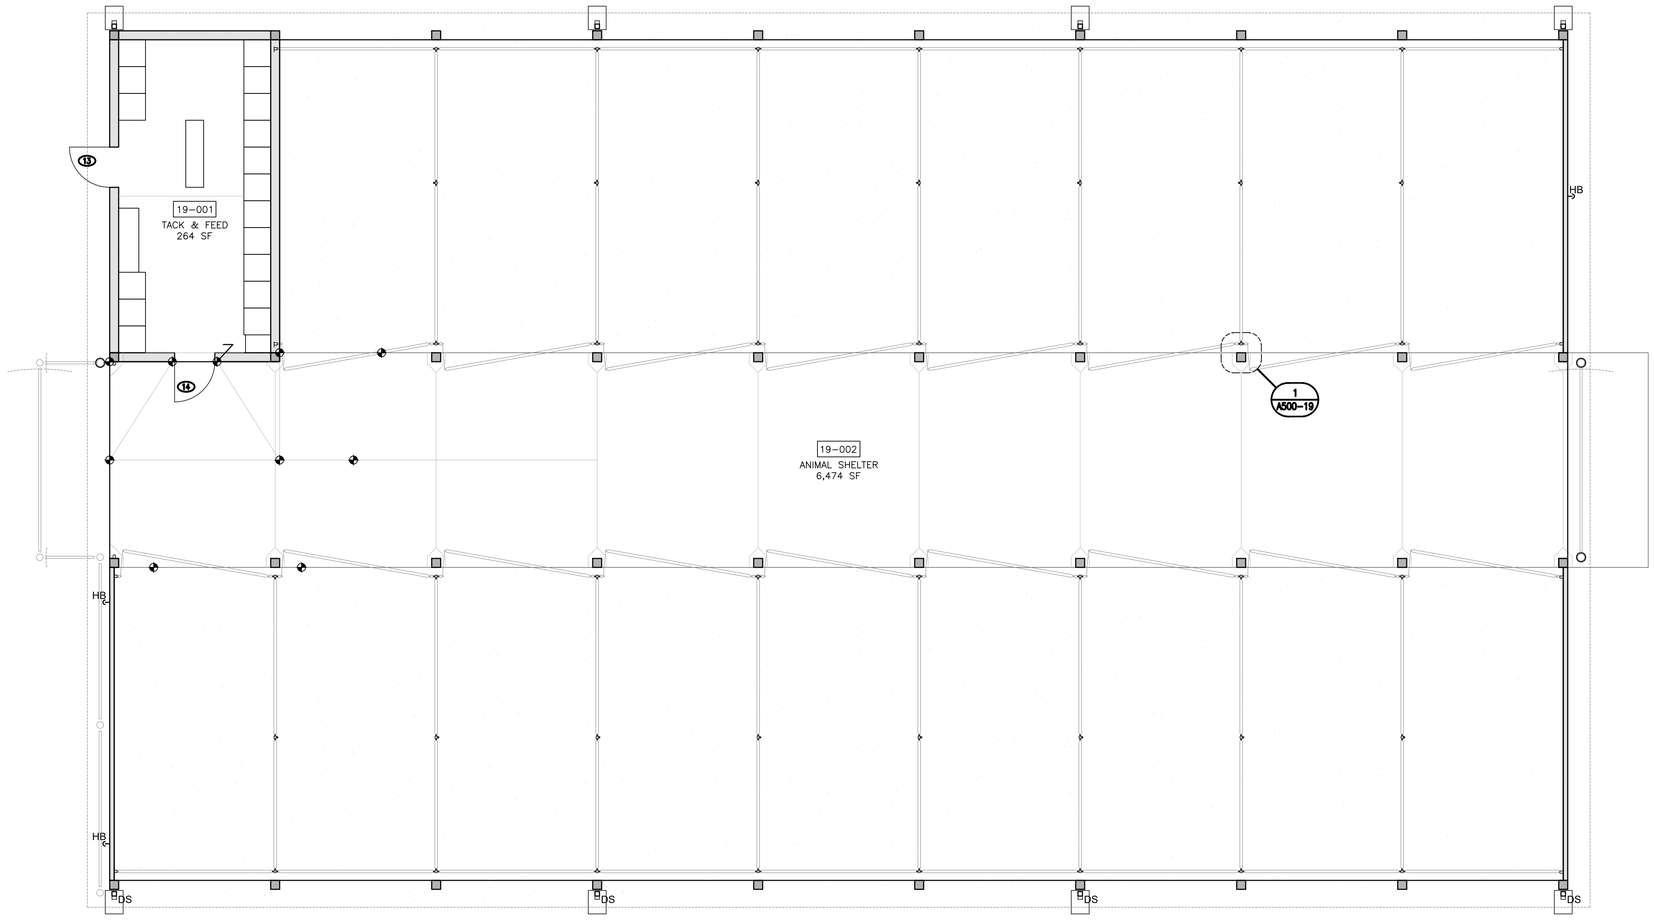


1 / A100-19 BUILDING #19 FLOOR PLAN

SCALE 3/16" = 1'-0"

N

THE SCHOOL BOARD OF SARASOTA COUNTY

CONSTRUCTION SERVICES DEPARTMENT
phone (941) 361-6680 fax (941) 361-6684

DRAWN BY:	WJC
DATE DRAWN:	Oct. 2, 26
CHK'D BY:	SCH
BUILDING NO:	TBD
FLOOR NO:	-
S.C.S.B. PROJ. NO:	TBD
ARCH/ENG. PROJ. NO:	2217
PROJECT PHASE:	SUBMITTED:
CONCEPTUAL PHASE	OCT 20, 2021
SCHEMATIC PHASE	DEC 9, 2022
DESIGN DEV. PHASE	MAR 3, 2023
ISSUED FOR BID	-
ISSUED FOR CONST.	JUN 30, 2023
ISSUED FOR REV.	-
RECORD DRAWINGS	SEPT 24, 2025

DRAWING PHASE: RECORD DRAWINGS-DRAFT

NO	DATE	REVISION/DESCRIPTION:
1	-	-
2	-	-
3	-	-
4	-	-
5	-	-
6	-	-
7	-	-
8	-	-
9	-	-
10	-	-

ARCHITECT/ENGINEER FIRM INFO:
seibert architects
1373 5th Street · Sarasota, FL
34236-4915 - seibertarchitects.com
T 941.366.9161 · F 941.365.0902
Lic. AA-C000070

ARCHITECT/ENGINEER/DESIGN PROF. OF RECORD:
WILLIAM J. CRAIG, AIA AR99330

KEY PLAN:

PROJECT INFORMATION:
MCINTOSH MIDDLE SCHOOL
NEW AGRICULTURAL CENTER

651 MCINTOSH ROAD
SARASOTA FL 34240


SHEET DESCRIPTION:
BLDG 19
FISH FLOOR PLAN

DATE PRINTED: -
CAD DWG FILE: -
SHEET: 9 OF: 105

A-100-19


These plans are protected by Federal Copyright protection. Unauthorized replication, use, or distribution may result in infringement or legal action. THIS SHEET SIZE IS 24X36 - PRINTING TO OTHER SIZES WILL NOT BE TO SCALE


PRE-ENGINEERED BUILDING SYSTEM NOTE:
BUILDING SECTION SHOWN DIAGRAMMATICALLY TO EXPRESS DESIGN INTENT. PEB SYSTEM SCOPE COMPONENTS AND THEIR CONFIGURATION TO BE ESTABLISHED BY PEB VENDOR/PROVIDER IN SUBMITTAL PROCESS.

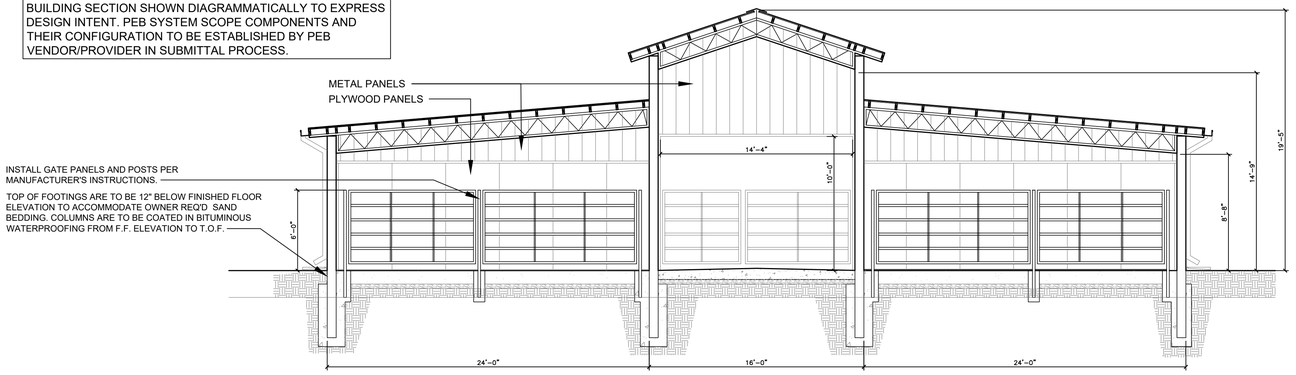

2 / A100-19 BLDG #19 SECTION

SCALE 3/16" = 1'-0"

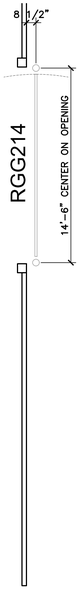

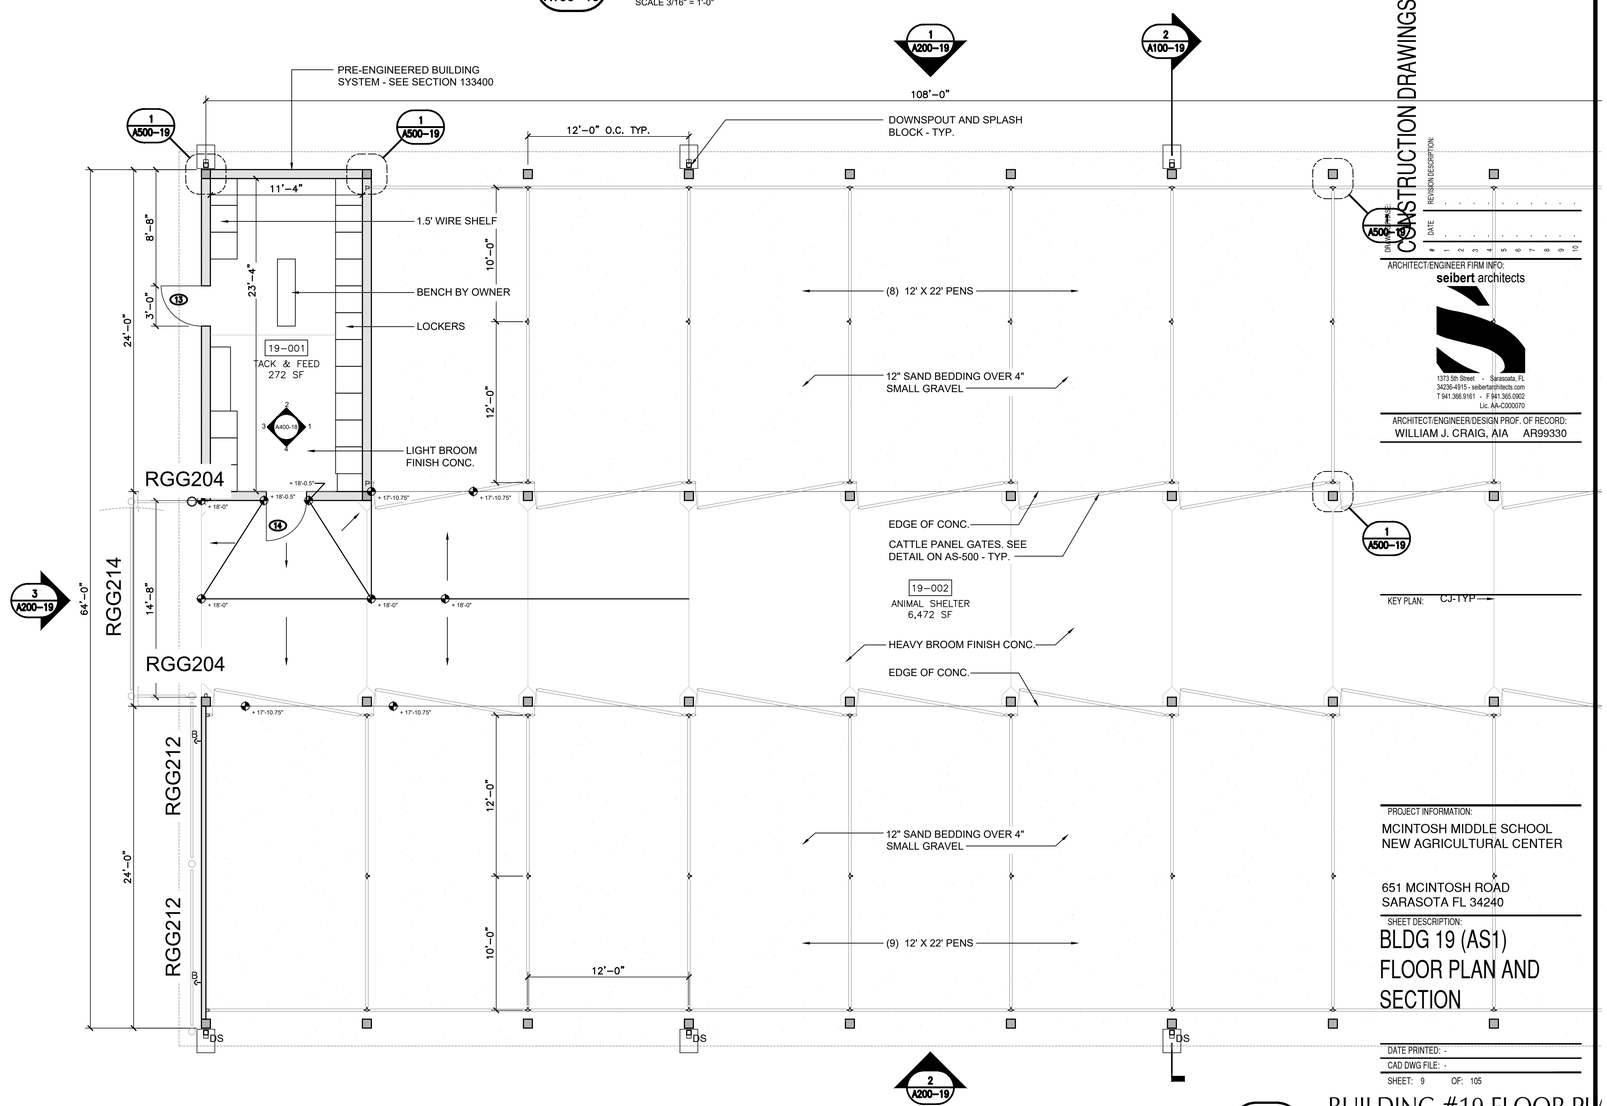

THE SCHOOL BOARD OF SARASOTA COUNTY

CONSTRUCTION SERVICES DEPARTMENT
phone (941) 361-6680 fax (941) 361-6684

DRAWN BY:	WJC
DATE DRAWN:	Mar. 10, 26
CHK'D BY:	SCH
BUILDING NO:	TBD
FLOOR NO:	-
S.C.S.B. PROJ. NO:	TBD
ARCH/ENG. PROJ. NO:	2217
PROJECT PHASE:	SUBMITTED:
CONCEPTUAL PHASE	OCT 20, 2021
SCHEMATIC PHASE	DEC 9, 2022
DESIGN DEV. PHASE	MAR 3, 2023
ISSUED FOR BID	-
ISSUED FOR CONST.	JUN 30, 2023
ISSUED FOR REV.	-
RECORD DRAWINGS	-

CONSTRUCTION DRAWINGS

REVISION/DESCRIPTION:	DATE

ARCHITECT/ENGINEER FIRM INFO:
seibert architects
1373 5th Street • Sarasota, FL
34236-4915 - seibertarchitects.com
T 941.366.9161 • F 941.365.0902
Lic. AA-C000070

ARCHITECT/ENGINEER/DESIGN PROF. OF RECORD:
WILLIAM J. CRAIG, AIA AR99330

KEY PLAN: CJ-TYP

PROJECT INFORMATION:
MCINTOSH MIDDLE SCHOOL
NEW AGRICULTURAL CENTER

651 MCINTOSH ROAD
SARASOTA FL 34240

SHEET DESCRIPTION:
BLDG 19 (AS1)
FLOOR PLAN AND SECTION

DATE PRINTED: -
CAD DWG FILE: -
SHEET: 9 OF: 105


1 / A100-19 BUILDING #19 FLOOR PL

SCALE 3/16" = 1'-0"

A-100-19

These plans are protected by Federal Copyright protection. Unauthorized replication, use, or distribution may result in infringement or legal action.

THIS SHEET SIZE IS 24X36 - PRINTING TO OTHER SIZES WILL NOT BE TO SCALE

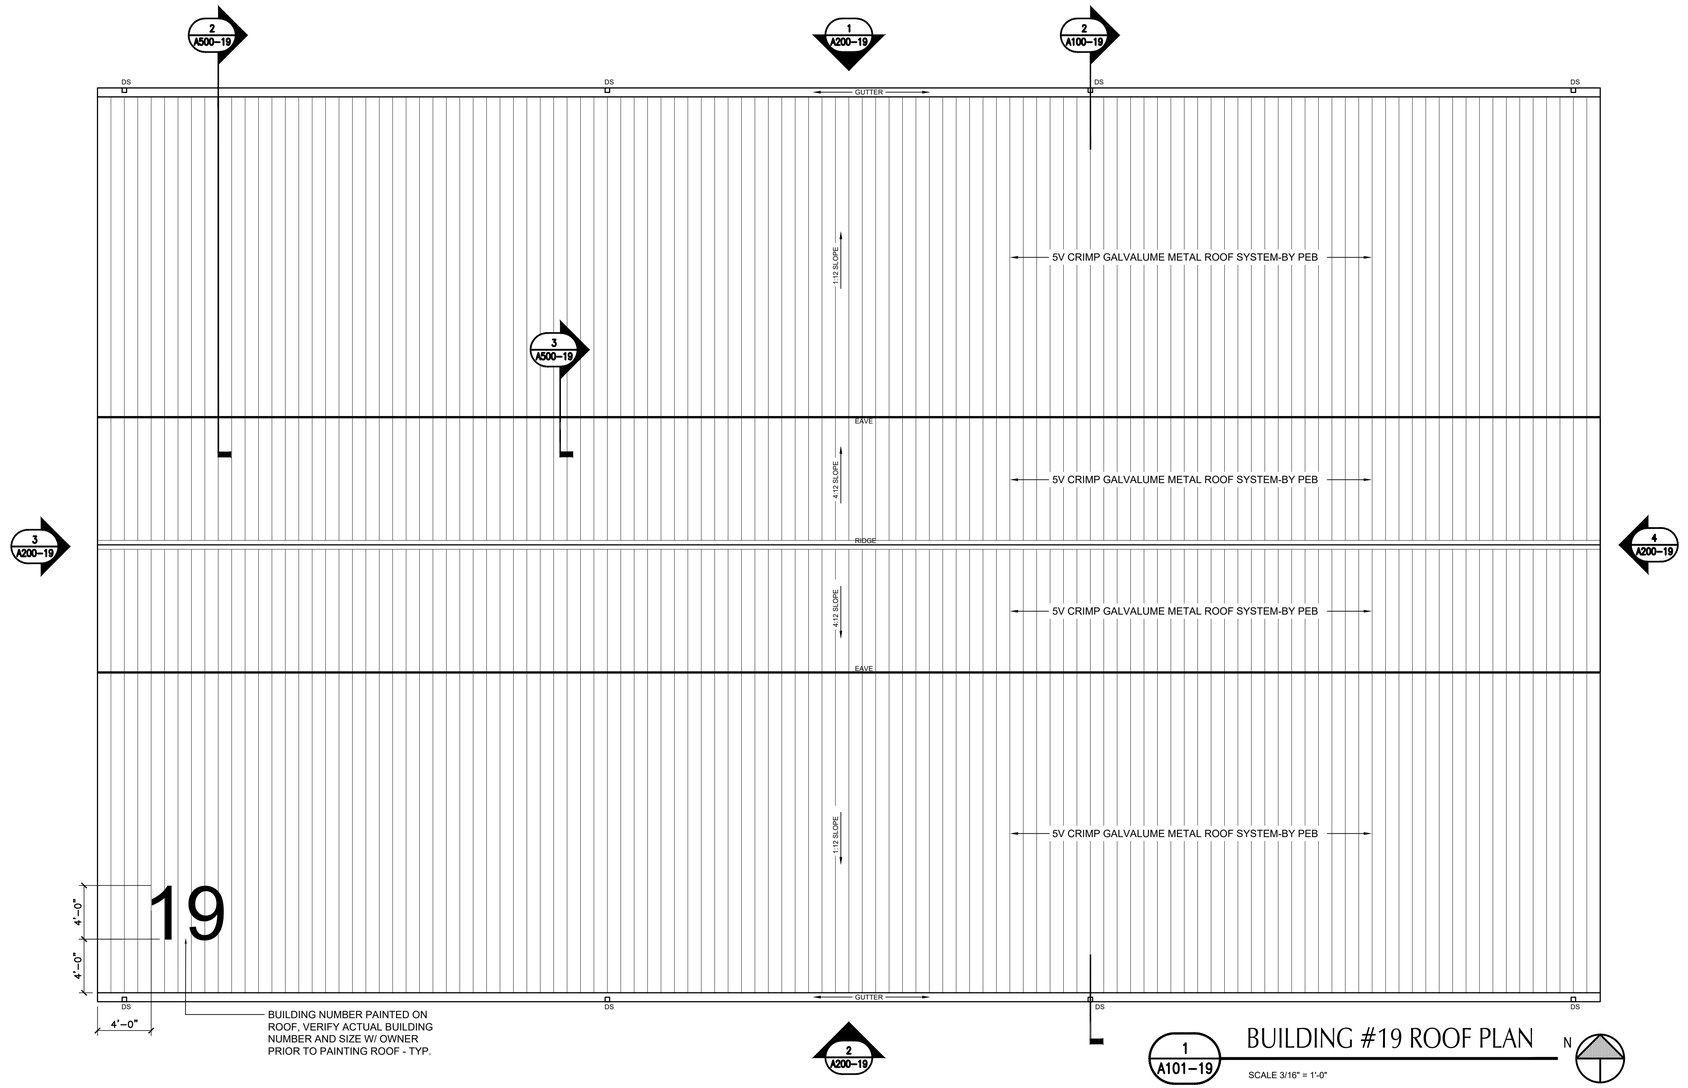

1 BUILDING #19 ROOF PLAN

1 A101–19

SCALE 3/16" = 1'-0"

N

THE SCHOOL BOARD OF SARASOTA COUNTY

CONSTRUCTION SERVICES DEPARTMENT
phone (941) 361-6680 fax (941) 361-6684

DRAWN BY:	WJC
DATE DRAWN:	Mar. 10, 26
CHK'D BY:	SCH
BUILDING NO:	TBD
FLOOR NO:	.
S.C.S.B. PROJ. NO:	TBD
ARCH/ENG. PROJ. NO:	2217
PROJECT PHASE:	SUBMITTED:
CONCEPTUAL PHASE	OCT 20, 2021
SCHEMATIC PHASE	DEC 9, 2022
DESIGN DEV. PHASE	MAR 3, 2023
ISSUED FOR BID	.
ISSUED FOR CONST.	JUN 30, 2023
ISSUED FOR REV.	.
RECORD DRAWINGS	.

DRAWING PHASE: CONSTRUCTION DRAWINGS

NO	DATE	REVISION/DESCRIPTION
1	.	.
2	.	.
3	.	.
4	.	.
5	.	.
6	.	.
7	.	.
8	.	.
9	.	.
10	.	.

ARCHITECT/ENGINEER FIRM INFO:
seibert architects
1373 5th Street - Sarasota, FL
34236-4915 - seibertarchitects.com
T 941.366.9161 - F 941.365.0902
Lic. AA-C000070

ARCHITECT/ENGINEER/DESIGN PROF. OF RECORD:
WILLIAM J. CRAIG, AIA AR99330

KEY PLAN:

PROJECT INFORMATION:
MCINTOSH MIDDLE SCHOOL
NEW AGRICULTURAL CENTER


651 MCINTOSH ROAD
SARASOTA FL 34240

SHEET DESCRIPTION:
BLDG 19 (AS1)
FLOOR PLAN AND
SECTION

DATE PRINTED: -
CAD DWG FILE: -
SHEET: 9 OF: 105


A-101-19

These plans are protected by Federal Copyright protection. Unauthorized replication, use, or distribution may result in infringement or legal action. THIS SHEET SIZE IS 24X36 - PRINTING TO OTHER SIZES WILL NOT BE TO SCALE

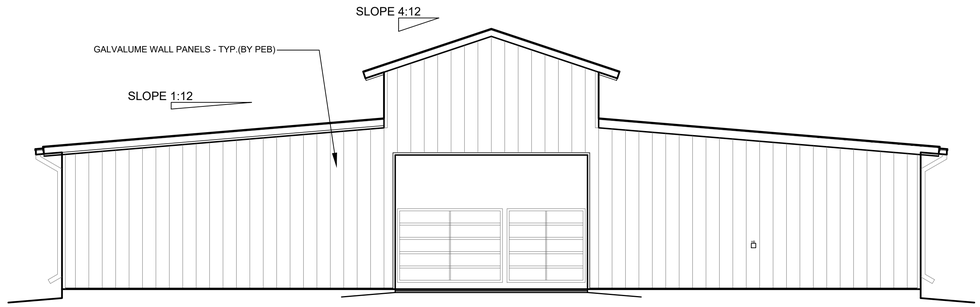


4 A200–19 BLDG #19 WEST ELEVATION

SCALE 3/16" = 1'-0"

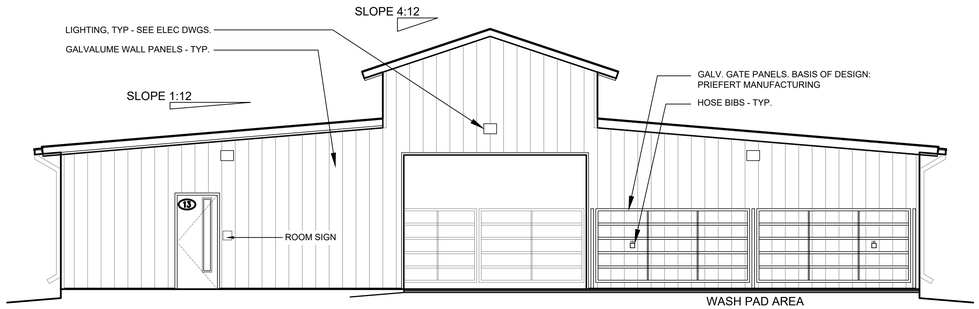


3 A200–19 BLDG #19 EAST ELEVATION

SCALE 3/16" = 1'-0"

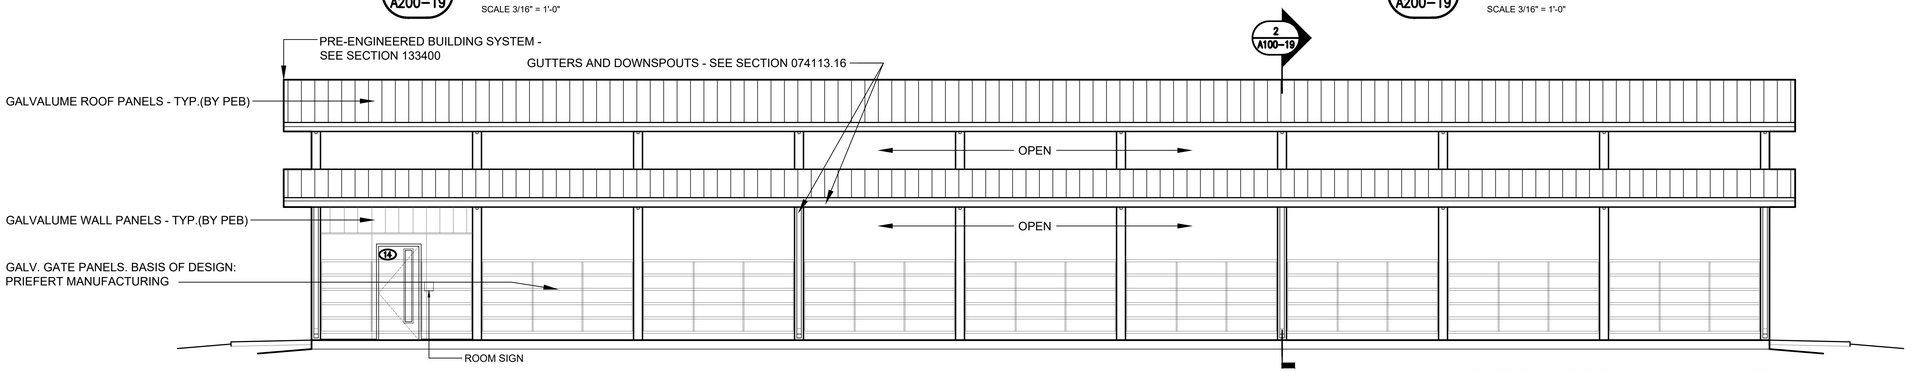

2 A200–19 BLDG #19 SOUTH ELEVATION

SCALE 3/16" = 1'-0"

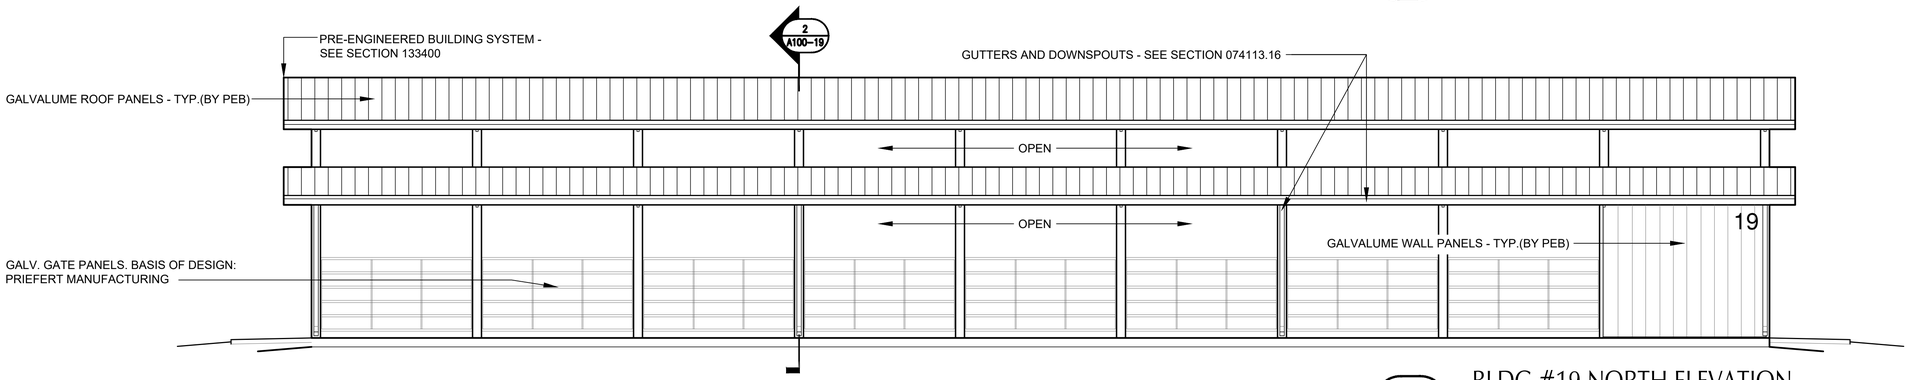

1 A200–19 BLDG #19 NORTH ELEVATION

SCALE 3/16" = 1'-0"

These plans are protected by Federal Copyright protection. Unauthorized replication, use, or distribution may result in infringement or legal action. THIS SHEET SIZE IS 24X36 - PRINTING TO OTHER SIZES WILL NOT BE TO SCALE

THE SCHOOL BOARD OF SARASOTA COUNTY

CONSTRUCTION SERVICES DEPARTMENT
phone (941) 361-6680 fax (941) 361-6684

DRAWN BY:	WJC
DATE DRAWN:	Mar. 10, 26
CHK'D BY:	SCH
BUILDING NO:	TBD
FLOOR NO:	-
S.C.S.B. PROJ. NO:	TBD
ARCH/ENG. PROJ. NO:	2217
PROJECT PHASE:	SUBMITTED:
CONCEPTUAL PHASE	OCT 20, 2021
SCHEMATIC PHASE	DEC 9, 2022
DESIGN DEV. PHASE	MAR 3, 2023
ISSUED FOR BID	-
ISSUED FOR CONST.	JUN 30, 2023
ISSUED FOR REV.	-
RECORD DRAWINGS	-

DRAWING PHASE: CONSTRUCTION DRAWINGS

NO	REVISION/DESCRIPTION:	DATE
1	-	-
2	-	-
3	-	-
4	-	-
5	-	-
6	-	-
7	-	-
8	-	-
9	-	-
10	-	-

ARCHITECT/ENGINEER FIRM INFO:
seibert architects

1373 5th Street · Sarasota, FL
34236-4915 - seibertarchitects.com
T 941.366.9161 · F 941.365.0902
Lic. AA-C000070

ARCHITECT/ENGINEER/DESIGN PROF. OF RECORD:
WILLIAM J. CRAIG, AIA AR99330

KEY PLAN:


PROJECT INFORMATION:
MCINTOSH MIDDLE SCHOOL
NEW AGRICULTURAL CENTER

651 MCINTOSH ROAD
SARASOTA FL 34240

SHEET DESCRIPTION:
BLDG 19 (AS1) ELEVATIONS AND SECTIONS


DATE PRINTED: -
CAD DWG FILE: -
SHEET: 13 OF: 105

A-200-19

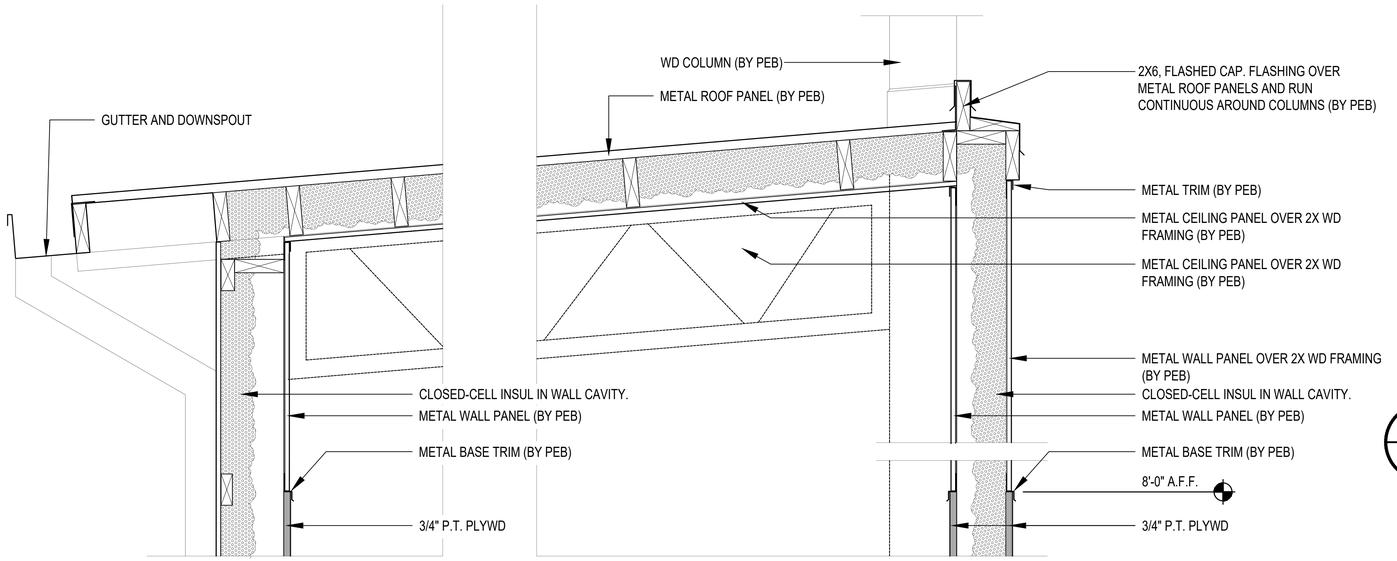


2 / A500–19 DETAIL @ TACK&FEED CEILING

SCALE 1" = 1'–0" 0 3" 6" 1' 2'

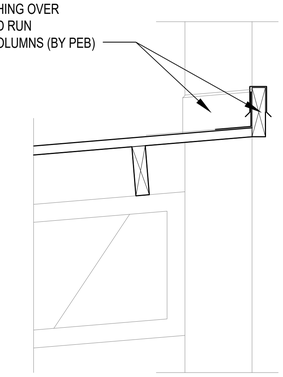

3 / A500–19 ROOF FLASHING DETAIL

SCALE 1" = 1'–0" 0 3" 6" 1' 2'

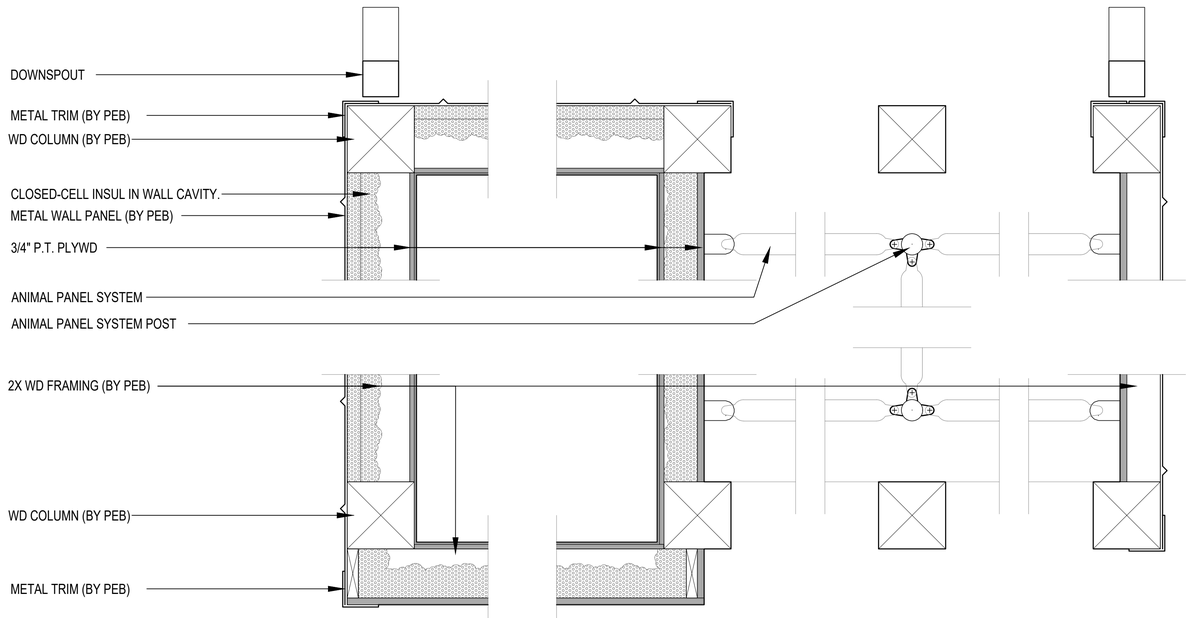

1 / A500–19 BUILDING #19 PLAN DETAILS

SCALE 1" = 1'–0" 0 3" 6" 1' 2'

THE SCHOOL BOARD OF SARASOTA COUNTY

CONSTRUCTION SERVICES DEPARTMENT
phone (941) 361-6680 fax (941) 361-6684

DRAWN BY:	WJC
DATE DRAWN:	Mar. 10, 26
CHK'D BY:	SCH
BUILDING NO:	TBD
FLOOR NO:	-
S.C.S.B. PROJ. NO:	TBD
ARCH/ENG. PROJ. NO:	2217
PROJECT PHASE:	SUBMITTED:
CONCEPTUAL PHASE	OCT 20, 2021
SCHEMATIC PHASE	DEC 9, 2022
DESIGN DEV. PHASE	MAR 3, 2023
ISSUED FOR BID	-
ISSUED FOR CONST.	JUN 30, 2023
ISSUED FOR REV.	-
RECORD DRAWINGS	-

RGG214 F

DRAWING PHASE: CONSTRUCTION DRAWINGS

NO	DATE	REVISION/DESCRIPTION:
1	-	-
2	-	-
3	-	-
4	-	-
5	-	-
6	-	-
7	-	-
8	-	-
9	-	-
10	-	-

ARCHITECT/ENGINEER FIRM INFO:
seibert architects
1373 5th Street · Sarasota, FL
34236-4915 - seibertarchitects.com
T 941.366.9161 · F 941.365.0902
Lic. AA-C000070

ARCHITECT/ENGINEER/DESIGN PROF. OF RECORD:
WILLIAM J. CRAIG, AIA AR99330

CONC. FC
8" PVC TL
SAND —
6" DIAME

KEY PLAN:

6" DIAME
CONC. FC
8" PVC TL
SAND —

PROJECT INFORMATION:
MCINTOSH MIDDLE SCHOOL
NEW AGRICULTURAL CENTER

651 MCINTOSH ROAD
SARASOTA FL 34240

SHEET DESCRIPTION:
BUILDING 19
DETAILS

DATE PRINTED: -
CAD DWG FILE: -
SHEET: 4 OF: 105

A-500-19

These plans are protected by Federal Copyright protection. Unauthorized replication, use, or distribution may result in infringement or legal action. THIS SHEET SIZE IS 24X36 - PRINTING TO OTHER SIZES WILL NOT BE TO SCALE